ОБЩЕСТВО С ОГРАНИЧЕННОЙ ОТВЕТСТВЕННОСТЬЮ

alabuga DEVELOPMENT

№ СРО-П-114-14012010

Заказчик – АО «ОЭЗ ППТ «Алабуга»

Инфраструктура индустриального парка «Этилен-600», Железнодорожная инфраструктура.

Этап №5. Строительство железнодорожных путей необщего пользования (приемоотправочный парк ст. Круглое Поле)

РАБОЧАЯ ДОКУМЕНТАЦИЯ

Генеральный план.

1439/2025/5-ГП

2026 г.

ОБЩЕСТВО С ОГРАНИЧЕННОЙ ОТВЕТСТВЕННОСТЬЮ

№ СРО-П-114-14012010

Заказчик – АО «ОЭЗ ППТ «Алабуга»

Инфраструктура индустриального парка «Этилен-600», Железнодорожная инфраструктура.

Этап №5. Строительство железнодорожных путей необщего пользования (приемоотправочный парк ст. Круглое Поле)

РАБОЧАЯ ДОКУМЕНТАЦИЯ

Генеральный план.

1439/2025/5-ГП

Главный инженер Мезенцев Д.В.

2026 г.

Общество с ограниченной ответственностью
«ГрадоПроект»

Инфраструктура индустриального парка «Этилен-600», Железнодорожная инфраструктура.

Этап №5. Строительство железнодорожных путей необщего пользования (приемоотправочный парк ст. Круглое Поле)

РАБОЧАЯ ДОКУМЕНТАЦИЯ

Генеральный план.

1439/2025/5-ГП

Директор **И. А. Трубицин**

Главный инженер проекта **В. В. Сундеев**

2026 г.

Ведомость рабочих чертежей основного комплекта

Лист	Наименование	Примечание
1	Общие данные	
2.1	Разбивочный план (1:500). Площадка в районе четной горловины проектируемого Парка. Пути необщего пользования	
2.2	Разбивочный план (1:500). Площадка в районе нечетной горловины проектируемого Парка. Пути необщего пользования	
2.3	Разбивочный план (1:500). Площадка водоподготовки	
2.4	Разбивочный план (1:500). Площадка локальных очистных сооружений	
3.1	План организации рельефа (1:500). Площадка в районе четной горловины проектируемого Парка. Пути необщего пользования	
3.2	План организации рельефа (1:500). Площадка в районе нечетной горловины проектируемого Парка. Пути необщего пользования	
3.3	План организации рельефа (1:500). Площадка водоподготовки	
3.4	План организации рельефа (1:500). Площадка локальных очистных сооружений	
4.1	План земляных масс (1:500). Площадка в районе четной горловины проектируемого Парка. Пути необщего пользования	
4.2	План земляных масс (1:500). Площадка в районе нечетной горловины проектируемого Парка. Пути необщего пользования	
4.3	План земляных масс (1:500). Площадка водоподготовки	
4.4	План земляных масс (1:500). Площадка локальных очистных сооружений	
5.1	Сводный план сетей инженерно-технического обеспечения (1:500). Площадка в районе четной горловины проектируемого Парка. Пути необщего пользования	
5.2	Сводный план сетей инженерно-технического обеспечения (1:500). Площадка в районе нечетной горловины проектируемого Парка. Пути необщего пользования	
5.3	Сводный план сетей инженерно-технического обеспечения (1:500). Площадка водоподготовки	
5.4	Сводный план сетей инженерно-технического обеспечения (1:500). Площадка локальных очистных сооружений	
6.1	План благоустройства (1:500). Площадка в районе четной горловины проектируемого Парка. Пути необщего пользования	
6.2	План благоустройства (1:500). Площадка в районе нечетной горловины проектируемого Парка. Пути необщего пользования	
6.3	План благоустройства (1:500) Площадка водоподготовки	
6.4	План благоустройства (1:500). Площадка локальных очистных сооружений	

Ведомость ссылочных и прилагаемых документов

Обозначение	Наименование	Примечание
	Ссылочные документы	
ГОСТ 32824-2014	Дороги автомобильные общего пользования. Песок природный	
ГОСТ 58406.2-2020	Дороги автомобильные общего пользования. Смеси горячие асфальтобетонные и асфальтобетон	
ГОСТ 32703-2014	Дороги автомобильные общего пользования. Щебень и гравий из плотных горных пород для строительных работ	
ГОСТ 32961-2014	Дороги автомобильные общего пользования. Камни бортовые	
ГОСТ 6665-91	Камни бетонные и железобетонные бортовые	
ГОСТ 32945-2014	Дороги автомобильные общего пользования. Знаки дорожные	

Общие указания

1 Рабочая документация разработана на основании задания на разработку проектно-сметной документации «Инфраструктура индустриального парка «Этилен-600», Железнодорожная инфраструктура. Этап №5. Строительство железнодорожных путей необщего пользования (приемоотправочный парк ст. Круглое Поле)

2 Рабочие чертежи разработаны в соответствии действующими нормами, правилами и стандартами, действующими на территории Российской Федерации:

- СП 18.13330.2019 "Генеральные планы промышленных предприятий. Актуализированная редакция СНиП II-89-80*";
- СП 4.131.30.2013 «Системы противопожарной защиты. Ограничение распространения пожара на объектах защиты. Требования к объемно-планировочным и конструктивным решениям»;
- СП 34.13330.2021 «Автомобильные дороги»;
- СП 34.13330.2012 «Промышленный транспорт»;
- ГОСТ 21.508-2020 «СПДС. Правила выполнения рабочей документации генеральных планов предприятий, сооружений и жилищно-гражданских объектов»;
- ГОСТ Р 21.101-2020 «Основные требования к проектной и рабочей документации»;
- СанПин 2.2.1/2.1.1.1200-03 «Санитарно-защитные зоны и санитарная классификация предприятий, сооружений и иных объектов»;
- ПУЭ «Правила устройства электроустановок. Издание 7».

3 В качестве подосновы для выполнения чертежей использована топографическая съемка участка, выполненная ООО "Геодезия Кадастр Изыскания" в 2026 г.

4 Система высот Балтийская 1977 г.

5 Система координат МСК-16.

6 Основные виды работ, для которых необходимо составлять акты на скрытые работы:

- снятие растительного слоя;
- укладка геотекстиля и геосетки;
- послойная отсыпка, послойное уплотнение, планировка земляного полотна и корыта;
- уплотнение и планировка обочин и откосов, засев трав при укреплении;
- засыпка коммуникаций и сооружений;
- сооружение каждого конструктивного слоя основания;
- сооружение каждого конструктивного слоя покрытия.

Взам. инв. №


Подп. и дата

Инв. № подл.

Изм.	Кол.уч	Лист	№док.	Подпись	Дата	1439/2025/5-ГП-1			
						Инфраструктура индустриального парка «Этилен-600», Железнодорожная инфраструктура. Этап №5. Строительство железнодорожных путей необщего пользования (приемоотправочный парк ст. Круглое Поле)			
Разраб.		Бурайкин			09.26	Этап №5	Стадия	Лист	Листов
Проверил		Сундеев			09.26		Р	1	21
Н. контр.		Грошев			09.26	Общие данные	ГРАДО ПРОЕКТ		

Формат А4х3

Площадка в районе четной горловины проектируемого Парка. Пути необщего пользования

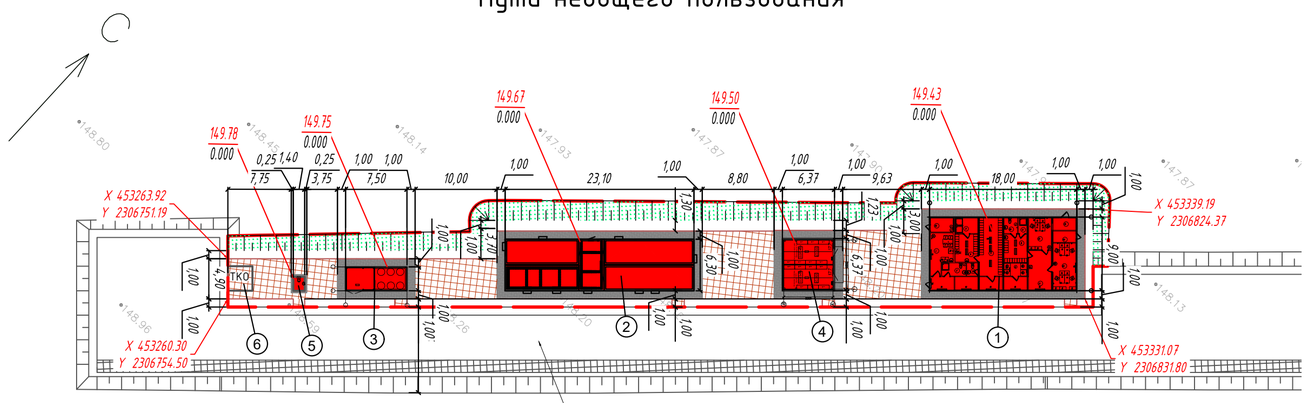


Экспликация зданий и сооружений

Номер на плане	Наименование	Примечание
1	Административно-бытовой модуль	Проектируемое
2	Мобильный комплекс железнодорожной Автоматики, телемеханики и связи (МК АТС)	Проектируемое
3	Модульная компрессорная	Проектируемое
4	Кладовая для хранения путевого инструмента и материалов ВСП	Проектируемое
5	Туалетный модуль 1.4х1.7	Проектируемое
6	ТКО	Проектируемое

Условные обозначения


	Граница проектирования благоустройства
	Проектируемое здание
	Откос
	Бортовой камень БР100.20.8
	Бровка земляного полотна

Тип 1. Тротуар

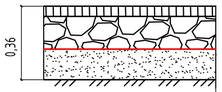


Покрытие: асфальтобетон А5Вл по ГОСТ 58406.2-2020 на битуме PG 64-22 вяжущее по ГОСТ 58400.1-2019	-0,05м
Слой основания: щебень М-600 по ГОСТ 32703-2014 фр. 16-31.5мм	-0,16м
Разделяющая прослойка: нетканый геотекстиль предельная прочность не менее 5кН/м, ГОСТ Р 56419-2015	
Дополнительный слой основания: песок очень мелкий по ГОСТ 32824-2014 Кф>1 м/сут	-0,15м

Тип 2. Оттмостка зданий

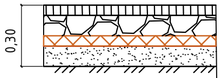


Покрытие: асфальтобетон А5Вл по ГОСТ 58406.2-2020 на битуме PG 64-22 вяжущее по ГОСТ 58400.1-2019	-0,05м
Слой основания: щебень М-600 по ГОСТ 32703-2014 фр. 16-31.5мм	-0,10м
Гидроизоляция	
Утеплитель ЭППС	-0,05м
Дополнительный слой основания: песок очень мелкий по ГОСТ 32824-2014 Кф>1 м/сут	-0,10м


Установка бортового камня БР100.20.8 в сопряжении отмостки и газона

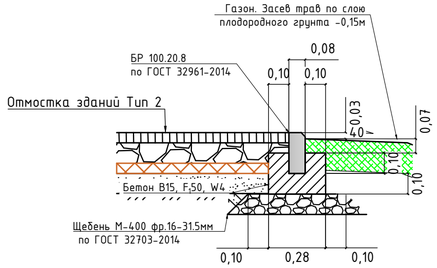

Установка бортового камня БР100.20.8 в сопряжении тротуара и газона

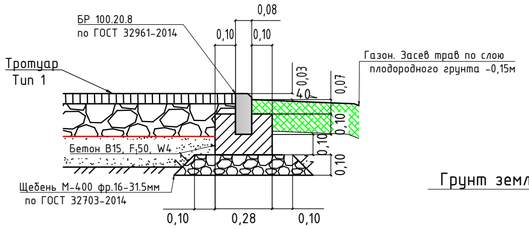

Укрепление откосов

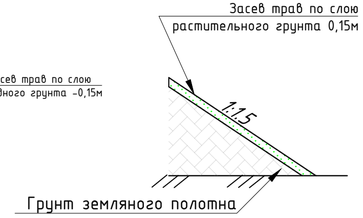

1. Система высот Балтийская 1977 г.
2. Система координат местная.
3. Размеры даны в метрах

Изм.	Колуч	Лист	№док.	Подпись	Дата	1439/2025/5-ГП-2.1			
						Инфраструктура индустриального парка «Этилен-600», Железнодорожная инфраструктура. Этап №5. Строительство железнодорожных путей необщего пользования (приемоотправочный парк ст. Круглое Поле)			
Разраб.		Бурайкин			09.26	Этап №5	Стадия	Лист	Листов
Проверил		Сундеев			09.26		Р	2.1	
Н. контр.		Грошев			09.26	Разбивочный план М 1:500. Площадка в районе четной горловины проектируемого Парка. Пути необщего пользования	ГРАДО ПРОЕКТ		


Взам. инв. №

Подп. и дата


Инв. № подл.

Формат А4х3


Площадка в районе нечетной горловины проектируемого Парка. Пути необщего пользования

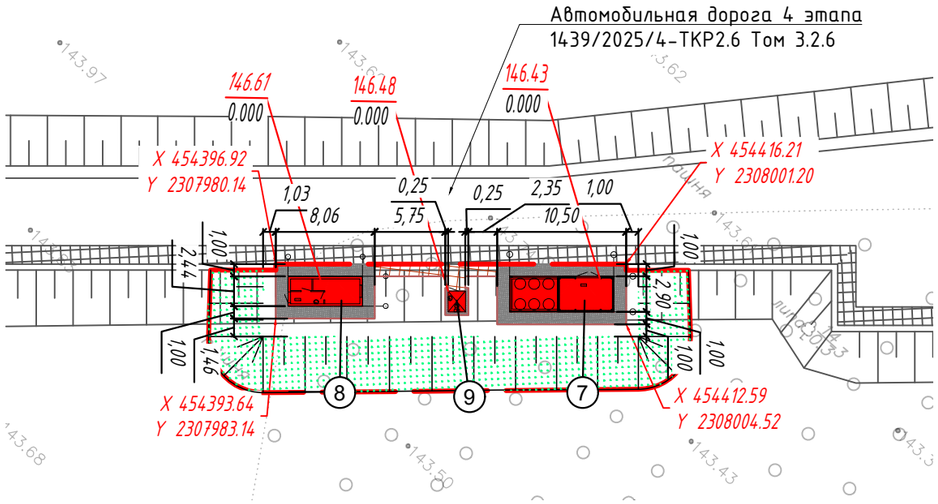

Установка бортового камня БР100.20.8 в сопряжении тротуара и газона

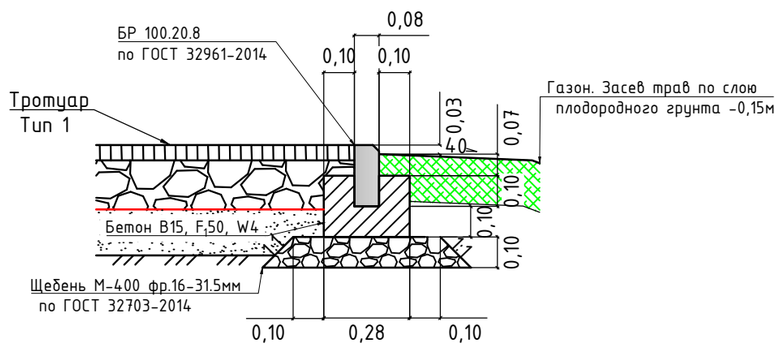

Установка бортового камня БР100.20.8 в сопряжении отмостки и газона

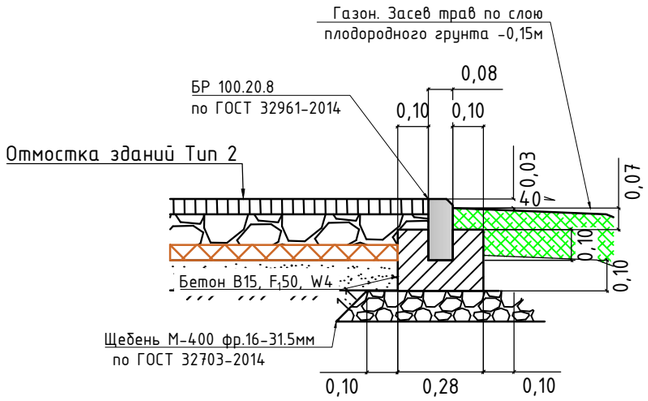


Экспликация зданий и сооружений

Номер на плане	Наименование	Примечание
7	Модульная компрессорная	Проектируемое
8	Модульный пункт обогрева	Проектируемое
9	Туалетный модуль 1.4х1.7	Проектируемое

Условные обозначения


	Граница проектирования благоустройства
	Проектируемое здание
	Откос
	Бортовой камень БР100.20.8
	Бровка земляного полотна

Тип 1. Тротуар

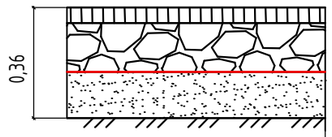


Покрытие: асфальтобетон А5Вл по ГОСТ 58406.2-2020 на битуме PG 64-22 вяжущее по ГОСТ 58400.1-2019	-0,05м
Слой основания: щебень М-600 по ГОСТ 32703-2014 фр. 16-31.5мм	-0,16м
Разделяющая прослойка: нетканый геотекстиль предельная прочность не менее 5кН/м, ГОСТ Р 56419-2015	
Дополнительный слой основания: песок очень мелкий по ГОСТ 32824-2014 Кф>1 м/сут	-0,15м

Тип 2. Отмостка зданий

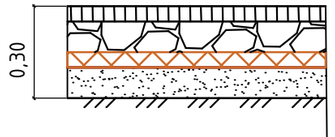

Покрытие: асфальтобетон А5Вл по ГОСТ 58406.2-2020 на битуме PG 64-22 вяжущее по ГОСТ 58400.1-2019	-0,05м
Слой основания: щебень М-600 по ГОСТ 32703-2014 фр. 16-31.5мм	-0,10м
Гидроизоляция	
Утеплитель ЭППС	-0,05м
Дополнительный слой основания: песок очень мелкий по ГОСТ 32824-2014 Кф>1 м/сут	-0,10м

Укрепление откосов

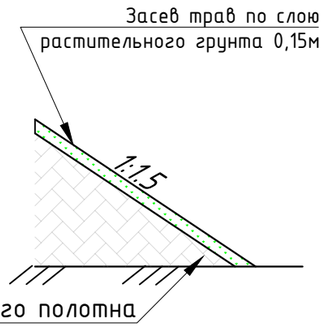

1. Система высот Балтийская 1977 г.
2. Система координат местная.
3. Размеры даны в метрах

Изм.	Кол.уч	Лист	N°док.	Подпись	Дата
Разраб.		Бурайкин			09.26
Проверил		Сундеев			09.26
Н. контр.		Грошев			09.26

1439/2025/5-ГП-2.2

Инфраструктура индустриального парка «Этилен-600», Железнодорожная инфраструктура. Этап №5. Строительство железнодорожных путей необщего пользования (приемоотправочный парк ст. Круглое Поле)

Стадия	Лист	Листов
Р	2.2	

Этап №5

Разбивочный план М 1:500. Площадка в районе нечетной горловины проектируемого Парка. Пути необщего пользования

ГРАДО ПРОЕКТ


Взам. инв. N°

Подп. и дата


Инв. N° подл.

Формат А3

Площадка Водоподготовки

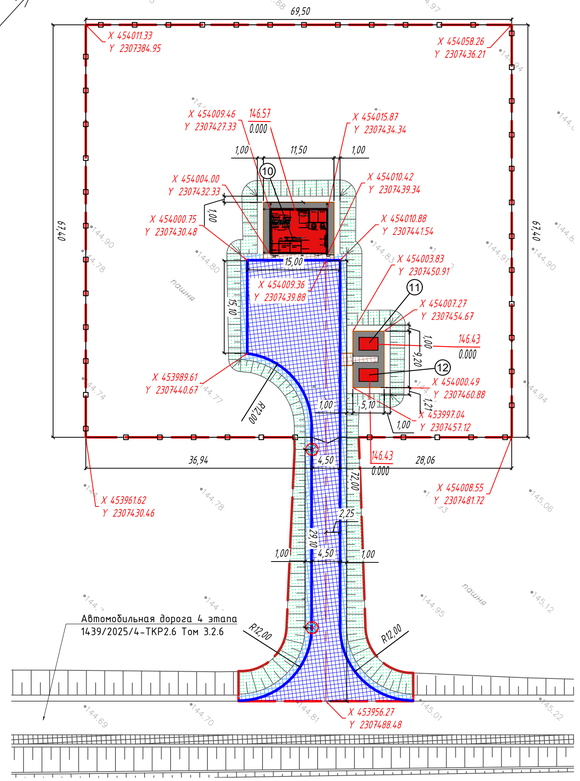


Тип 2. Отмостка зданий

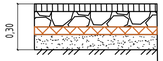


Покрытие: асфальтобетон А5Вл по ГОСТ 58406.2-2020 на битуме PG 64-22 вяжущее по ГОСТ 58400.1-2019	-0,05м
Слой основания: щебень М-600 по ГОСТ 32703-2014 фр. 16-31.5мм	-0,10м
Гидроизоляция	
Утеплитель ЭППС	-0,05м
Дополнительный слой основания: песок очень мелкий по ГОСТ 32824-2014 Кф>1 м/сут	-0,10м

Тип 1. Тротуар

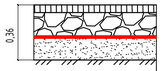


Покрытие: асфальтобетон А5Вл по ГОСТ 58406.2-2020 на битуме PG 64-22 вяжущее по ГОСТ 58400.1-2019	-0,05м
Слой основания: щебень М-600 по ГОСТ 32703-2014 фр. 16-31.5мм	-0,16м
Разделяющая прослойка: нетканый геотекстиль предельная прочность не менее 5кН/м, ГОСТ Р 56419-2015	
Дополнительный слой основания: песок очень мелкий по ГОСТ 32824-2014 Кф>1 м/сут	-0,15м


Установка бортового камня БР100.20.8 в сопряжении тротуара и газона

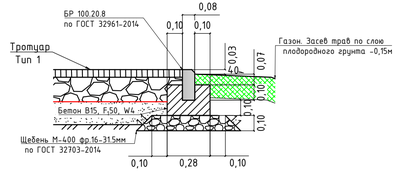

Установка бортового камня БР100.20.8 в сопряжении отмостки и газона

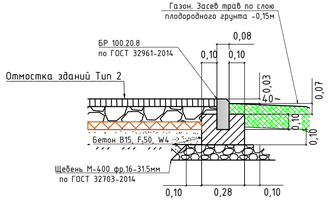


Тип 3. Асфальтобетонный проезд

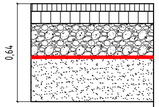

Верхний слой покрытия – Асфальтобетон А16$В_{Щ}$ по ГОСТ Р 58406.2-2020 на битумном вяжущем PG 64-34 по ГОСТ Р 58400.1-2019	-0,05м
Нижний слой покрытия – Асфальтобетон А32$Н_{Ц}$ по ГОСТ Р 58406.2-2020 на битумном вяжущем PG 64-34 по ГОСТ Р 58400.1-2019	-0,08м
Слой основания – Щебень фракционированный фракции св. 31,5–63 мм М600 с расклинцовкой верхнего слоя щебнем фр. 4–8мм. и фр. 8–16мм М600 по ГОСТ 32703-2014 уложенный в один слой	-0,22м
Разделяющая прослойка – нетканый геотекстиль предельная прочность не менее 5кН/м, ГОСТ Р 56419-2015	
Дополнительный слой основания – Песок мелкий по ГОСТ 32824-2014 с коэф. фильтрации Кф>2 м/сут.	-0,29м
Грунт рабочего слоя – глина	

Поперечный разрез асфальтобетонного проезда Тип 3 М 1:50

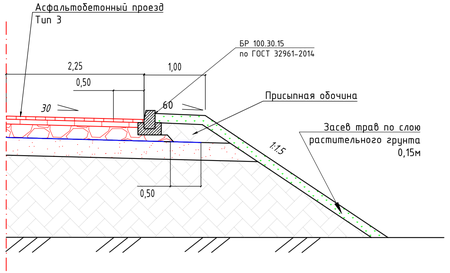

Укрепление откосов



1. Система высот Балтийская 1977 г.
2. Система координат местная.
3. Размеры даны в метрах

Экспликация зданий и сооружений

Номер на плане	Наименование	Примечание
10	Водоподготовка	Проектируемое
11, 12	Трансформаторная подстанция	Проектируемое

Условные обозначения

	Граница проектирования благоустройства
	Проектируемое здание
	Откос
	Бортовой камень БР100.30.15
	Бортовой камень БР100.20.8
	Бровка земляного полотна
	Ось проезда
	Дождеприемный колодец
	Ограждение L=269,30 м
	Ворота распашные 4,5 м

Примечание:

1. Все размеры даны в метрах, поперечные уклоны в промилле.
2. Дорожно-климатическая зона – II_2.
3. Тип дорожной одежды – облегченный.
4. Перед устройством асфальтобетонных покрытий (оснований) по основаниям из щебня производится розлив битумной эмульсии по ГОСТ Р 58952.1-2020 ЭБДК-Б из расчета 0,7л/м^2.
5. Перед устройством асфальтобетонных покрытий по асфальтобетонным покрытиям (основаниям) производится розлив битумной эмульсии по ГОСТ Р 58952.1-2020 ЭБДК-Б из расчета 0,3 л/м^2.
6. Расчет прочности дорожной одежды выполнен по ГОСТ Р 71404-2024.
7. Класс асфальтобетона А16Вн по истираемости не ниже 2.
8. Марка щебня по сопротивлению истираемости по показателю микро-Деваль для приготовления А16Вн – МД2 или МД1.
9. Марка щебня по дробимости, для устройства оснований, не менее М600.

						1439/2025/5-ГП-2.3	
						Инфраструктура индустриального парка «Этилен-600», Железнодорожная инфраструктура. Этап №5. Строительство железнодорожных путей необщего пользования (приемоотправочный парк ст. Круглое Поле)	
Изм.	Кол.уч	Лист	№док	Подпись	Дата		
Разраб.		Бурайкин			09.26	Этап №5	Стадия: Р; Лист: 2.3; Листов:
Проверил		Сундеев			09.26		
Н. контр.		Грошев			09.26	Разбивочный план М 1:500. Площадка водоподготовки	ГРАДО ПРОЕКТ


Взам. инв. №

Подп. и дата


Инв. № подл.

Формат А4х4

Площадка локальных очистных сооружений

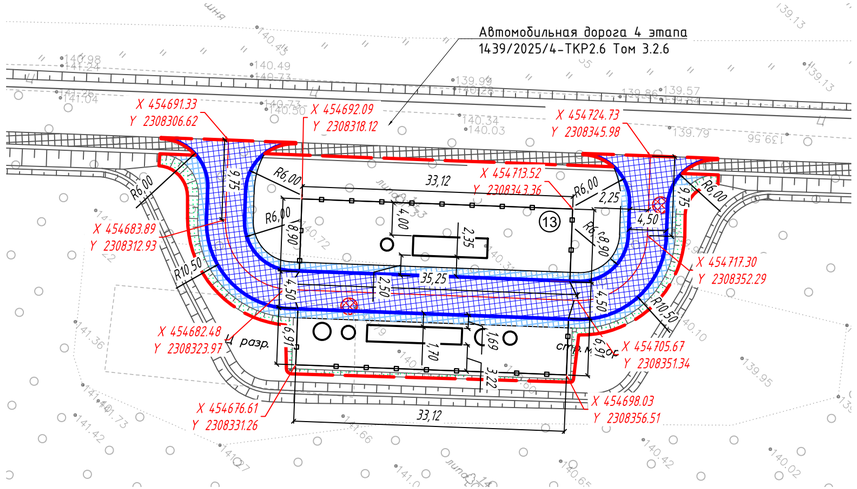

Тип 3. Асфальтобетонный проезд

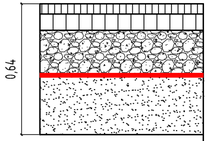

Верхний слой покрытия - Асфальтобетон А16$В_Н$ по ГОСТ Р 58406.2-2020 на битумном вяжущем PG 64-34 по ГОСТ Р 58400.1-2019	-0,05м
Нижний слой покрытия - Асфальтобетон А32$Н_Н$, по ГОСТ Р 58406.2-2020 на битумном вяжущем PG 64-34 по ГОСТ Р 58400.1-2019	-0,08м
Слой основания - Щебень фракционированный фракции св. 31,5-63 мм М600 с расклинцовкой верхнего слоя щебнем фр. 4-8мм. и фр. 8-16мм М600 по ГОСТ 32703-2014 уложенный в один слой	-0,22м
Разделяющая прослойка - нетканый геотекстиль предельная прочность не менее 5кН/м, ГОСТ Р 56419-2015	
Дополнительный слой основания - Песок мелкий по ГОСТ 32824-2014 с коэф. фильтрации Кф>2 м/сут.	-0,29м
Грунт рабочего слоя - глина	


Экспликация зданий и сооружений

Номер на плане	Наименование	Примечание
13	Локальные очистные сооружения (ЛОС)	Проектируемое


Условные обозначения

	Граница проектирования благоустройства
	Проектируемые сооружения
	Откос
	Бортовой камень БР100.30.15
	Бровка земляного полотна
	Ось проезда
	Ограждение l=97,90 м
	Ворота распашные 4,5 м

Поперечный разрез асфальтобетонного проезда Тип 3 М 1:50

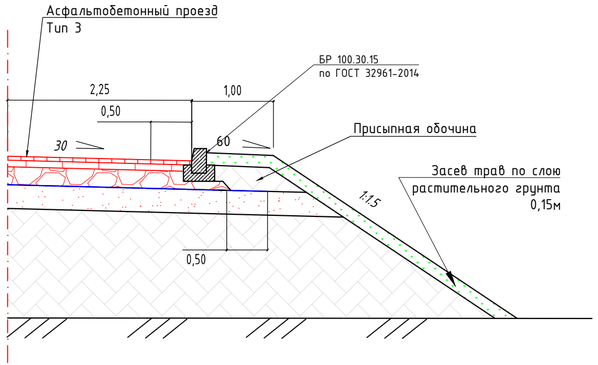

Укрепление откосов

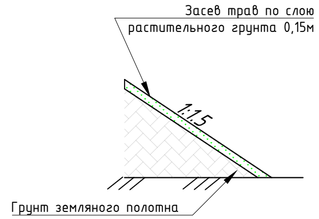


Примечание:
1. Все размеры даны в метрах, поперечные уклоны в промилле.
2. Дорожно-климатическая зона - II_2.
3. Тип дорожной одежды - облегченный.
4. Перед устройством асфальтобетонных покрытий (оснований) по основаниям из щебня производится розлив битумной эмульсии по ГОСТ Р 58952.1-2020 ЭБДК-Б из расчета 0,7л/м^2.
5. Перед устройством асфальтобетонных покрытий по асфальтобетонным покрытиям (основаниям) производится розлив битумной эмульсии по ГОСТ Р 58952.1-2020 ЭБДК-Б из расчета 0,3 л/м^2.
6. Расчет прочности дорожной одежды выполнен по ГОСТ Р 71404-2024.
7. Класс асфальтобетона А16Вн по истираемости не ниже 2.
8. Марка щебня по сопротивлению истираемости по показателю микро-Деваль для приготовления А16Вн - МД2 или МД1.
9. Марка щебня по дробимости, для устройства оснований, не менее М600.

Изм.	Кол.уч	Лист	N°док.	Подпись	Дата	1439/2025/5-ГП-2.4			
						Инфраструктура индустриального парка «Этилен-600», Железнодорожная инфраструктура. Этап №5. Строительство железнодорожных путей необщего пользования (приемоотправочный парк ст. Круглое Поле)			
Разраб.		Бурайкин			09.26	Этап №5	Стадия	Лист	Листов
Проверил		Сундеев			09.26		Р	2.4	
Н. контр.		Грошев			09.26	Разбивочный план М 1:500. Площадка локальных очистных сооружений	ГРАДО ПРОЕКТ		

Взам. инв. N°
Подп. и дата
Инв. N° подл.

Формат А4х3

Площадка в районе четной горловины проектируемого Парка. Пути необщего пользования

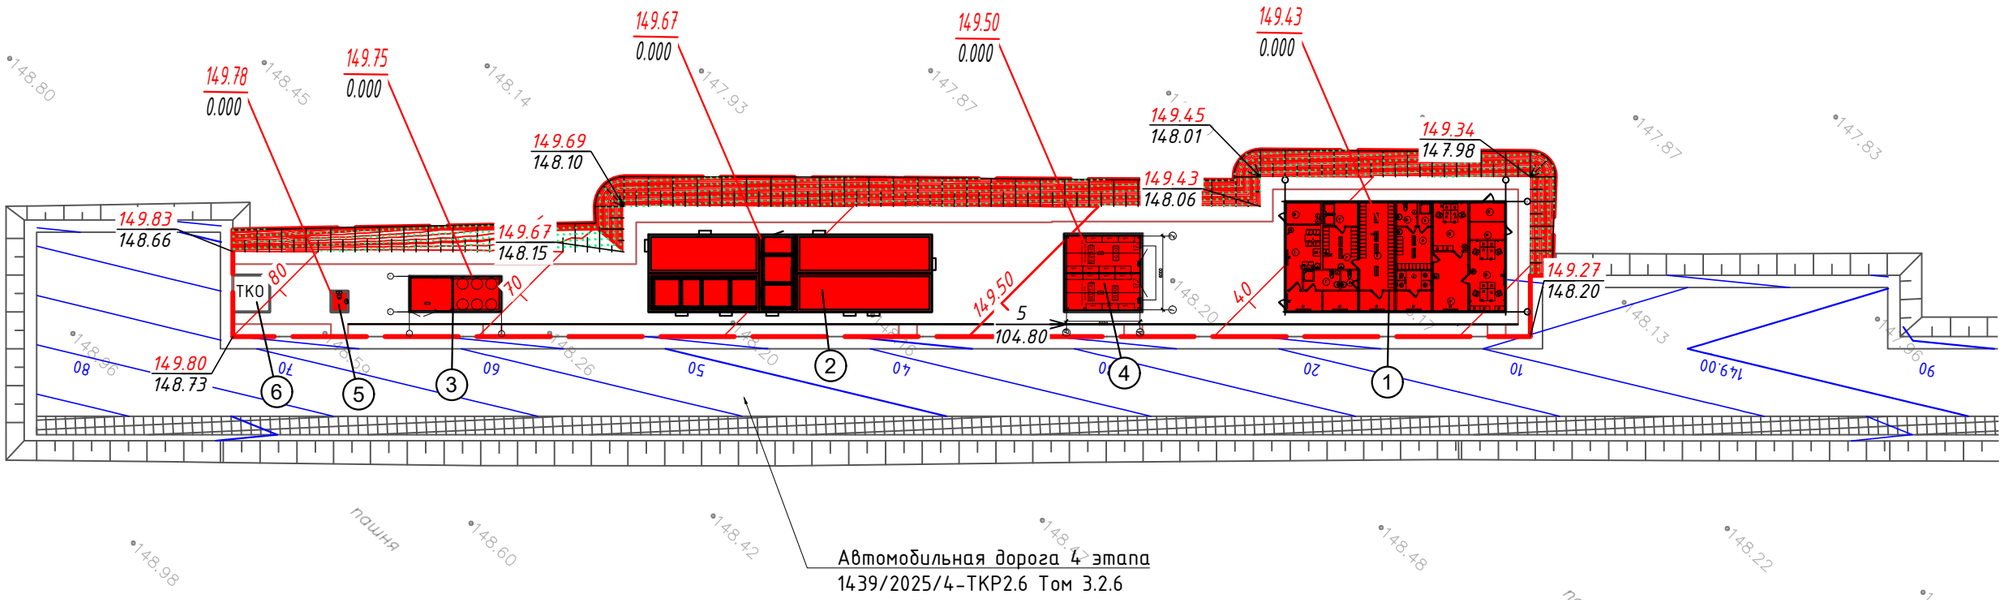

Экспликация зданий и сооружений

Номер на плане	Наименование	Примечание
1	Административно-бытовой модуль	Проектируемое
2	Мобильный комплекс железнодорожной Автоматики, телемеханики и связи (МК АТС)	Проектируемое
3	Модульная компрессорная	Проектируемое
4	Кладовая для хранения путевого инструмента и материалов ВСП	Проектируемое
5	Туалетный модуль 1.4х1.7	Проектируемое
6	ТКО	Проектируемое

Условные обозначения

	Граница проектирования благоустройства
	Проектируемое здание
	Откос
	Бортовой камень БР100.20.8
	Бровка земляного полотна
	Проектная горизонталь
	Проектная горизонталь АД 4 этапа 1439/2025/4-ТКР2.6 Том 3.2.6
5 / 104.80	Направление уклона проектируемого рельефа
149.94 / 147.98	Отметка поверхности (проектная / существующая)


1. Система высот Балтийская 1977 г.
2. Система координат местная.
3. Отметки и уклоноуказатели приведены по верху покрытия.

Изм.	Кол.уч	Лист	N°док.	Подпись	Дата	1439/2025/5-ГП-3.1			
						Инфраструктура индустриального парка «Этилен-600», Железнодорожная инфраструктура. Этап №5. Строительство железнодорожных путей необщего пользования (приемоотправочный парк ст. Круглое Поле)			
Разраб.		Бурайкин			09.26	Этап №5	Стадия	Лист	Листов
Проверил		Сундеев			09.26		Р	3.1	
Н. контр.		Грошев			09.26	План организации рельефа М 1:500. Площадка в районе четной горловины проектируемого Парка. Пути необщего пользования	ГРАДО ПРОЕКТ		

Взам. инв. N° | Подп. и дата | Инв. N° подл.

Формат А3

Площадка в районе нечетной горловины проектируемого Парка. Пути необщего пользования

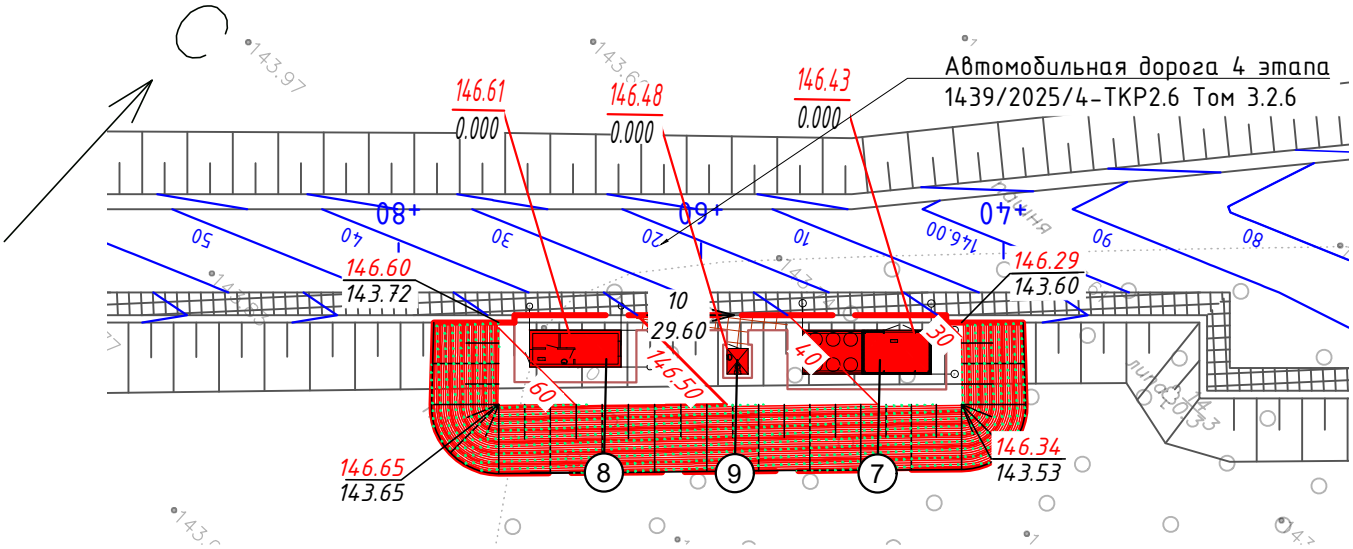

1. Система высот Балтийская 1977 г.
2. Система координат местная.
3. Отметки и уклоноуказатели приведены по верху покрытия.

Экспликация зданий и сооружений

Номер на плане	Наименование	Примечание
7	Модульная компрессорная	Проектируемое
8	Модульный пункт обогрева	Проектируемое
9	Туалетный модуль 1.4х1.7	Проектируемое

Условные обозначения

	Граница проектирования благоустройства
	Проектируемое здание
	Откос
	Бортовой камень БР100.20.8
	Бровка земляного полотна
	Проектная горизонталь
	Проектная горизонталь АД 4 этапа 1439/2025/4-ТКР2.6 Том 3.2.6
10 / 29.60	Направление уклона проектируемого рельефа
146.34 / 143.53	Отметка поверхности (проектная / существующая)

Взам. инв. №

Подп. и дата

Инв. № подл.

Изм.	Кол.уч	Лист	№док.	Подпись	Дата
Разраб.		Бурайкин			09.26
Проверил		Сундеев			09.26
Н. контр.		Грошев			09.26

1439/2025/5-ГП-3.2

Инфраструктура индустриального парка «Этилен-600», Железнодорожная инфраструктура. Этап №5. Строительство железнодорожных путей необщего пользования (приемоотправочный парк ст. Круглое Поле)

Этап №5


Стадия	Лист	Листов
Р	3.2	

План организации рельефа М 1:500. Площадка в районе нечетной горловины проектируемого Парка. Пути необщего пользования

ГРАДО ПРОЕКТ

Формат А4

Площадка Водоподготовки

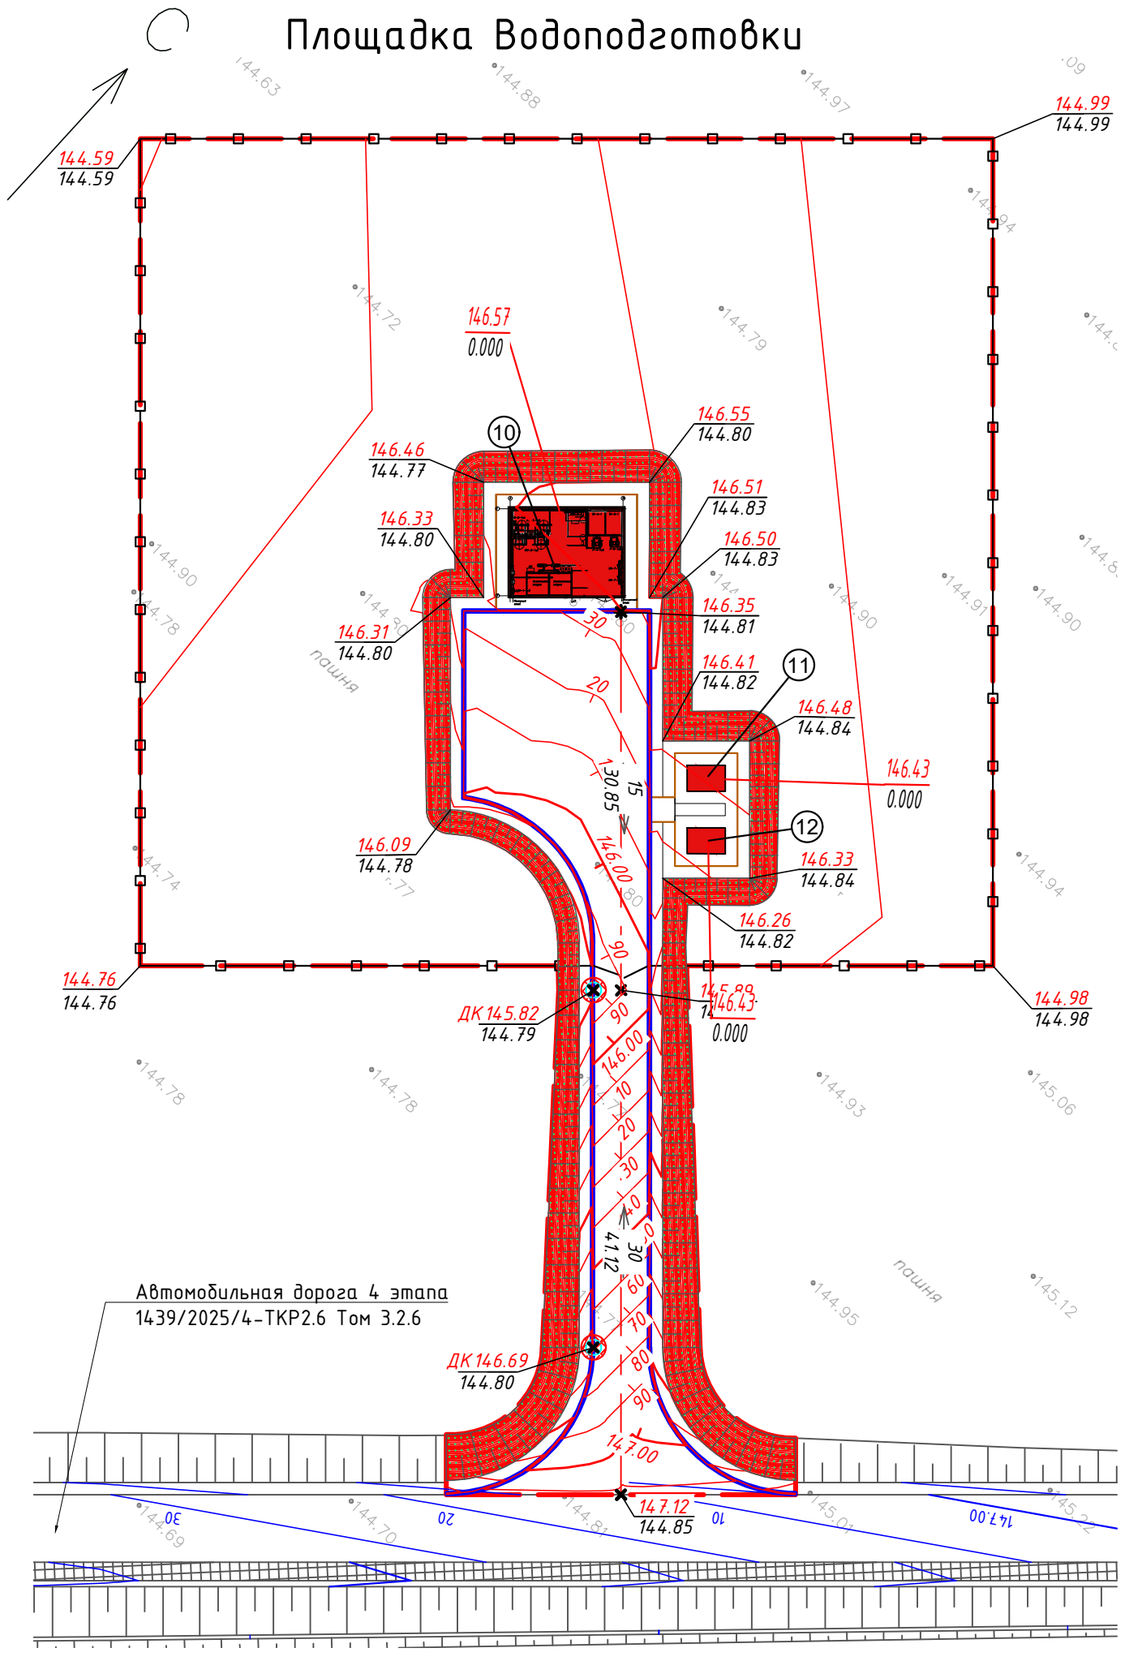

Экспликация зданий и сооружений

Номер на плане	Наименование	Примечание
10	Водоподготовка	Проектируемое
11, 12	Трансформаторная подстанция	Проектируемое

Условные обозначения

	Граница проектирования благоустройства
	Проектируемое здание
	Откос
	Бортовой камень БР100.30.15
	Бортовой камень БР100.20.8
	Бровка земляного полотна
	Ось проезда
	Дождеприемный колодец
	Ограждение l=269,30 м
	Ворота распашные 4,5 м
	Проектная горизонталь
	Проектная горизонталь АД 4 этапа 1439/2025/4-ТКР2.6 Том 3.2.6
15 / 30.85	Направление уклона проектируемого рельефа
146.26 / 144.82	Отметка поверхности (проектная / существующая)
147.12 / 144.85	Точка перелома проектируемого рельефа (проектная / существующая)

1. Система высот Балтийская 1977 г.
2. Система координат местная.
3. Отметки и уклоноуказатели приведены по верху покрытия.

Изм.	Кол.уч	Лист	N°док.	Подпись	Дата
Разраб.		Бурайкин			09.26
Проверил		Сундеев			09.26
Н. контр.		Грошев			09.26

1439/2025/5-ГП-3.3

Инфраструктура индустриального парка «Этилен-600», Железнодорожная инфраструктура. Этап №5. Строительство железнодорожных путей необщего пользования (приемоотправочный парк ст. Круглое Поле)

Стадия	Лист	Листов
Р	3.3	

Этап №5

План организации рельефа М 1:500.
Площадка водоподготовки

ГРАДО ПРОЕКТ


Взам. инв. N°

Подп. и дата

Инв. N° подл.

Формат А3

Площадка локальных очистных сооружений

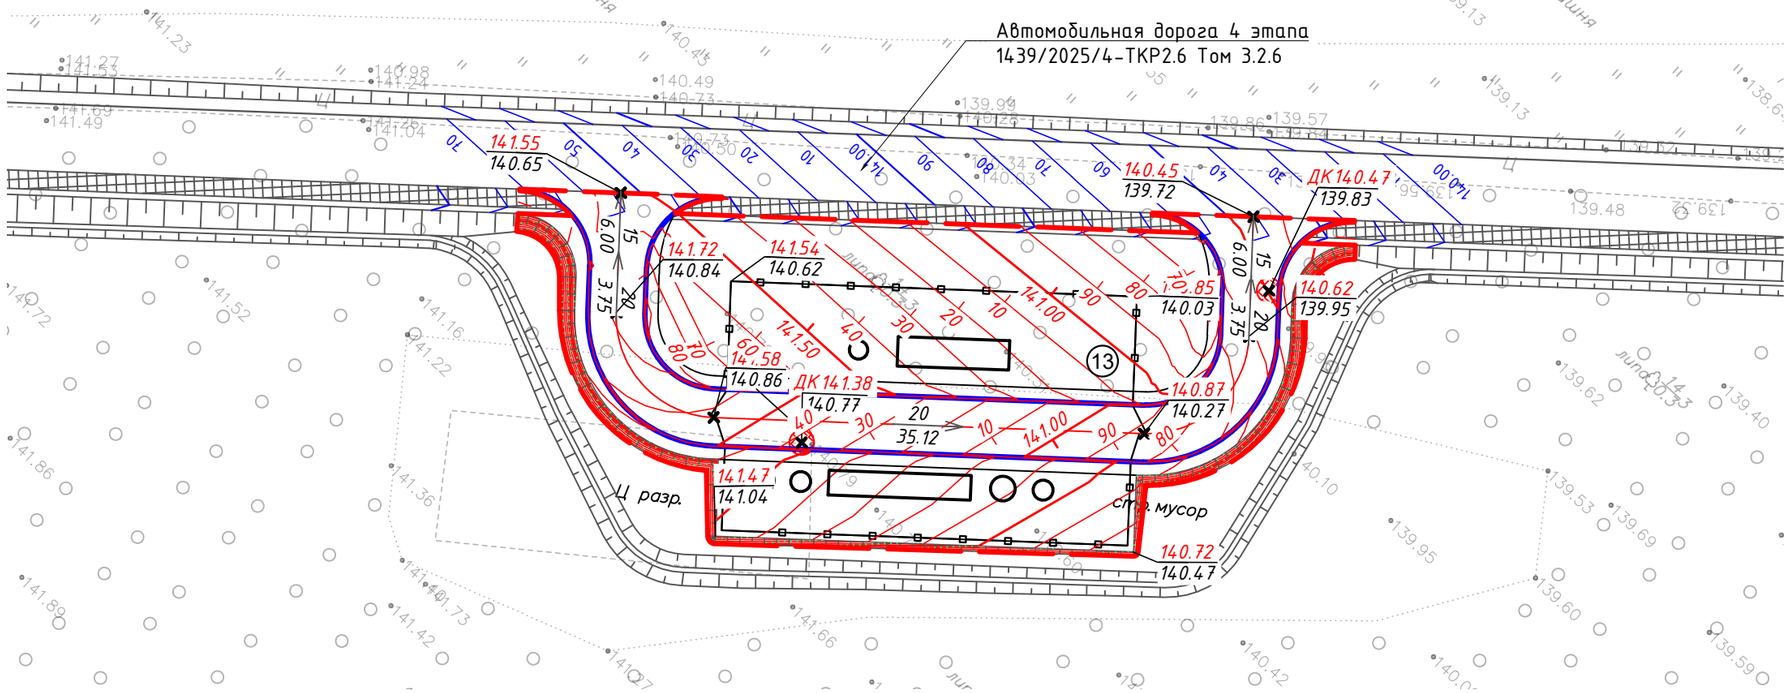

Условные обозначения

	Граница проектирования благоустройства
	Проектируемые сооружения
	Откос
	Бортовой камень БР100.30.15
	Бровка земляного полотна
	Ось проезда
	Дождеприемный колодец
	Ограждение l=97,90 м
	Ворота распашные 4,5 м
	Проектная горизонталь
	Проектная горизонталь АД 4 этапа 1439/2025/4-ТКР2.6 Том 3.2.6
20 / 35.12	Направление уклона проектируемого рельефа
140.87 / 140.27	Отметка поверхности (проектная / существующая)
140.62 / 139.95	Точка перелома проектируемого рельефа (проектная / существующая)

Экспликация зданий и сооружений

Номер на плане	Наименование	Примечание
13	Локальные очистные сооружения (ЛОС)	Проектируемое

1. Система высот Балтийская 1977 г.
2. Система координат местная.
3. Отметки и уклоноуказатели приведены по верху покрытия.

						1439/2025/5-ГП-3.4
						Инфраструктура индустриального парка «Этилен-600», Железнодорожная инфраструктура. Этап №5. Строительство железнодорожных путей необщего пользования (приемоотправочный парк ст. Круглое Поле)
Изм.	Кол.уч	Лист	N°док.	Подпись	Дата	
Разраб.		Бурайкин			09.26	Этап №5
Проверил		Сундеев			09.26	Стадия: Р; Лист: 3.4; Листов:
Н. контр.		Грошев			09.26	План организации рельефа М 1:500. Площадка локальных очистных сооружений

ГРАДО ПРОЕКТ


Взам. инв. N°

Подп. и дата


Инв. N° подл.

Формат А3

Площадка в районе четной горловины проектируемого Парка. Пути необщего пользования

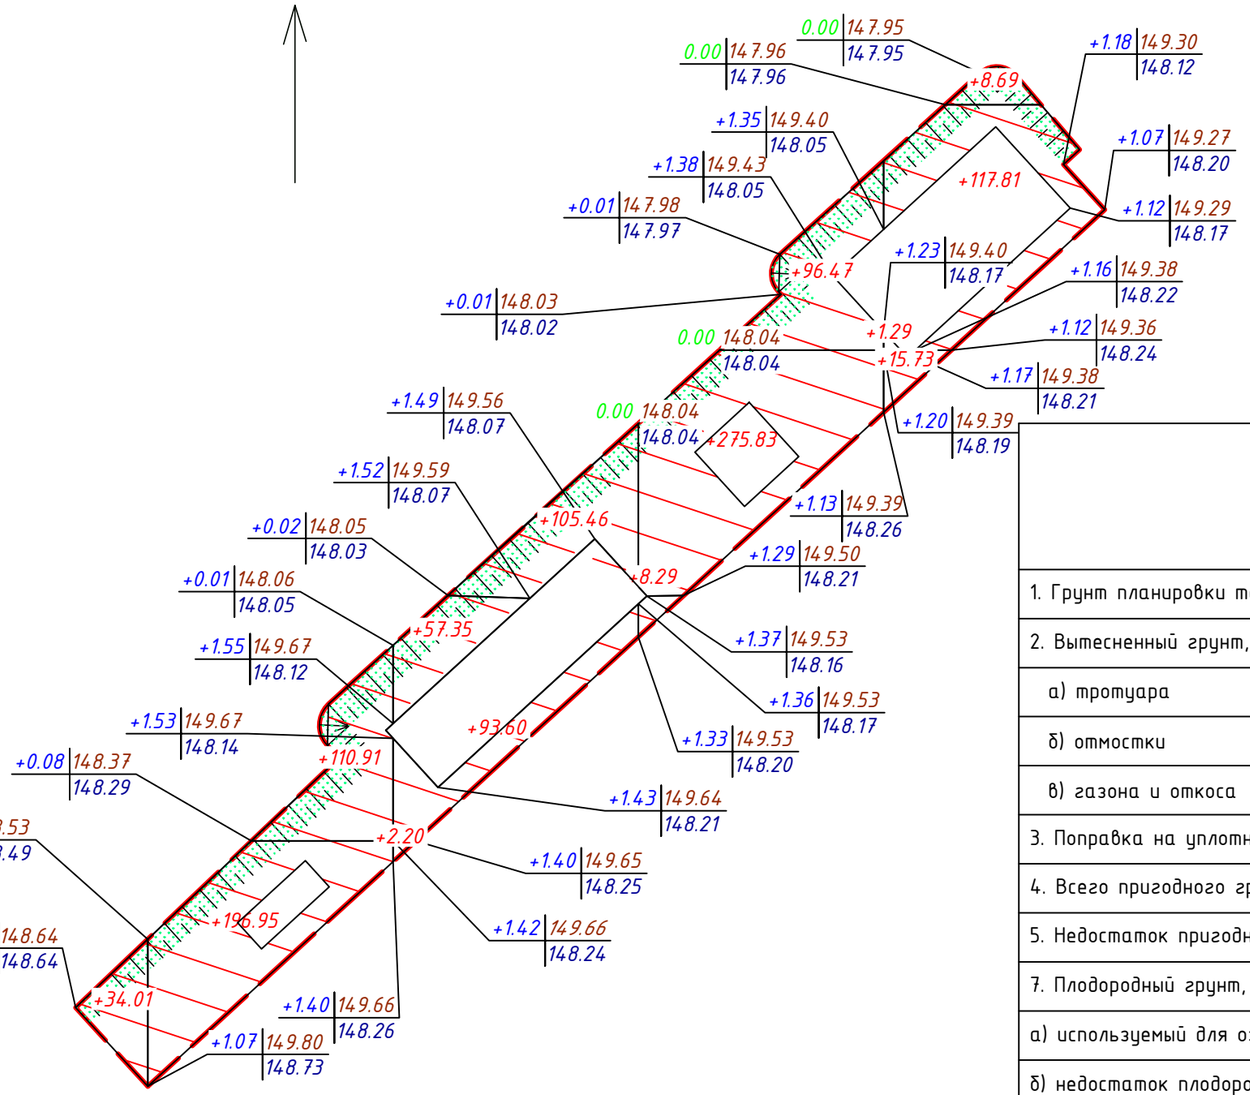

Условные обозначения

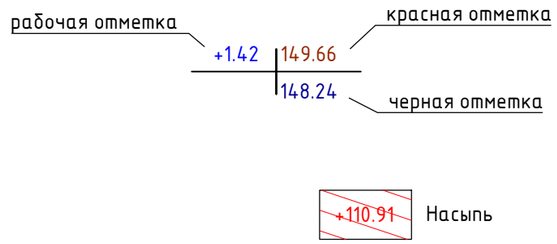

Ведомость объемов земляных масс

Наименование грунта	Количество, м³		Примечание
	Насыпь (+)	Выемка (–)	
1. Грунт планировки территории	1125	–	
2. Вытесненный грунт, в т.ч. при устройстве:		225	
а) тротуара		98	
б) отмостки		53	
в) газона и откоса		74	
3. Поправка на уплотнение, k=0,1	113	–	
4. Всего пригодного грунта	1238	225	
5. Недостаток пригодного грунта		1013	
7. Плодородный грунт, всего:	09.26		
а) используемый для озеленения территории	09.26 74	–	
б) недостаток плодородного грунта		74	
8. Итого перерабатываемого грунта	09.26 1312	1312	

Итого, м³							Всего, м³	
	Насыпь	+34.01	+307.86	+258.61	+380.59	+143.52		+1125
	Выемка	–	–	–	–	–		–

Площадь картограммы – 947.21 м², в т.ч.:
насыпь – 947.21 м², выемка – 0.00 м²

1. Система высот Балтийская 1977 г.
2. Система координат местная.
3. Картограмма разработана в программном комплексе Civil3d.
4. При расчете картограммы квадраты сетки приняты стороной равной 20 м.
5. Необходимость замены грунта под зданиями и сооружениями определена в марке КР.
6. Коэффициент уплотнения – не менее 0,95. Толщина каждого слоя 0,3–0,6 м (уточняется по результатам опытного уплотнения).
7. После возведения земляного полотна откосы необходимо доуплотнять планировщиками-уплотнителями.

Изм.	Кол.уч	Лист	N°док.	Подпись	Дата
Разраб.		Бурайкин			09.26
Проверил		Сундеев			09.26
Н. контр.		Грошев			09.26

1439/2025/5-ГП-4.1

Инфраструктура индустриального парка «Этилен-600», Железнодорожная инфраструктура. Этап №5. Строительство железнодорожных путей необщего пользования (приемоотправочный парк ст. Круглое Поле)

Стадия	Лист	Листов
Р	4.1	

Этап №5

План земляных масс М 1:500. Площадка в районе четной горловины проектируемого Парка. Пути необщего пользования


ГРАДО ПРОЕКТ

Взам. инв. N°
Подп. и дата
Инв. N° подл.

Формат А3

Площадка в районе нечетной горловины проектируемого Парка. Пути необщего пользования

С

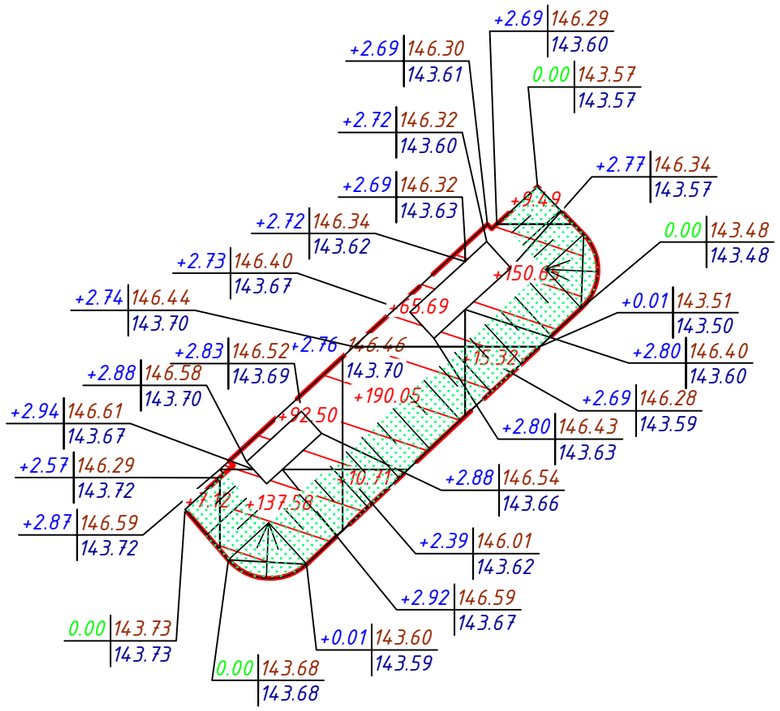

Итого, м³	*Насыпь*	*+7.12*	*+230.08*	*+266.45*	*+175.46*	*Всего, м³*	*+679.11*
	Выемка	–	–	–	–		–

Площадь картограммы – 338.89 м², в т.ч.:
насыпь – 338.89 м², выемка – 0.00 м²

Условные обозначения

рабочая отметка — +2.80 / 143.63 — красная отметка, черная отметка

+150.65 — Насыпь

Ведомость объемов земляных масс

Наименование грунта	Количество, м³		Примечание
	Насыпь (+)	Выемка (–)	
1. Грунт планировки территории	680	–	
2. Вытесненный грунт, в т.ч. при устройстве:		234	
а) тротуара		5	
б) отмостки		15	
в) газона и откоса		214	
3. Поправка на уплотнение, k=0,1	68	–	
4. Всего пригодного грунта	748	234	
5. Недостаток пригодного грунта		514	
7. Плодородный грунт, всего:			
а) используемый для озеленения территории	214	–	
б) недостаток плодородного грунта		214	
8. Итого перерабатываемого грунта	962	962	

1. Система высот Балтийская 1977 г.
2. Система координат местная.
3. Картограмма разработана в программном комплексе Civil3d.
4. При расчете картограммы квадраты сетки приняты стороной равной 10 м.
5. Необходимость замены грунта под зданиями и сооружениями определена в марке КР.
6. Коэффициент уплотнения – не менее 0,95. Толщина каждого слоя 0,3–0,6 м (уточняется по результатам опытного уплотнения).
7. После возведения земляного полотна откосы необходимо доуплотнять планировщиками-уплотнителями.

Изм.	Кол.уч	Лист	N°док.	Подпись	Дата
Разраб.		Бурайкин			09.26
Проверил		Сундеев			09.26
Н. контр.		Грошев			09.26

1439/2025/5-ГП-4.2

Инфраструктура индустриального парка «Этилен-600», Железнодорожная инфраструктура. Этап №5. Строительство железнодорожных путей необщего пользования (приемоотправочный парк ст. Круглое Поле)

Стадия	Лист	Листов
Р	4.2	

Этап №5


План земляных масс М 1:500. Площадка в районе нечетной горловины проектируемого Парка. Пути необщего пользования

ГРАДО ПРОЕКТ

Взам. инв. N° | Подп. и дата | Инв. N° подл.

Формат А3

Площадка Водоподготовки

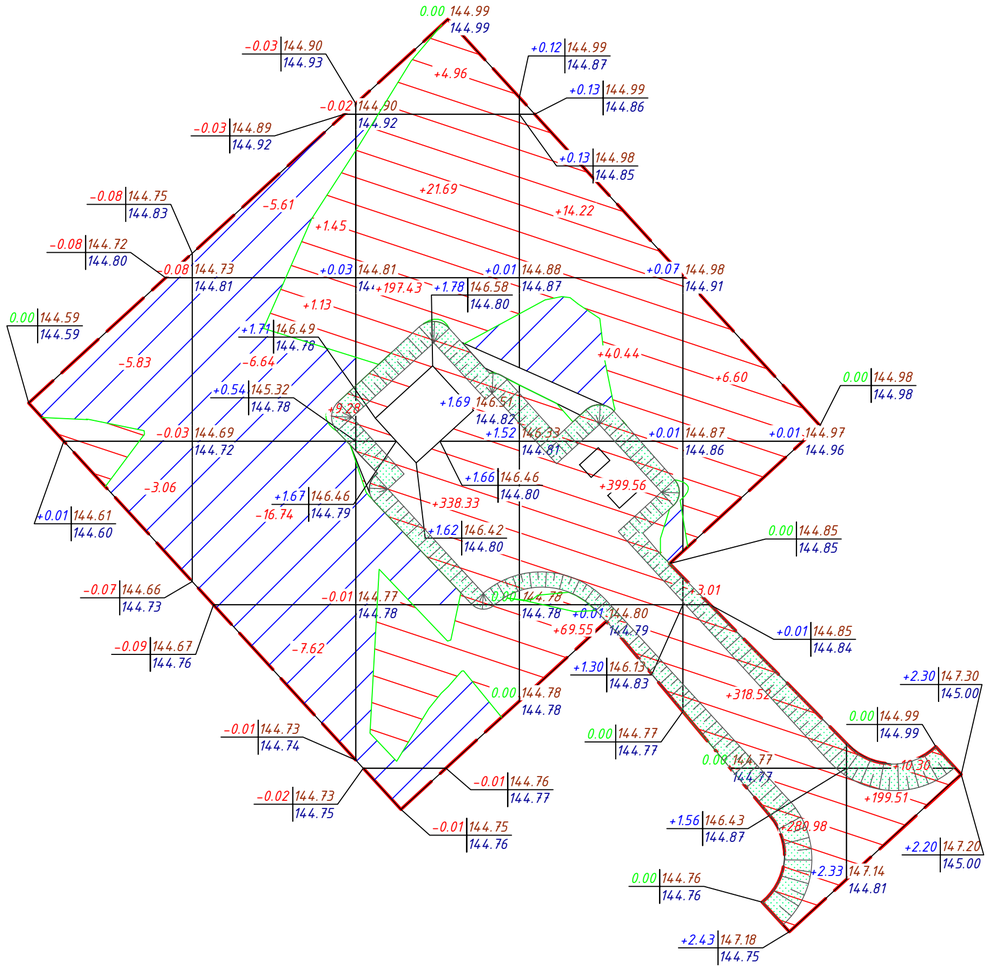


Всего, Итого, $м^3$	Насыпь	–	+11.86	+562.41	+523.77	+609.11	+209.81
	Выемка	-8.89	-36.61	–	–	–	–
	Насыпь	+1916.96	Площадь картограммы – 4337.80 $м^2$, в т.ч.: насыпь – 2959.10 $м^2$, выемка – 1378.70 $м^2$				
	Выемка	-45.50					

Ведомость объемов земляных масс

Наименование грунта	Количество, $м^3$		Приме-чание
	Насыпь (+)	Выемка (–)	
1. Грунт планировки территории	1909	46	
2. Вытесненный грунт, в т.ч. при устройстве:		1332	
а) проезда		575	
б) тротуара		56	
в) отмостки		20	
г) газона и откоса		681	
3. Поправка на уплотнение, k=0,1	191	–	
4. Всего пригодного грунта	2100	1378	
5. Недостаток пригодного грунта		722	
7. Плодородный грунт, всего:			
а) используемый для озеленения территории	681	–	
б) недостаток плодородного грунта		681	
8. Итого перерабатываемого грунта	2781	2781	

Условные обозначения

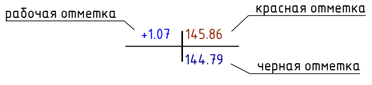

-1.62 Выемка

+319.63 Насыпь

1. Система высот Балтийская 1977 г.
2. Система координат местная.
3. Картограмма разработана в программном комплексе Civil3d.
4. При расчете картограммы квадраты сетки приняты стороной равной 20 м.
5. Необходимость замены грунта под зданиями и сооружениями определена в марке КР.
6. Коэффициент уплотнения – не менее 0,95. Толщина каждого слоя 0,3–0,6 м (уточняется по результатам опытного уплотнения).
7. После возведения земляного полотна откосы необходимо доуплотнять планировщиками-уплотнителями.

						1439/2025/5-ГП-4.3	
						Инфраструктура индустриального парка «Этилен-600», Железнодорожная инфраструктура. Этап №5. Строительство железнодорожных путей необщего пользования (приемоотправочный парк ст. Круглое Поле)	
Изм.	Кол.уч	Лист	№док.	Подпись	Дата		
Разраб.		Бурайкин			09.26	Этап №5	Стадия: Р; Лист: 4.3; Листов:
Проверил		Сундеев			09.26		
Н. контр.		Грошев			09.26	План земляных масс М 1:500. Площадка водоподготовки	ГРАДО ПРОЕКТ

Взам. инв. №


Подп. и дата

Инв. № подл.

Формат А4х3

С

Площадка локальных очистных сооружений

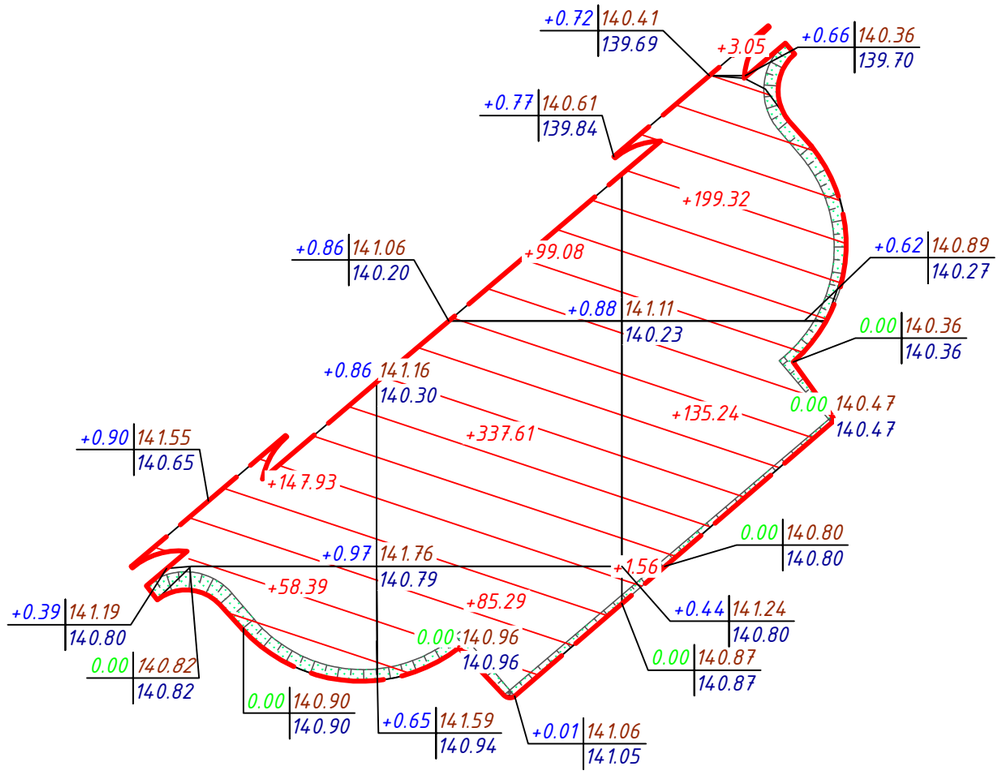

Ведомость объемов земляных масс

Наименование грунта	Количество, м³		Примечание
	Насыпь (+)	Выемка (–)	
1. Грунт планировки территории	1068	–	
2. Вытесненный грунт, в т.ч. при устройстве:		408	
а) проезда		252	
г) газона и откоса		156	
3. Поправка на уплотнение, k=0,1	107	–	
4. Всего пригодного грунта	1175	408	
5. Недостаток пригодного грунта		767	
7. Плодородный грунт, всего:			
а) используемый для озеленения территории	156	–	
б) недостаток плодородного грунта		156	
8. Итого перерабатываемого грунта	1331	1331	

Итого, м³					Всего, м³	
	Насыпь	+206.32	+521.98	+339.17		+1067.47
	Выемка	–	–	–		–

Площадь картограммы – 1453.29 м², в т.ч.:
насыпь – 1453.29 м², выемка – 0.00 м²

1. Система высот Балтийская 1977 г.
2. Система координат местная.
3. Картограмма разработана в программном комплексе Civil3d.
4. При расчете картограммы квадраты сетки приняты стороной равной 20 м.
5. Необходимость замены грунта под зданиями и сооружениями определена в марке КР.
6. Коэффициент уплотнения – не менее 0,95. Толщина каждого слоя 0,3–0,6 м (уточняется по результатам опытного уплотнения).
7. После возведения земляного полотна откосы необходимо доуплотнять планировщиками-уплотнителями.

Условные обозначения

рабочая отметка +0.88 / 140.23 черная отметка — красная отметка 141.11

+99.08 Насыпь

Изм.	Кол.уч	Лист	N°док.	Подпись	Дата
Разраб.		Бурайкин			09.26
Проверил		Сундеев			09.26
Н. контр.		Грошев			09.26

1439/2025/5-ГП-4.4

Инфраструктура индустриального парка «Этилен-600», Железнодорожная инфраструктура. Этап №5. Строительство железнодорожных путей необщего пользования (приемоотправочный парк ст. Круглое Поле)

Стадия	Лист	Листов
Р	4.4	

Этап №5


План земляных масс М 1:500.
Площадка локальных очистных сооружений

ГРАДО ПРОЕКТ

Взам. инв. N°
Подп. и дата
Инв. N° подл.

Формат А3

Площадка в районе четной горловины проектируемого Парка. Пути необщего пользования

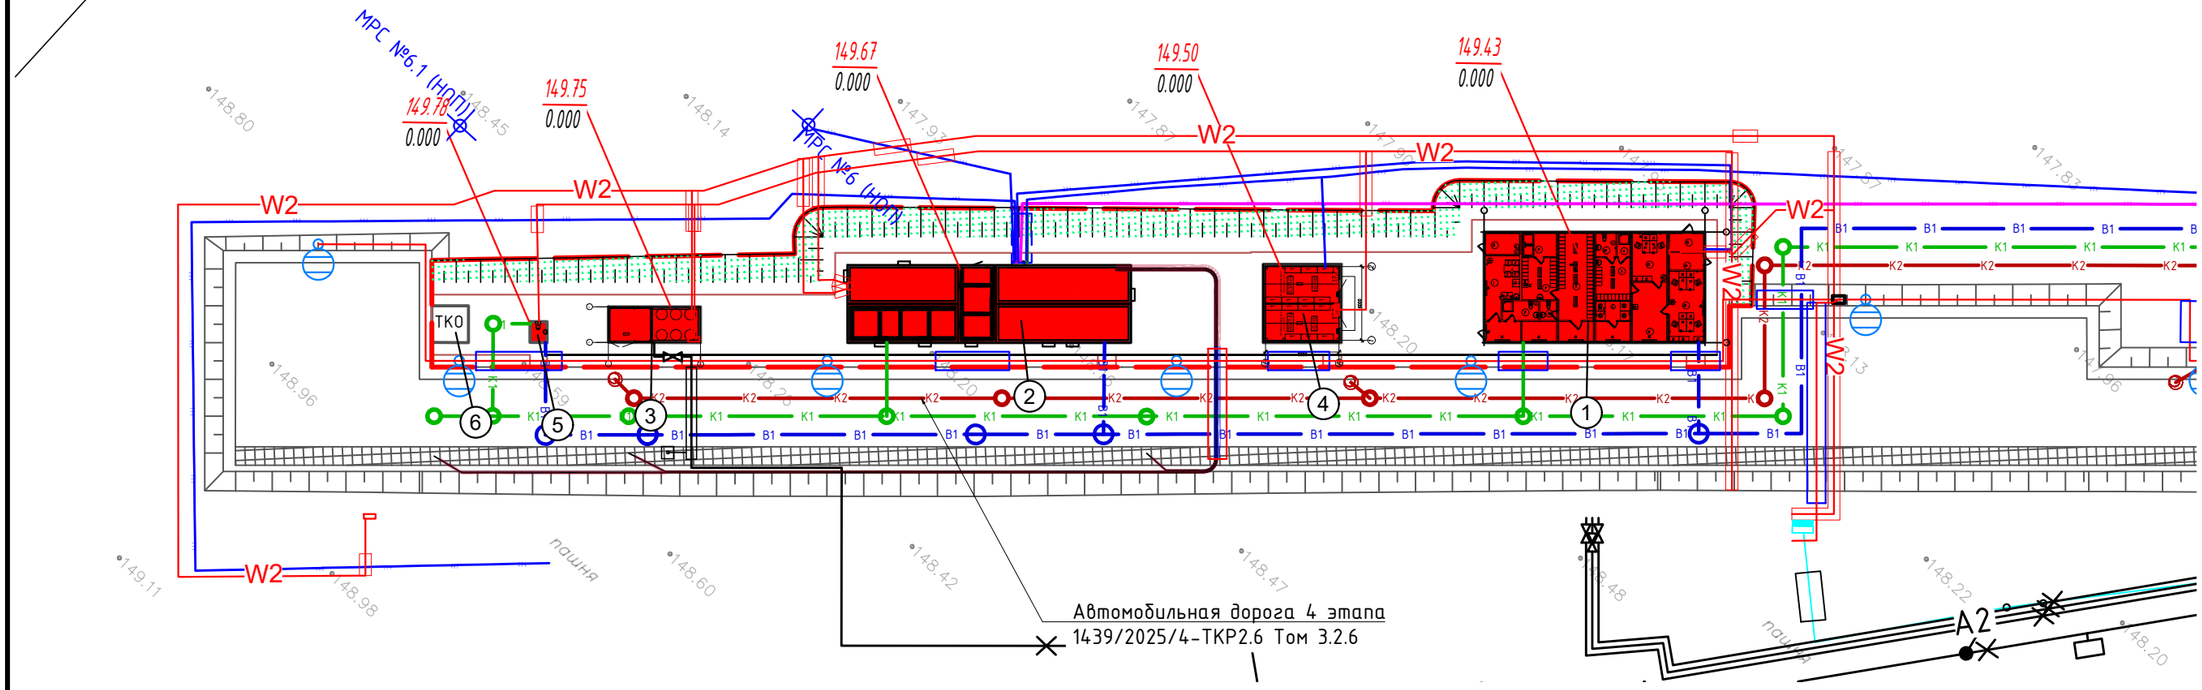

Экспликация зданий и сооружений

Номер на плане	Наименование	Примечание
1	Административно-бытовой модуль	Проектируемое
2	Мобильный комплекс железнодорожной Автоматики, телемеханики и связи (МК АТС)	Проектируемое
3	Модульная компрессорная	Проектируемое
4	Кладовая для хранения путевого инструмента и материалов ВСП	Проектируемое
5	Туалетный модуль 1.4х1.7	Проектируемое
6	ТКО	Проектируемое

Условные обозначения

	Граница проектирования благоустройства
	Проектируемое здание
	Проектируемые сети связи
	Проектируемая сеть воздуховода
WK	Проектируемая кабельная линия электропередач
	Проектируемый водопровод
	Проектируемая бытовая канализация
	Проектируемая ливневая канализация
W1	Кабельная линия 6 кВ в траншее
W2	Кабельная линия 0,4 кВ в траншее


1. Система высот Балтийская 1977 г.
2. Система координат местная.

Изм.	Кол.уч	Лист	N°док.	Подпись	Дата	1439/2025/5-ГП-5.1			
						Инфраструктура индустриального парка «Этилен-600», Железнодорожная инфраструктура. Этап №5. Строительство железнодорожных путей необщего пользования (приемоотправочный парк ст. Круглое Поле)			
Разраб.		Бурайкин			09.26	Этап №5	Стадия	Лист	Листов
Проверил		Сундеев			09.26		Р	5.1	
Н. контр.		Грошев			09.26	Сводный план сетей инженерно-технического обеспечения М 1:500. Площадка в районе четной горловины проектируемого Парка. Пути необщего пользования	ГРАДО ПРОЕКТ		

Взам. инв. N° | Подп. и дата | Инв. N° подл.

Формат А3

Площадка в районе нечетной горловины проектируемого Парка. Пути необщего пользования

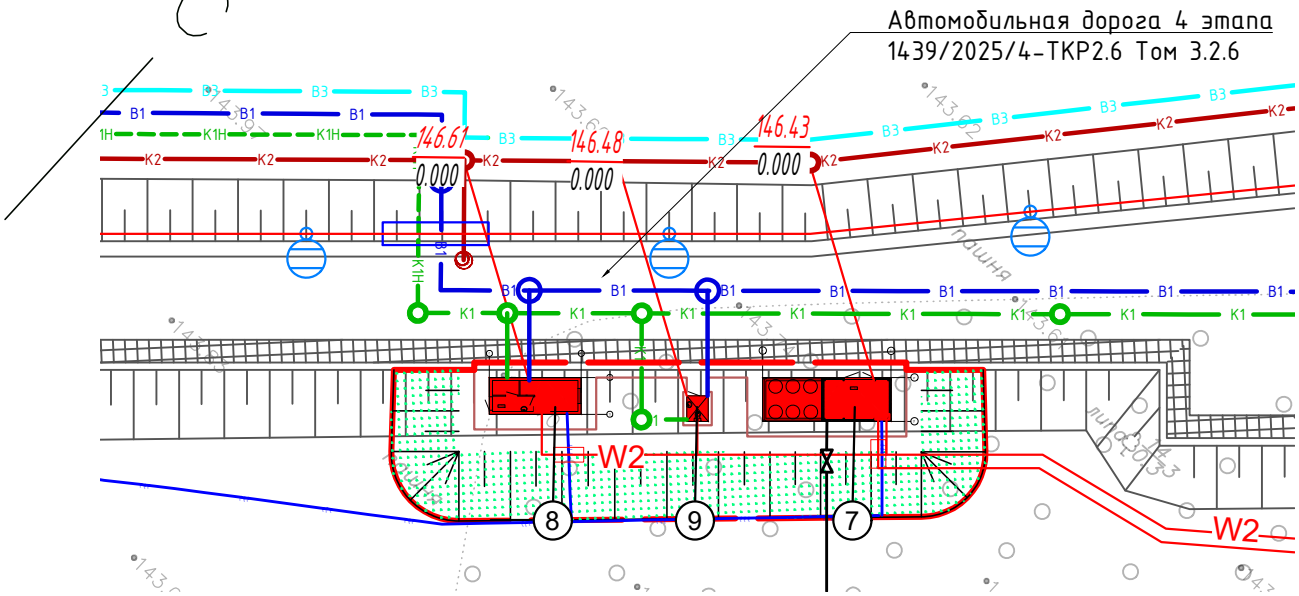

1. Система высот Балтийская 1977 г.
2. Система координат местная.

Экспликация зданий и сооружений

Номер на плане	Наименование	Примечание
7	Модульная компрессорная	Проектируемое
8	Модульный пункт обогрева	Проектируемое
9	Туалетный модуль 1.4х1.7	Проектируемое

Условные обозначения

	Граница проектирования благоустройства
	Проектируемое здание
	Проектируемые сети связи
	Проектируемая сеть воздуховода
	Проектируемый водопровод
	Проектируемая бытовая канализация
W1	Кабельная линия 6 кВ в траншее
W2	Кабельная линия 0,4 кВ в траншее

Взам. инв. N°

Подп. и дата

Инв. N° подл.

Изм.	Кол.уч	Лист	N°док.	Подпись	Дата
Разраб.		Бурайкин			09.26
Проверил		Сундеев			09.26
Н. контр.		Грошев			09.26

1439/2025/5-ГП-5.2

Инфраструктура индустриального парка «Этилен-600», Железнодорожная инфраструктура. Этап №5. Строительство железнодорожных путей необщего пользования (приемоотправочный парк ст. Круглое Поле)

Этап №5


Стадия	Лист	Листов
Р	5.2	

Сводный план сетей инженерно-технического обеспечения М 1:500. Площадка в районе нечетной горловины проектируемого Парка. Пути необщего пользования

ГРАДО ПРОЕКТ

Формат А4

Площадка Водоподготовки

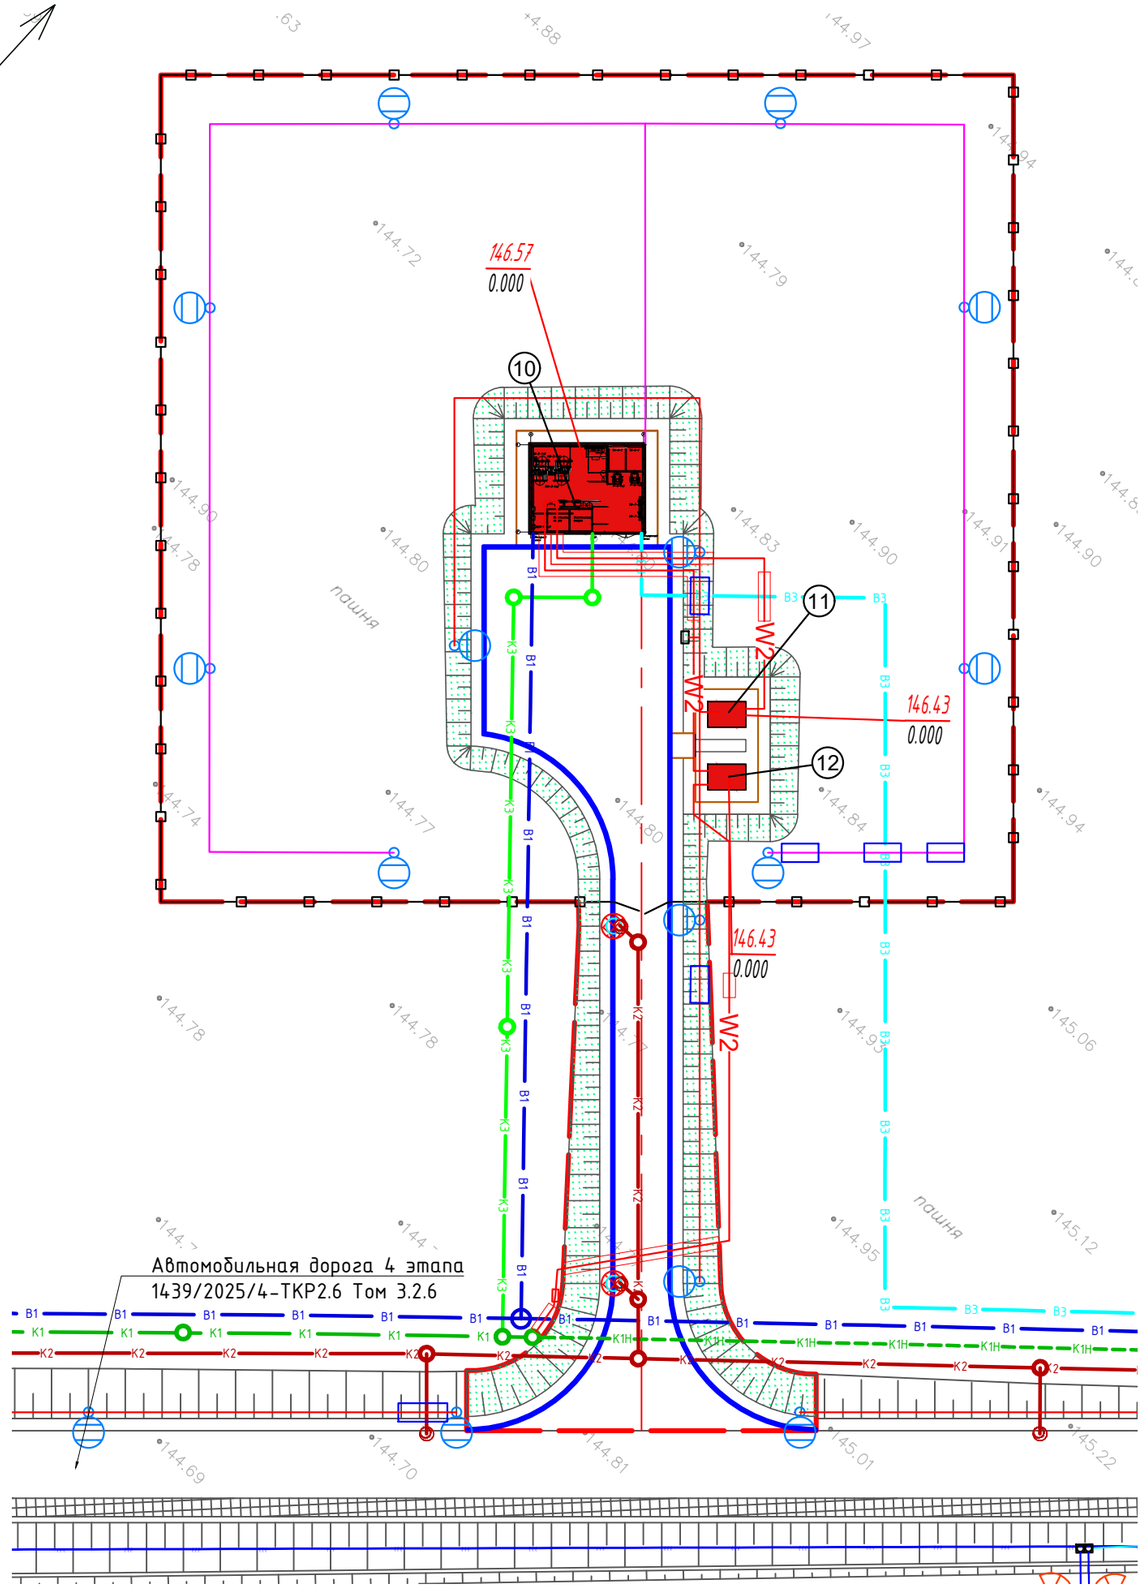

Экспликация зданий и сооружений

Номер на плане	Наименование	Примечание
10	Водоподготовка	Проектируемое
11, 12	Трансформаторная подстанция	Проектируемое

Условные обозначения

	Граница проектирования благоустройства
	Проектируемое здание
	Проектируемые сети связи
	Проектируемая сеть воздуховода
	Проектируемая кабельная линия электропередач
	Проектируемый водопровод
	Проектируемая бытовая канализация
	Проектируемая ливневая канализация
W1	Кабельная линия 6 кВ в траншее
W2	Кабельная линия 0,4 кВ в траншее
	Мачта освещения
	Дождеприемный колодец
	Ограждение l=269,30 м
	Ворота распашные 4,5 м

1. Система высот Балтийская 1977 г.
2. Система координат местная.

Изм.	Кол.уч	Лист	N°док.	Подпись	Дата
Разраб.		Бурайкин			09.26
Проверил		Сундеев			09.26
Н. контр.		Грошев			09.26

1439/2025/5-ГП-5.3

Инфраструктура индустриального парка «Этилен-600», Железнодорожная инфраструктура. Этап №5. Строительство железнодорожных путей необщего пользования (приемоотправочный парк ст. Круглое Поле)

Стадия	Лист	Листов
Р	5.3	

Этап №5

Сводный план сетей инженерно-технического обеспечения М 1:500. Площадка водоподготовки

ГРАДО ПРОЕКТ


Взам. инв. N°

Подп. и дата

Инв. N° подл.

Формат А3

Площадка локальных очистных сооружений

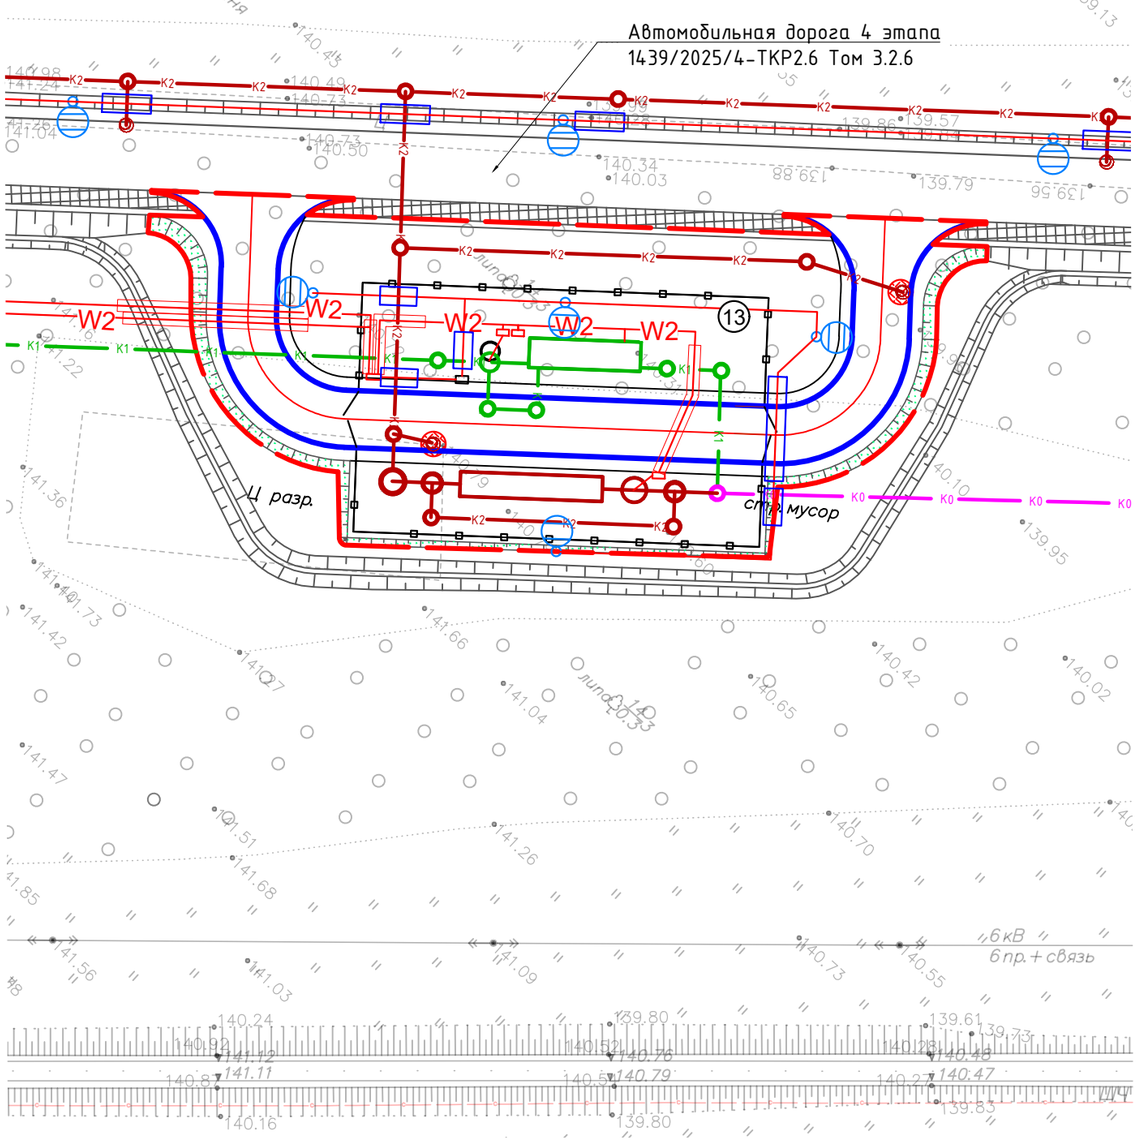

Экспликация зданий и сооружений

Номер на плане	Наименование	Примечание
13	Локальные очистные сооружения (ЛОС)	Проектируемое

Условные обозначения

	Граница проектирования благоустройства
	Проектируемое здание
	Проектируемые сети связи
	Проектируемая сеть воздуховода
	Проектируемая бытовая канализация
	Проектируемая ливневая канализация
W2	Кабельная линия 0,4 кВ в траншее
	Мачта освещения
	Дождеприемный колодец
	Ограждение l=97,90 м
	Ворота распашные 4,5 м

1. Система высот Балтийская 1977 г.
2. Система координат местная.

Изм.	Кол.уч	Лист	N°док.	Подпись	Дата
Разраб.		Бурайкин			09.26
Проверил		Сундеев			09.26
Н. контр.		Грошев			09.26

1439/2025/5-ГП-5.4

Инфраструктура индустриального парка «Этилен-600», Железнодорожная инфраструктура. Этап №5. Строительство железнодорожных путей необщего пользования (приемоотправочный парк ст. Круглое Поле)

Этап №5

Стадия	Лист	Листов
Р	5.4	

Сводный план сетей инженерно-технического обеспечения М 1:500. Площадка локальных очистных сооружений

ГРАДО ПРОЕКТ


Формат А3

Взам. инв. N°


Подп. и дата

Инв. N° подл.


Площадка в районе четной горловины проектируемого Парка. Пути необщего пользования

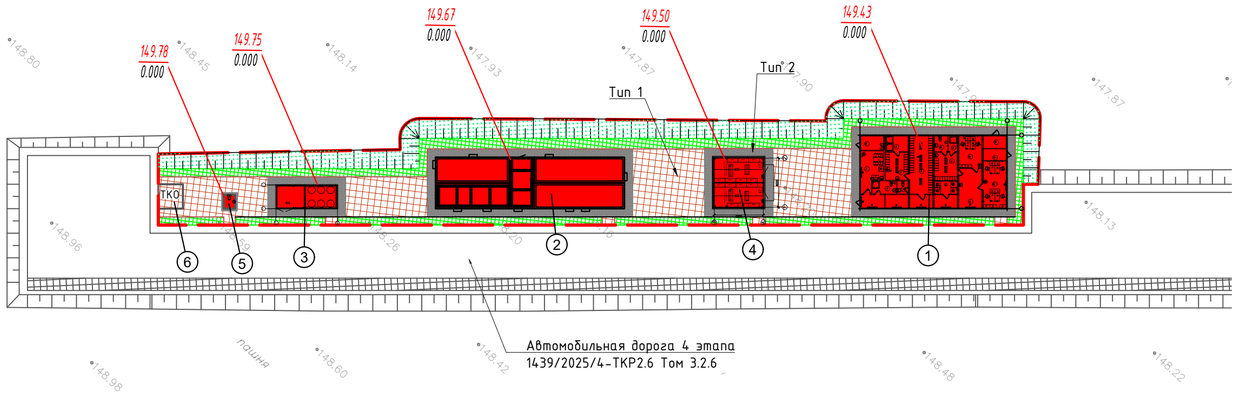

Установка бортового камня БР100.20.8 в сопряжении тротуара и газона

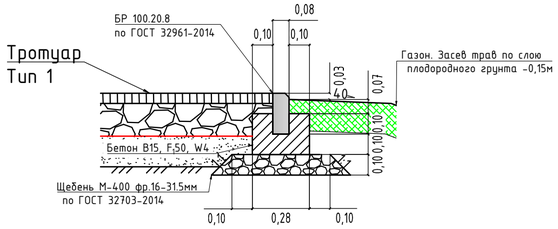

Установка бортового камня БР100.20.8 в сопряжении отмостки и газона

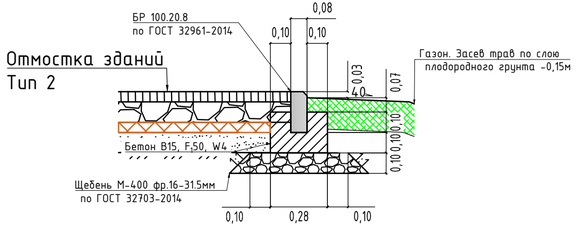

Ведомость тротуаров, дорожек и площадок

Поз.	Наименование	Тип	Площадь покрытия, м²	Примечание
1	Тротуар (асфальтобетон)	1	271,55	
2	Отмостка (асфальтобетон)	2	176,88	

Ведомость элементов озеленения

Поз.	Наименование породы или вида насаждения	Возраст, лет	Площадь покрытия, м²	Примечание
1	Газон посевной		235,65	м²
2	Укрепление откосов посевом трав		257,66	м²

Ведомость бортовых камней

Поз.	Наименование	Тип	пог.м	Примечание
1	БР 100.20.18 ГОСТ 32961-2014	2	231,55	


Экспликация зданий и сооружений

Номер на плане	Наименование	Примечание
1	Административно-бытовой модуль	Проектируемое
2	Мобильный комплекс железнодорожной Автоматики, телемеханики и связи (МК АТС)	Проектируемое
3	Модульная компрессорная	Проектируемое
4	Кладовая для хранения путевого инструмента и материалов ВСП	Проектируемое
5	Туалетный модуль 1.4х1.7	Проектируемое
6	ТКО	Проектируемое

Условные обозначения

	Граница проектирования благоустройства
	Проектируемое здание
	Тротуар из асфальтобетона
	Отмостка
	Газон
	Откос
	Бортовой камень БР100.20.8
	Бровка земляного полотна

Укрепление откосов

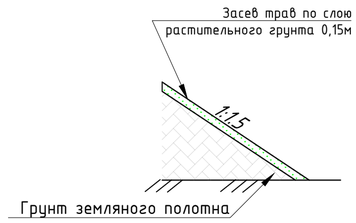

1. Система высот Балтийская 1977 г.
2. Система координат местная.
3. Размеры даны в метрах

Изм.	Кол.уч	Лист	№док.	Подпись	Дата	1439/2025/5-ГП-6.1			
						Инфраструктура индустриального парка «Этилен-600», Железнодорожная инфраструктура. Этап №5. Строительство железнодорожных путей необщего пользования (приемоотправочный парк ст. Круглое Поле)			
Разраб.		Бурайкин			09.26	Этап №5	Стадия	Лист	Листов
Проверил		Сундеев			09.26		Р	6.1	
Н. контр.		Грошев			09.26	План благоустройства М 1:500. Площадка в районе четной горловины проектируемого Парка. Пути необщего пользования	ГРАДО ПРОЕКТ		


Взам. инв. №

Подп. и дата

Инв. № подл.

Формат А4х3

Площадка в районе нечетной горловины проектируемого Парка. Пути необщего пользования

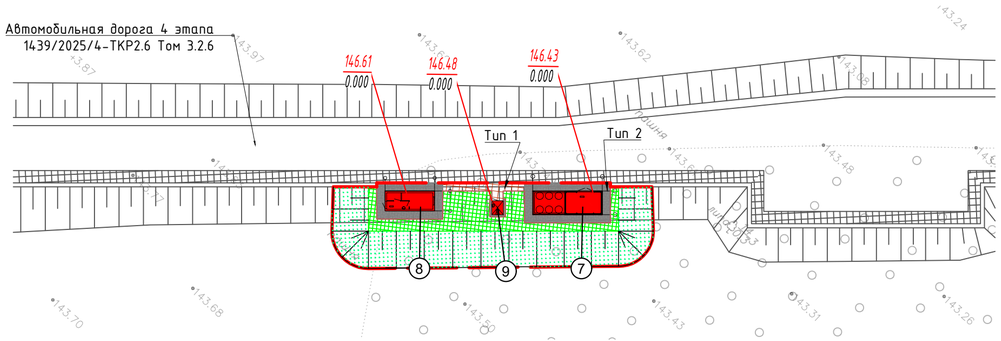


Экспликация зданий и сооружений

Номер на плане	Наименование	Примечание
7	Модульная компрессорная	Проектируемое
8	Модульный пункт обогрева	Проектируемое
9	Туалетный модуль 1.4х1.7	Проектируемое


Условные обозначения

	Граница проектирования благоустройства
	Проектируемое здание
	Тротуар из асфальтобетона
	Отмостка
	Газон
	Откос
	Бортовой камень БР100.20.8
	Бровка земляного полотна

Установка бортового камня БР100.20.8 в сопряжении тротуара и газона

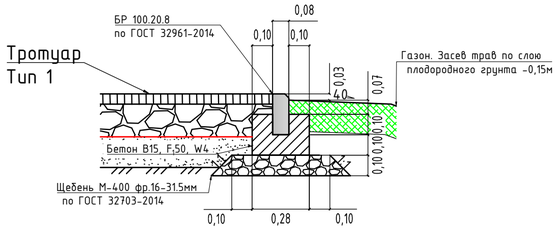

Установка бортового камня БР100.20.8 в сопряжении отмостки и газона

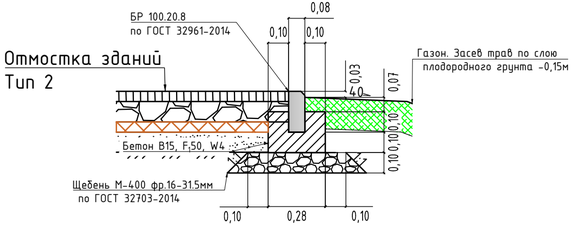

Ведомость тротуаров, дорожек и площадок

Поз.	Наименование	Тип	Площадь покрытия, м²	Примечание
1	Тротуар (асфальтобетон)	1	11,66	
2	Отмостка (асфальтобетон)	2	49,25	


Ведомость элементов озеленения

Поз.	Наименование породы или вида насаждения	Возраст, лет	Площадь покрытия, м²	Примечание
1	Газон посевной		256,80	м²
2	Укрепление откосов посевом трав		212,56	м²

Ведомость бортовых камней

Поз.	Наименование	Тип	пог.м	Примечание
1	БР 100.20.18 ГОСТ 32961-2014	2	52,55	

Укрепление откосов

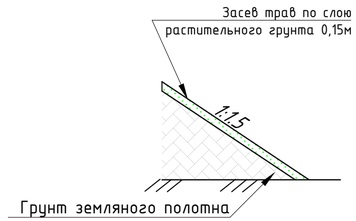

1. Система высот Балтийская 1977 г.
2. Система координат местная.
3. Размеры даны в метрах

Изм.	Колуч	Лист	№док.	Подпись	Дата	1439/2025/5-ГП-6.2			
						Инфраструктура индустриального парка «Этилен-600», Железнодорожная инфраструктура. Этап №5. Строительство железнодорожных путей необщего пользования (приемоотправочный парк ст. Круглое Поле)			
Разраб.		Бурайкин			09.26	Этап №5	Стадия	Лист	Листов
Проверил		Сундеев			09.26		Р	6.2	
Н. контр.		Грошев			09.26	План благоустройства М 1:500. Площадка в районе нечетной горловины проектируемого Парка. Пути необщего пользования	ГРАДО ПРОЕКТ		


Взам. инв. №

Подп. и дата


Инв. № подл.

Формат А4х3


Площадка Водоподготовки

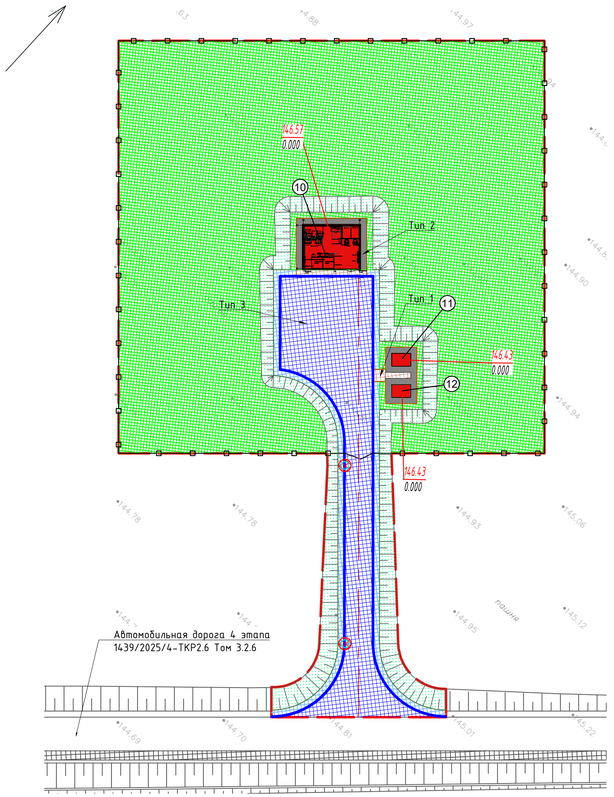

Установка бортового камня БР100.20.8 в сопряжении тротуара и газона

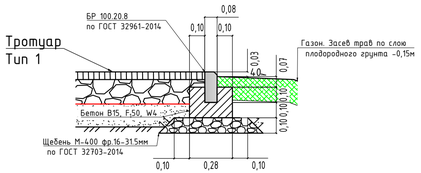

Установка бортового камня БР100.20.8 в сопряжении отмостки и газона

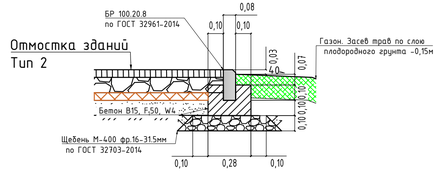

Ведомость тротуаров, дорожек и площадок

Поз.	Наименование	Тип	Площадь покрытия, м²	Примечание
1	Тротуар (асфальтобетон)	1	19,60	
2	Отмостка (дорожки)	2	56,10	
3	Асфальтобетонный проезд	3	574,20	


Ведомость элементов озеленения

Поз.	Наименование породы или вида насаждения	Возраст, лет	Площадь покрытия, м²	Примечание
1	Газон посевной		3858,15	м²
2	Укрепление откосов посевом трав		514,70	м²
3	Насыпная обочина		165,35	м²

Ведомость бортовых камней

Поз.	Наименование	Тип	пог.м	Примечание
1	БР 100.30.15 ГОСТ 32961-2014	1	178,10	
2	БР 100.20.18 ГОСТ 32961-2014	2	60,90	

Укрепление откосов

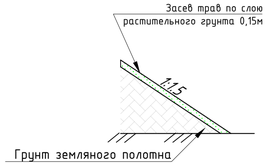

Экспликация зданий и сооружений

Номер на плане	Наименование	Примечание
10	Водоподготовка	Проектируемое
11, 12	Трансформаторная подстанция	Проектируемое

Условные обозначения

	Граница проектирования благоустройства
	Проектируемое здание
	Асфальтобетонный проезд
	Тротуар из асфальтобетонна
	Отмостка из асфальтобетонна
	Обочина
	Газон
	Откос
	Бортовой камень БР100.30.15
	Бортовой камень БР100.20.8
	Бровка земляного полотна
	Ось проезда
	Дождеприемный колодец
	Ограждение l=269,30 м
	Ворота распашные 4,5 м


1. Система высот Балтийская 1977 г.
2. Система координат местная.
3. Размеры даны в метрах

Изм.	Колич.	Лист	№док.	Подпись	Дата	1439/2025/5-ГП-6.3			
						Инфраструктура индустриального парка «Этилен-600», Железнодорожная инфраструктура. Этап №5. Строительство железнодорожных путей необщего пользования (приемоотправочный парк ст. Круглое Поле)			
Разраб.		Бурайкин			09.26	Этап №5	Стадия	Лист	Листов
Проверил		Сундеев			09.26		Р	6.3	
Н. контр.		Грошев			09.26	План благоустройства М 1:500. Площадка водоподготовки	ГРАДО ПРОЕКТ		

Взам. инв. №
Подп. и дата
Инв. № подл.

Формат А4х4

Площадка локальных очистных сооружений

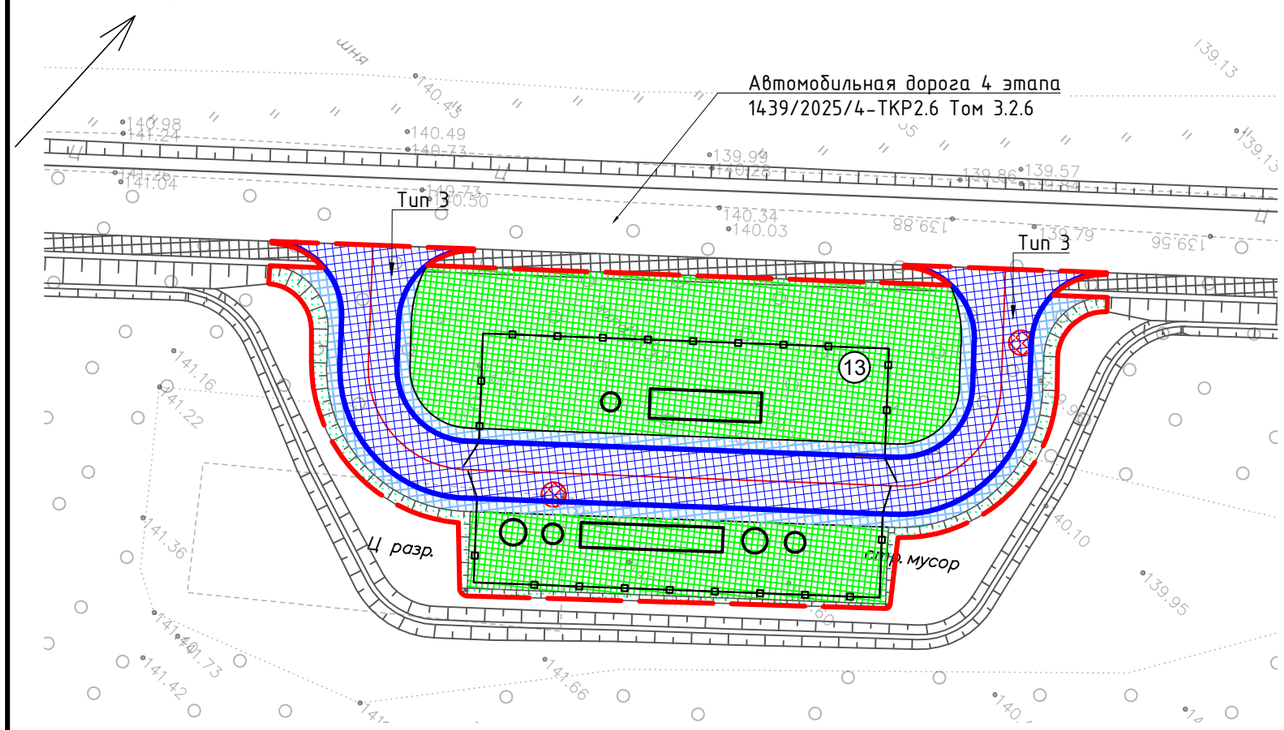

Ведомость тротуаров, дорожек и площадок

Поз.	Наименование	Тип	Площадь покрытия, м²	Примечание
1	Асфальтобетонный проезд	3	393,35	

Ведомость элементов озеленения

Поз.	Наименование породы или вида насаждения	Воз-раст, лет	Площадь покрытия, м²	Примечание
1	Газон посевной		785,20	м²
2	Укрепление откосов посевом трав		88,40	м²
3	Насыпная обочина		157,83	м²

Ведомость бортовых камней

Поз.	Наименование	Тип	пог.м	Примечание
1	БР 100.30.15 ГОСТ 32961-2014	1	174,80	


Экспликация зданий и сооружений

Номер на плане	Наименование	Примечание
13	Локальные очистные сооружения (ЛОС)	Проектируемое

Условные обозначения

	Граница проектирования благоустройства
	Проектируемые сооружения
	Асфальтобетонный проезд
	Обочина
	Газон
	Откос
	Бортовой камень БР100.30.15
	Бровка земляного полотна
	Ось проезда
	Ограждение l=97,90 м
	Ворота распашные 4,5 м

Укрепление откосов

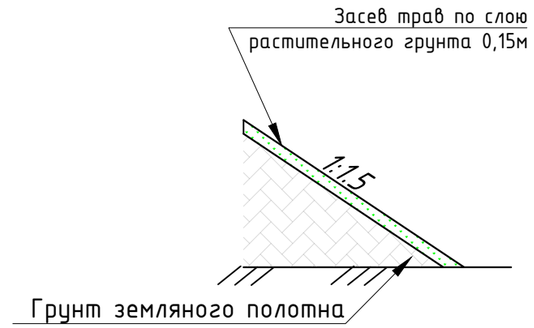

1. Система высот Балтийская 1977 г.
2. Система координат местная.
3. Размеры даны в метрах

Изм.	Кол.уч	Лист	N°док.	Подпись	Дата
Разраб.		Бурайкин			09.26
Проверил		Сундеев			09.26
Н. контр.		Грошев			09.26

1439/2025/5-ГП-6.4

Инфраструктура индустриального парка «Этилен-600», Железнодорожная инфраструктура. Этап №5. Строительство железнодорожных путей необщего пользования (приемоотправочный парк ст. Круглое Поле)

Стадия	Лист	Листов
Р	6.4	

Этап №5

План благоустройства М 1:500. Площадка локальных очистных сооружений

ГРАДО ПРОЕКТ

Взам. инв. N°

Подп. и дата

Инв. N° подл.

Формат А3