ОБЩЕСТВО С ОГРАНИЧЕННОЙ ОТВЕТСТВЕННОСТЬЮ

alabuga DEVELOPMENT

№ СРО-П-114-14012010

Заказчик – АО «ОЭЗ ППТ «Алабуга»

Инфраструктура индустриального парка «Этилен-600», Железнодорожная инфраструктура.

Этап №5. Строительство железнодорожных путей необщего пользования (приемоотправочный парк ст. Круглое Поле)

ПРОЕКТНАЯ ДОКУМЕНТАЦИЯ

РАЗДЕЛ 4. Здания и сооружения, входящие в инфраструктуру линейного объекта. Здания обслуживания железнодорожной инфраструктуры необщего пользования Дополнительного парка

Часть 1. Схема планировочной организации земельного участка

1439/2025/5-ИЛО1

Том 4.1

2026 г.

ОБЩЕСТВО С ОГРАНИЧЕННОЙ ОТВЕТСТВЕННОСТЬЮ

alabuga
DEVELOPMENT

№ СРО-П-114-14012010

Заказчик – АО «ОЭЗ ППТ «Алабуга»

Инфраструктура индустриального парка «Этилен-600», Железнодорожная инфраструктура.

Этап №5. Строительство железнодорожных путей необщего пользования (приемоотправочный парк ст. Круглое Поле)

ПРОЕКТНАЯ ДОКУМЕНТАЦИЯ

РАЗДЕЛ 4. Здания и сооружения, входящие в инфраструктуру линейного объекта. Здания обслуживания железнодорожной инфраструктуры необщего пользования Дополнительного парка

Часть 1. Схема планировочной организации земельного участка

1439/2025/5-ИЛО1

Том 4.1

Главный инженер проекта Мезенцев Д.В.

2026 г.

Общество с ограниченной ответственностью
«ГрадоПроект»

Инфраструктура индустриального парка «Этилен-600», Железнодорожная инфраструктура.

Этап №5. Строительство железнодорожных путей необщего пользования (приемоотправочный парк ст. Круглое Поле)

ПРОЕКТНАЯ ДОКУМЕНТАЦИЯ

РАЗДЕЛ 4. Здания и сооружения, входящие в инфраструктуру линейного объекта. Здания обслуживания железнодорожной инфраструктуры необщего пользования Дополнительного парка

Часть 1. Схема планировочной организации земельного участка

1439/2025/5-ИЛО1

Том 4.1

Директор **И. А. Трубицин**

Главный инженер проекта **В. В. Сундеев**

2026 г.

Обозначение	Наименование	Примечание
1439/2025/5-ИЛО1-С	Содержание тома	3
	Текстовая часть	
1439/2025/5-ИЛО1-ТЧ	Текстовая часть	4
	Графическая часть	
1439/2025/5-ИЛО1-ГЧ.01	Ведомость документов графической части	
1439/2025/5-ИЛО1-ГЧ.02	Ситуационный план	
1439/2025/5-ИЛО1-ГЧ.03	Схема планировочной организации земельного участка	
1439/2025/5-ИЛО1-ГЧ.04	Сводный план сетей инженерно-технического обеспечения	
1439/2025/5-ИЛО1-ГЧ.05	Схема организации рельефа и план земляных масс	

Состав проекта см. в томе 1439/2025/5-СП.

Взам. инв №

Подпись и дата

Инв. № подл.

Изм.	Колуч	Лист	№ док	Подпись	Дата	1439/2025/5-ИЛО1-С		
Разработал		Бурайкин			05.26	Содержание тома	Стадия	Лист	Листов
Проверил		Сундеев			05.26		П	1	1
Н. контр.		Грошев			05.26		ГРАДО ПРОЕКТ		

Содержание текстовой части

1 Основание, исходные данные и условия для разработки раздела 5
2 Характеристика земельных участков для размещения объектов капитального строительства, входящих в инфраструктуру линейного объекта..... 6
3 Сведения о наличии зон с особыми условиями использования территорий в пределах границ земельных участков объектов капитального строительства, входящих в инфраструктуру линейного объекта..... 9
4 Обоснование границ санитарно-защитных зон объектов капитального строительства в пределах границ земельных участков для их размещения 9
5 Обоснование и описание планировочной организации земельных участков для размещения зданий и сооружений в соответствии с документами об использовании земельного участка 10
6 Технико-экономические показатели земельных участков для размещения зданий и сооружений 11
7 Обоснование и описание решений по инженерной подготовке территории, в том числе решений по инженерной защите территории и объектов капитального строительства от последствий опасных геологических процессов, паводковых, поверхностных и грунтовых вод 11
8 Описание организации рельефа вертикальной планировкой 12
9 Описание решений по благоустройству территории 12
10 Обоснование зонирования территории земельных участков для размещения зданий строений и сооружений, а также принципиальная схема размещения территориальных зон с указанием сведений о расстояниях до ближайших установленных территориальных зон и мест размещения существующих и проектируемых зданий, строений и сооружений (основного, вспомогательного, подсобного, складского и обслуживающего назначения) объектов капитального строительства, входящих в инфраструктуру линейного объекта 13
11 Обоснование схем транспортных коммуникаций, обеспечивающих внешние и внутренние (в том числе межцеховые) грузоперевозки..... 13
12 Характеристика и технические показатели транспортных коммуникаций объектов капитального строительства, входящих в инфраструктуру линейного объекта 14
13 Обоснование схем транспортных коммуникаций, обеспечивающих внешний и внутренний подъезд к объектам капитального строительства, входящих в инфраструктуру линейного объекта..... 14
14 Использованные документы и материалы..... 14
15 Постановление об утверждении проекта планировки территории и проекта межевания территории 15
Таблица регистрации изменений..... 17

Взам. инв №

Подпись и дата

Инв. № подл.

						1439/2025/5-ИЛО1-ТЧ
Изм.	Колуч	Лист	№ док	Подпись	Дата	
Разработал		Бурайкин			05.26	Текстовая часть
Проверил		Сундеев			05.26	
Н. контр.		Грошев			05.26	

Стадия	Лист	Листов
П	1	14

ГРАДО ПРОЕКТ

1 Основание, исходные данные и условия для разработки раздела

Основанием и исходными данными для разработки настоящего раздела служат:

- договор № 1439/2025/4 от 10.10.2025 г между Заказчиком ООО «Алабуга Девелопмент», и Подрядчиком ООО «ГрадоПроект» (свидетельство о членстве в саморегулируемой организации в области архитектурно-строительного проектирования "Саморегулируемая организация СОЮЗ «Гильдия архитекторов и проектировщиков Поволжья»", регистрационный номер П-108-002130020178-0080 от 23.11.2022 г.).
- отчетная документация по результатам инженерных изысканий: инженерно – геологических, инженерно – геодезических, инженерно – экологических и инженерно – гидрометеорологических, выполненных ООО "Геодезия Кадастр Изыскания" в ноябре 2025 года;
- Постановления об утверждении Проекта планировки территории и Проекта межевания территории;

Состав и содержание раздела соответствует требованиям «Положения о составе разделов проектной документации и требованиях к их содержанию» (в действующей редакции), утвержденного постановлением Правительства Российской Федерации от 16.02.2008 года № 87.

Состав проекта представлен отдельным документом.

2 Характеристика земельных участков для размещения объектов капитального строительства, входящих в инфраструктуру линейного объекта

Земельный участок определен на основании "Проекта планировки территории" и "Проекта межевания территории".

В процессе сбора исходных данных были получены правоустанавливающие документы и сведения государственного кадастра недвижимости на земельные участки, на которых располагается объект проектирования.

Указанные материалы позволили произвести анализ существующей полосы отвода железной дороги на предмет соответствия требованиям № 221-ФЗ «О государственном кадастре недвижимости».

Территория строительства расположена в границах, определенных проектом межевания и планировки территории на землях с разрешенным использованием – строительство, реконструкция, эксплуатация линейных объектов и землях категории - земли промышленности, энергетики, транспорта, связи, радиовещания, телевидения, информатики, земли для обеспечения космической деятельности, земли обороны, безопасности и земли иного специального назначения.

Перечень и характеристики земельных участков представлены в таблице 2.1.

Таблица 2.1 - Перечень и характеристики земельных участков

Контур	Участок	Категория земель	Разрешенное использование	Площадь, м2
1	16:39:000000:487	Земли промышленности*	-	15688.47
2	16:39:161101:9	Земли сельскохозяйственного назначения	-	12484.79
3	16:39:000000:487	Земли промышленности*	-	8296.42
4	16:39:160801:1	Земли населенных пунктов	По документу: малоэтажная многоквартирная жилая застройка (код по классификатору видов разрешенного использования земельных участков-2.1.1),	675.94
5	16:39:160901:96	Земли сельскохозяйственного назначения	Для сельскохозяйственного производства	4627.25
6	16:39:160801:1	Земли населенных пунктов	По документу: малоэтажная многоквартирная жилая застройка (код по классификатору видов разрешенного использования земельных участков-2.1.1),	936.75
8	16:39:000000:487	Земли промышленности*	-	59966.9
9	16:39:000000:5730	Земли промышленности*	для размещения объектов аэропорта "Бегишево" (код разрешенного использования: 7.4)	411.32

Контур	Участок	Категория земель	Разрешенное использование	Площадь, м2
10	16:39:160902:2	Земли сельскохозяйственного назначения	-	1449.94
11	16:39:160902:6	Земли сельскохозяйственного назначения	-	14404.56
12	16:39:160902:2	Земли сельскохозяйственного назначения	-	3979.98
13	16:39:011903:20	Земли сельскохозяйственного назначения	-	9206.18
14	16:39:011903:60	Земли сельскохозяйственного назначения	Для сельскохозяйственного производства	1627.85
15	16:39:011903:61	Земли сельскохозяйственного назначения	для сельскохозяйственного производства	188.44
16	Неразграниченная территория	-	-	48.27
17	16:39:011903:20	Земли сельскохозяйственного назначения	-	306.15
18	16:39:012003:1	Земли промышленности*	-	1282.97
19	16:39:011903:20	Земли сельскохозяйственного назначения	-	274.76
20	16:39:011902:10	Земли сельскохозяйственного назначения	-	47.21
21	16:39:011902:31	Земли сельскохозяйственного назначения	для сельскохозяйственного производства	4150
22	16:39:011902:53	Земли сельскохозяйственного назначения	для сельскохозяйственного производства	688.28
23	16:39:011902:47	Земли промышленности*	в целях добычи полезных ископаемых	76.35
24	16:39:011902:10	Земли сельскохозяйственного назначения	-	1224.06
25	16:39:011902:53	Земли сельскохозяйственного назначения	для сельскохозяйственного производства	6304.59
26	16:39:011902:13	Земли сельскохозяйственного назначения	для сельскохозяйственного производства	37180.36
27	16:39:012001:10	Земли сельскохозяйственного назначения	-	783.57

Контур	Участок	Категория земель	Разрешенное использование	Площадь, м2
28	16:39:000000:6728	Земли сельскохозяйственного назначения	для сельскохозяйственного производства	3175.46
29	16:39:011902:67	Земли сельскохозяйственного назначения	для сельскохозяйственного производства	11367.69
30	16:39:000000:487	Земли промышленности*		109629.3
31	Неразграниченная территория	-	-	5.21
32	Неразграниченная территория	-	-	501.93
33	16:39:012001:8	Земли сельскохозяйственного назначения	-	15797.28
35	Неразграниченная территория	-	-	142.99
36	16:39:012001:8	Земли сельскохозяйственного назначения		11430.43
37	16:39:000000:469	Земли населенных пунктов		7133.22
38	16:39:011902:9	Земли сельскохозяйственного назначения		9594.1
39	Неразграниченная территория	-	-	997.31
40	16:39:160702:4132	Земли населенных пунктов	земельные участки (территории) общего пользования (код вида разрешенного использования 12.0)	614.48
41	16:39:160702:4132	Земли населенных пунктов	земельные участки (территории) общего пользования (код вида разрешенного использования 12.0)	3654.79
42	Неразграниченная территория	-	-	6039.62
Итого				**366395**

*****Земли промышленности, энергетики, транспорта, связи, радиовещания, телевидения, информатики, земли для обеспечения космической деятельности, земли обороны, безопасности и земли иного специального назначения

Зона планируемого размещения, проектируемого объекта представляет собой территорию, необходимую для выполнения всего комплекса подготовительных, земляных и строительно-монтажных работ, ограниченную условными линиями, по которым на местности устраивается ограждение строительной площадки.

Размеры граница зоны планируемого размещения объекта, приняты, согласно проекту планировки территории.

Сопоставление проектных планировочных решений и границ земельного участка, определенного "Проектом планировки территории", для размещения вновь проектируемых объектов не выявило необходимости в дополнительном приобретении земель.

3 Сведения о наличии зон с особыми условиями использования территорий в пределах границ земельных участков объектов капитального строительства, входящих в инфраструктуру линейного объекта

Зоны с особыми условиями использования территорий в границах земельного участка, предназначенного для размещения объекта представлены в таблице 3.1.

Таблица 3.1

№	Кадастровый номер	Тип зоны (территории)
1	16:00-6.1607	Водоохранная зона
2	16:00-6.250	Прибрежная защитная полоса
3	16:39-6.1621	Охранная зона инженерных коммуникаций
4	16:39-6.129	Охранная зона инженерных коммуникаций
5	16:39-6.585	Охранная зона инженерных коммуникаций
6	01.06.4185 16:00	Охранная зона инженерных коммуникаций
7	01.06.2601 16:39	Охранная зона транспорта
8	16:39-6.934	Охранная зона инженерных коммуникаций
9	01.06.4298 16:00	Иная зона с особыми условиями использования территории
10	16:39-6.849	Охранная зона инженерных коммуникаций
11	01.06.4307 16:00	Иная зона с особыми условиями использования территории
12	16:39-6.1524	Охранная зона инженерных коммуникаций
13	01.06.3780 16:00	Охранная зона инженерных коммуникаций
14	01.06.3804 16:00	Охранная зона инженерных коммуникаций
15	01.06.2602 16:39	Охранная зона транспорта
16	01.06.2795 16:00	Охранная зона инженерных коммуникаций
17	16:39-6.801	Охранная зона инженерных коммуникаций
18	16:39-6.1609	Охранная зона линий и сооружений связи и линий и сооружений радиофикации
19	01.06.4464 16:00	Охранная зона линий и сооружений связи и линий и сооружений радиофикации
20	16:39-6.1382	Охранная зона линий и сооружений связи и линий и сооружений радиофикации
21	01.06.4207 16:00	Охранная зона линий и сооружений связи и линий и сооружений радиофикации
22	01.06.4326 16:00	Иная зона с особыми условиями использования территории
23	01.06.2600 16:39	Охранная зона транспорта

4 Обоснование границ санитарно-защитных зон объектов капитального строительства в пределах границ земельных участков для их размещения

Проектируемый объект - "Инфраструктура индустриального парка "Этилен 600", Железнодорожная инфраструктура» находится на территории индустриального парка "Этилен 600", и относится к его объектам. Изменение санитарно-защитных зон данным проектом не предусмотрено

5 Обоснование и описание планировочной организации земельных участков для размещения зданий и сооружений в соответствии с документами об использовании земельного участка

Дополнительно испрашиваемых земельных участков настоящим проектом не предусмотрено.

Планировочная организация участка проектирования разработана в увязке с существующей застройкой, дорожной сетью, технологическими и транспортно-эксплуатационными условиями действующего промышленного предприятия. А также с учётом санитарных и противопожарных требований, технологической схемой работы проектируемого объекта.

Противопожарные мероприятия реализуются наличием разрывов между зданиями и сооружениями согласно степени огнестойкости и классу конструктивной пожарной опасности. Ко всем зданиям и сооружениям обеспечен подъезд пожарных автомобилей и другого специализированного транспорта, необходимого для обслуживания проектируемого объекта в период эксплуатации.

Размещение сооружений принято в увязке с технологической схемой работы предприятия. Размещение вновь проектируемых зданий и сооружений на генплане действующего предприятия выполняется в соответствии с требованиями действующих на момент разработки строительных норм и правил и иных нормативных документов. Расстояния от соседних зданий и сооружений приняты согласно СП 4.13130.2013 в соответствии со степенью огнестойкости и классом конструктивной пожарной опасности.

Для размещения сооружений необходимо выполнить демонтаж существующих инженерных сетей и сооружений, попадающий в «пятно» застройки.

Ко всем проектируемым зданиям и сооружениям предусмотрен подъезд пожарной техники. Ширина проезда составляет 4,5 м. Расстояния от проездов до наружных стен зданий и сооружений принято с учётом высоты зданий. Проезды выполнены с одной или двух сторон.

В основу построения схемы планировочной организации земельного участка проектируемой установки положены следующие основные принцип:

- обеспечение технологических связей отдельных секций и блоков;
- обеспечение нормативных транспортных связей по кратчайшим направлениям;
- наиболее оптимальное (в соответствии с технологической взаимосвязью производственных процессов) размещение зданий, сооружений, надземных и подземных инженерных сетей и коммуникаций;
- обеспечение удобства для проведения ремонтных работ.

6 Технико-экономические показатели земельных участков для размещения зданий и сооружений

Технико-экономические показатели земельного участка приведены в таблице 6.1.

Таблица 6.1. Технико-экономические показатели

Поз.	Наименование	Ед. изм.	Кол-во
1	Площадь участка в границах проектирования ,в том числе: -Площадка размещения зданий НОП №1 -Площадка размещения зданий НОП №2 -Площадка Водоподготовки -Площадка ЛОС	м2	8463.41 1318.91 392.01 5299.20 1453.29
2	Площадь проектируемых зданий, в том числе: -Площадка размещения зданий НОП №1 -Площадка размещения зданий НОП №2 -Площадка Водоподготовки -Площадка ЛОС	м2	541.43 371.25 41.81 83.33 45.04
3	Площадь проектируемого покрытия, в том числе: -Площадка размещения зданий НОП №1 -Площадка размещения зданий НОП №2 -Площадка Водоподготовки -Площадка ЛОС	м2	7921.98 947.66 350.20 5215.87 1408.25
4	Площадь застройки, в том числе: -Площадка размещения зданий НОП №1 -Площадка размещения зданий НОП №2 -Площадка Водоподготовки -Площадка ЛОС	%	6.35 28.14 10.66 1.57 3.09

7 Обоснование и описание решений по инженерной подготовке территории, в том числе решений по инженерной защите территории и объектов капитального строительства от последствий опасных геологических процессов, паводковых, поверхностных и грунтовых вод

В данном проекте применены следующие способы отвода поверхностных вод:

1) Свободный отвод. Стоки свободно на обочины, далее на откосы и на рельеф. Для этого предусмотрены соответствующие поперечные и продольные уклоны конструктивных элементов дороги.
2) Предусмотрена ливневая канализация на проектируемых на АД и площадках ЛОС и Водоподготовки

8 Описание организации рельефа вертикальной планировкой

Планировочные решения по вертикальному планированию территории приняты с учётом существующего рельефа площадки и отметок прилегающих существующих покрытий.

Организация рельефа участка строительства решена с учетом:

- высотных отметок существующих проездов;
- высотных отметок существующих зданий и сооружений;
- поверхностного водоотвода с территории участка.

План организации рельефа выполнен методом проектных горизонталей с сечением через 0.1 м. по всем планировочным элементам. Отвод поверхностных вод осуществляется сбросом в ливневую канализацию и с площадок на существующий рельеф. Объем земляных масс подсчитан по картограмме с разбивкой сетки квадратов 10х10м и 20х20м

9 Описание решений по благоустройству территории

Устройство проездов, площадок с твердыми покрытиями необходимо выполнить после окончания строительно-монтажных работ.

Проектом предусматривается устройство асфальтобетонных тротуаров с установкой бортовых камней для подходов к проектируемым зданиям.

Тип 1. Тротуар

Слой покрытия: асфальтобетон А5Вл по ГОСТ 58406.2-2020 на битуме PG 64-22 по ГОСТ 58400.1-2019, толщина 0,05м;

Слой основания: щебень М600 по ГОСТ 32703-2014 фр. 16-31.5мм, толщина 0,16м;

Разделяющая прослойка: геотекстиль 300гр/м2 по ГОСТ Р 56419-2015;

Дополнительный слой основания: песок очень мелкий по ГОСТ 32824-2014 Кф>1 м/сут, толщина 0,15м.

Тип 2. Отмостка зданий

Слой покрытия: асфальтобетон А5Вл по ГОСТ 58406.2-2020 на битуме PG 64-22 по ГОСТ 58400.1- 2019,толщина 0,05м;

Слой основания: щебень М-600 по ГОСТ 32703-2014 фр. 16-31.5мм 0,10м;

Гидроизоляция;

Утеплитель ЭППС 0,05м;

Дополнительный слой основания: песок очень мелкий по ГОСТ 32824-2014 Кф>1 м/сут 0,10м.

Тип 3. Проезды

Покрытие: Асфальтобетон А16В/Н по ГОСТ Р 58406.2-2020 на битумном вяжущем PG 64-34 по ГОСТ Р 58400.1-2019 0,05;

Нижний слой покрытия асфальтобетон А32Н/Н, по ГОСТ Р 58406.2-2020 на битумном вяжущем PG 64-34 по ГОСТ Р 58400.1-2019 0,08;

Основание: Щебень фракционированный фракции св. 31,5-63 мм М600 с расклинцовкой верхнего слоя щебнем фр. 4-8мм. и фр. 8-16мм М600 по ГОСТ 32703-2014 уложенный в один слой 0,22м;

Разделяющая прослойка - нетканый геотекстиль предельная прочность не менее 5кН/м, ГОСТ Р 56419-2015

Дополнительный слой основания - Песок мелкий по ГОСТ 32824-2014 с коэф. фильтрации Кф>2 м/сут 0,29

Примечания:

Марка щебня по дробимости, для устройства оснований, не менее М600.

Перед устройством асфальтобетонных покрытий по асфальтобетонным покрытиям производится розлив битумной эмульсии по ГОСТ Р 58952.1-2020 ЭБДК-Б из расчета 0,3л/м^2.

Перед устройством асфальтобетонных покрытий по основаниям из щебня производится розлив битумной эмульсии по ГОСТ Р 58952.1-2020 ЭБДК-Б из расчета 0,7л/м^2.

Укрепление откосов и территории благоустройства производится засевом многолетних трав по слою плодородного грунта, h=0,15м.

10 Обоснование зонирования территории земельных участков для размещения зданий строений и сооружений, а также принципиальная схема размещения территориальных зон с указанием сведений о расстояниях до ближайших установленных территориальных зон и мест размещения существующих и проектируемых зданий, строений и сооружений (основного, вспомогательного, подсобного, складского и обслуживающего назначения) объектов капитального строительства, входящих в инфраструктуру линейного объекта

Отдельное зонирование в зоне проектирования проектом не предусматривается Проектируемые объекты находятся в полосе отвода железной дороги и входят в ее инфраструктуру.

11 Обоснование схем транспортных коммуникаций, обеспечивающих внешние и внутренние (в том числе межцеховые) грузоперевозки

Проектируемые объекты находятся в полосе отвода железной дороги и входят в ее инфраструктуру. Указанная железная дорога не является объектом производственного назначения.

12 Характеристика и технические показатели транспортных коммуникаций объектов капитального строительства, входящих в инфраструктуру линейного объекта

Проектируемые объекты находятся в полосе отвода железной дороги и входят в ее инфраструктуру. Указанная железная дорога не является объектом производственного назначения.

13 Обоснование схем транспортных коммуникаций, обеспечивающих внешний и внутренний подъезд к объектам капитального строительства, входящих в инфраструктуру линейного объекта

Подъезды разработаны в соответствии с ГОСТ Р 58818-2020 “Дороги автомобильные с низкой интенсивностью движения” Категория автомобильных дорог принята VБ категории.

Поперечный профиль принят в соответствии с ГОСТ Р 58818-2020 “Дороги автомобильные с низкой интенсивностью движения” с шириной проезжей части 4,5 м.

Проезжая часть дорог запроектирована однополосная, с односкатным поперечным профилем.

Основные параметры поперечного профиля назначены с учетом проектных решений вертикальной планировки, размещения подземных и надземных коммуникаций.

14 Использованные документы и материалы

№ 190-ФЗ «Градостроительный кодекс Российской Федерации».

№ 69-ФЗ «О пожарной безопасности».

№ 136-ФЗ «Земельный кодекс Российской Федерации».

№ 384-ФЗ «Технический регламент о безопасности зданий сооружений».

№ 123-ФЗ «Технический регламент о требованиях пожарной безопасности».

Постановление Правительства Российской Федерации от 16 февраля 2008 года № 87 «О составе разделов проектной документации и требованиях к их содержанию».

СП 18.13330.2019 «Производственные объекты. Планировочная организация земельного участка» (СНиП II-89-80* «Генеральные планы промышленных предприятий»).

СП 42.13330.2016 «СНиП 2.07.01-89* Градостроительство. Планировка и застройка городских и сельских поселений».

СП 104.13330.2016 «СНиП 2.06.15-85 Инженерная защита территории от затопления и подтопления».

СП 116.13330.2012 «СНиП 22-02-2003 Инженерная защита территорий, зданий и сооружений от опасных геологических процессов. Основные положения».

15 Постановление об утверждении проекта планировки территории и проекта межевания территории

МИНИСТЕРСТВО СТРОИТЕЛЬСТВА, АРХИТЕКТУРЫ И ЖИЛИЩНО-КОММУНАЛЬНОГО ХОЗЯЙСТВА РЕСПУБЛИКИ ТАТАРСТАН

ТАТАРСТАН РЕСПУБЛИКАСЫ ТӨЗЕЛЕШ, АРХИТЕКТУРА ҺӘМ ТОРАК-КОММУНАЛЬ ХУҖАЛЫГЫ МИНИСТРЛЫГЫ

№ 1311/0

ПРИКАЗ

БОЕРЫК

«16» 09 2025

Об утверждении проекта планировки территории и проекта межевания территории, предусматривающих размещение линейного объекта «Инфраструктура индустриального парка «Этилен 600», Железнодорожная инфраструктура» 3 этап. Примыкание к станции Круглое Поле. Биклянского, Мелекесского, Круглопольского сельских поселений Тукаевского муниципального района

В целях обеспечения устойчивого развития территории, в соответствии со статьями 42, 43, 45 и 46 Градостроительного кодекса Российской Федерации, Законом Республики Татарстан от 23 декабря 2023 года № 131-ЗРТ «О перераспределении полномочий между органами местного самоуправления муниципальных образований Республики Татарстан и органами государственной власти Республики Татарстан в области градостроительной деятельности», приказом Министерства строительства, архитектуры и жилищно-коммунального хозяйства Республики Татарстан от 17.02.2025 № 132/о «О подготовке проекта планировки территории и проекта межевания территории объекта капитального строительства «Инфраструктура индустриального парка «Этилен 600», Железнодорожная инфраструктура» 3 этап. Примыкание к станции Круглое Поле. Биклянского, Мелекесского, Круглопольского сельских поселений Тукаевского муниципального района», учитывая протоколы публичных слушаний и заключение о результатах публичных слушаний, п р и к а з ы в а ю:

1. Утвердить прилагаемые проект планировки территории и проекта межевания территории, предусматривающие размещение линейного объекта «Инфраструктура индустриального парка «Этилен 600», Железнодорожная инфраструктура» 3 этап. Примыкание к станции Круглое Поле. Биклянского, Мелекесского, Круглопольского сельских поселений Тукаевского муниципального района».

2. Отделу развития Камской агломерации управления развития агломераций Департамента развития территорий (В.В. Бельскому) обеспечить:

направление настоящего приказа Руководителю Исполнительного комитета Тукаевского муниципального района Республики Татарстан в срок не позднее семи календарных дней с даты вступления его в силу;

размещение настоящего приказа на официальном сайте Министерства строительства, архитектуры и жилищно-коммунального хозяйства Республики Татарстан в информационно-телекоммуникационной сети «Интернет» в срок не позднее семи календарных дней с даты вступления его в силу;

размещение настоящего приказа в государственной информационной системе Республики Татарстан «Информационное обеспечение градостроительной деятельности Республики Татарстан» в течение 10 рабочих дней с даты его издания.

3. Юридическому отделу (Р.И. Кузьмину) обеспечить направление настоящего приказа на государственную регистрацию в Министерство юстиции Республики Татарстан.

4. Установить, что настоящий приказ вступает в силу со дня его официального опубликования.

5. Контроль за исполнением настоящего приказа возложить на начальника управления развития агломераций Департамента развития территорий С.А. Рыбакова.

Заместитель министра В.Н. Кудряшев

Министерство строительства, архитектуры и жилищно-коммунального хозяйства Республики Татарстан
Отдел контроля исполнения документов

Взам. инв №
Подпись и дата
Инв. № подл.

Изм.	Кол.Уч	Лист	№док.	Подпись	Дата	1439/2025/5-ИЛО1-ТЧ	Лист 13

Таблица регистрации изменений

Изм.	Номера листов (страниц)				Всего листов (страниц) в док.	Номер док.	Подп.	Дата
	изме–ненных	заме–ненных	новых	аннули–рован–ных				

Ведомость документов графической части

Обозначение	Наименование	Примечание
1439/2025/5-ИЛО1-ГЧ.01	Ведомость документов графической части	
1439/2025/5-ИЛО1-ГЧ.02	Ситуационный план	
1439/2025/5-ИЛО1-ГЧ.03	Схема планировочной организации земельного участка	
1439/2025/5-ИЛО1-ГЧ.04	Сводный план сетей инженерно-технического обеспечения	
1439/2025/5-ИЛО1-ГЧ.05	Схема организации рельефа и план земляных масс	

Взам. инв. №

Подп. и дата

Инв. № подл.

Изм.	Кол.уч	Лист	N°док.	Подпись	Дата
Разраб.		Бурайкин			18.05.26
Проверил		Сундеев			18.05.26
Н. контр.		Грошев			18.05.26

1439/2025/5-ИЛО1-ГЧ.01

Инфраструктура индустриального парка «Этилен-600», Железнодорожная инфраструктура. Этап №5. Строительство железнодорожных путей необщего пользования (приемоотправочный парк ст. Круглое Поле)


Этап №5

Стадия	Лист	Листов
П		1

Ведомость документов графической части

ГРАДО ПРОЕКТ

Формат А4

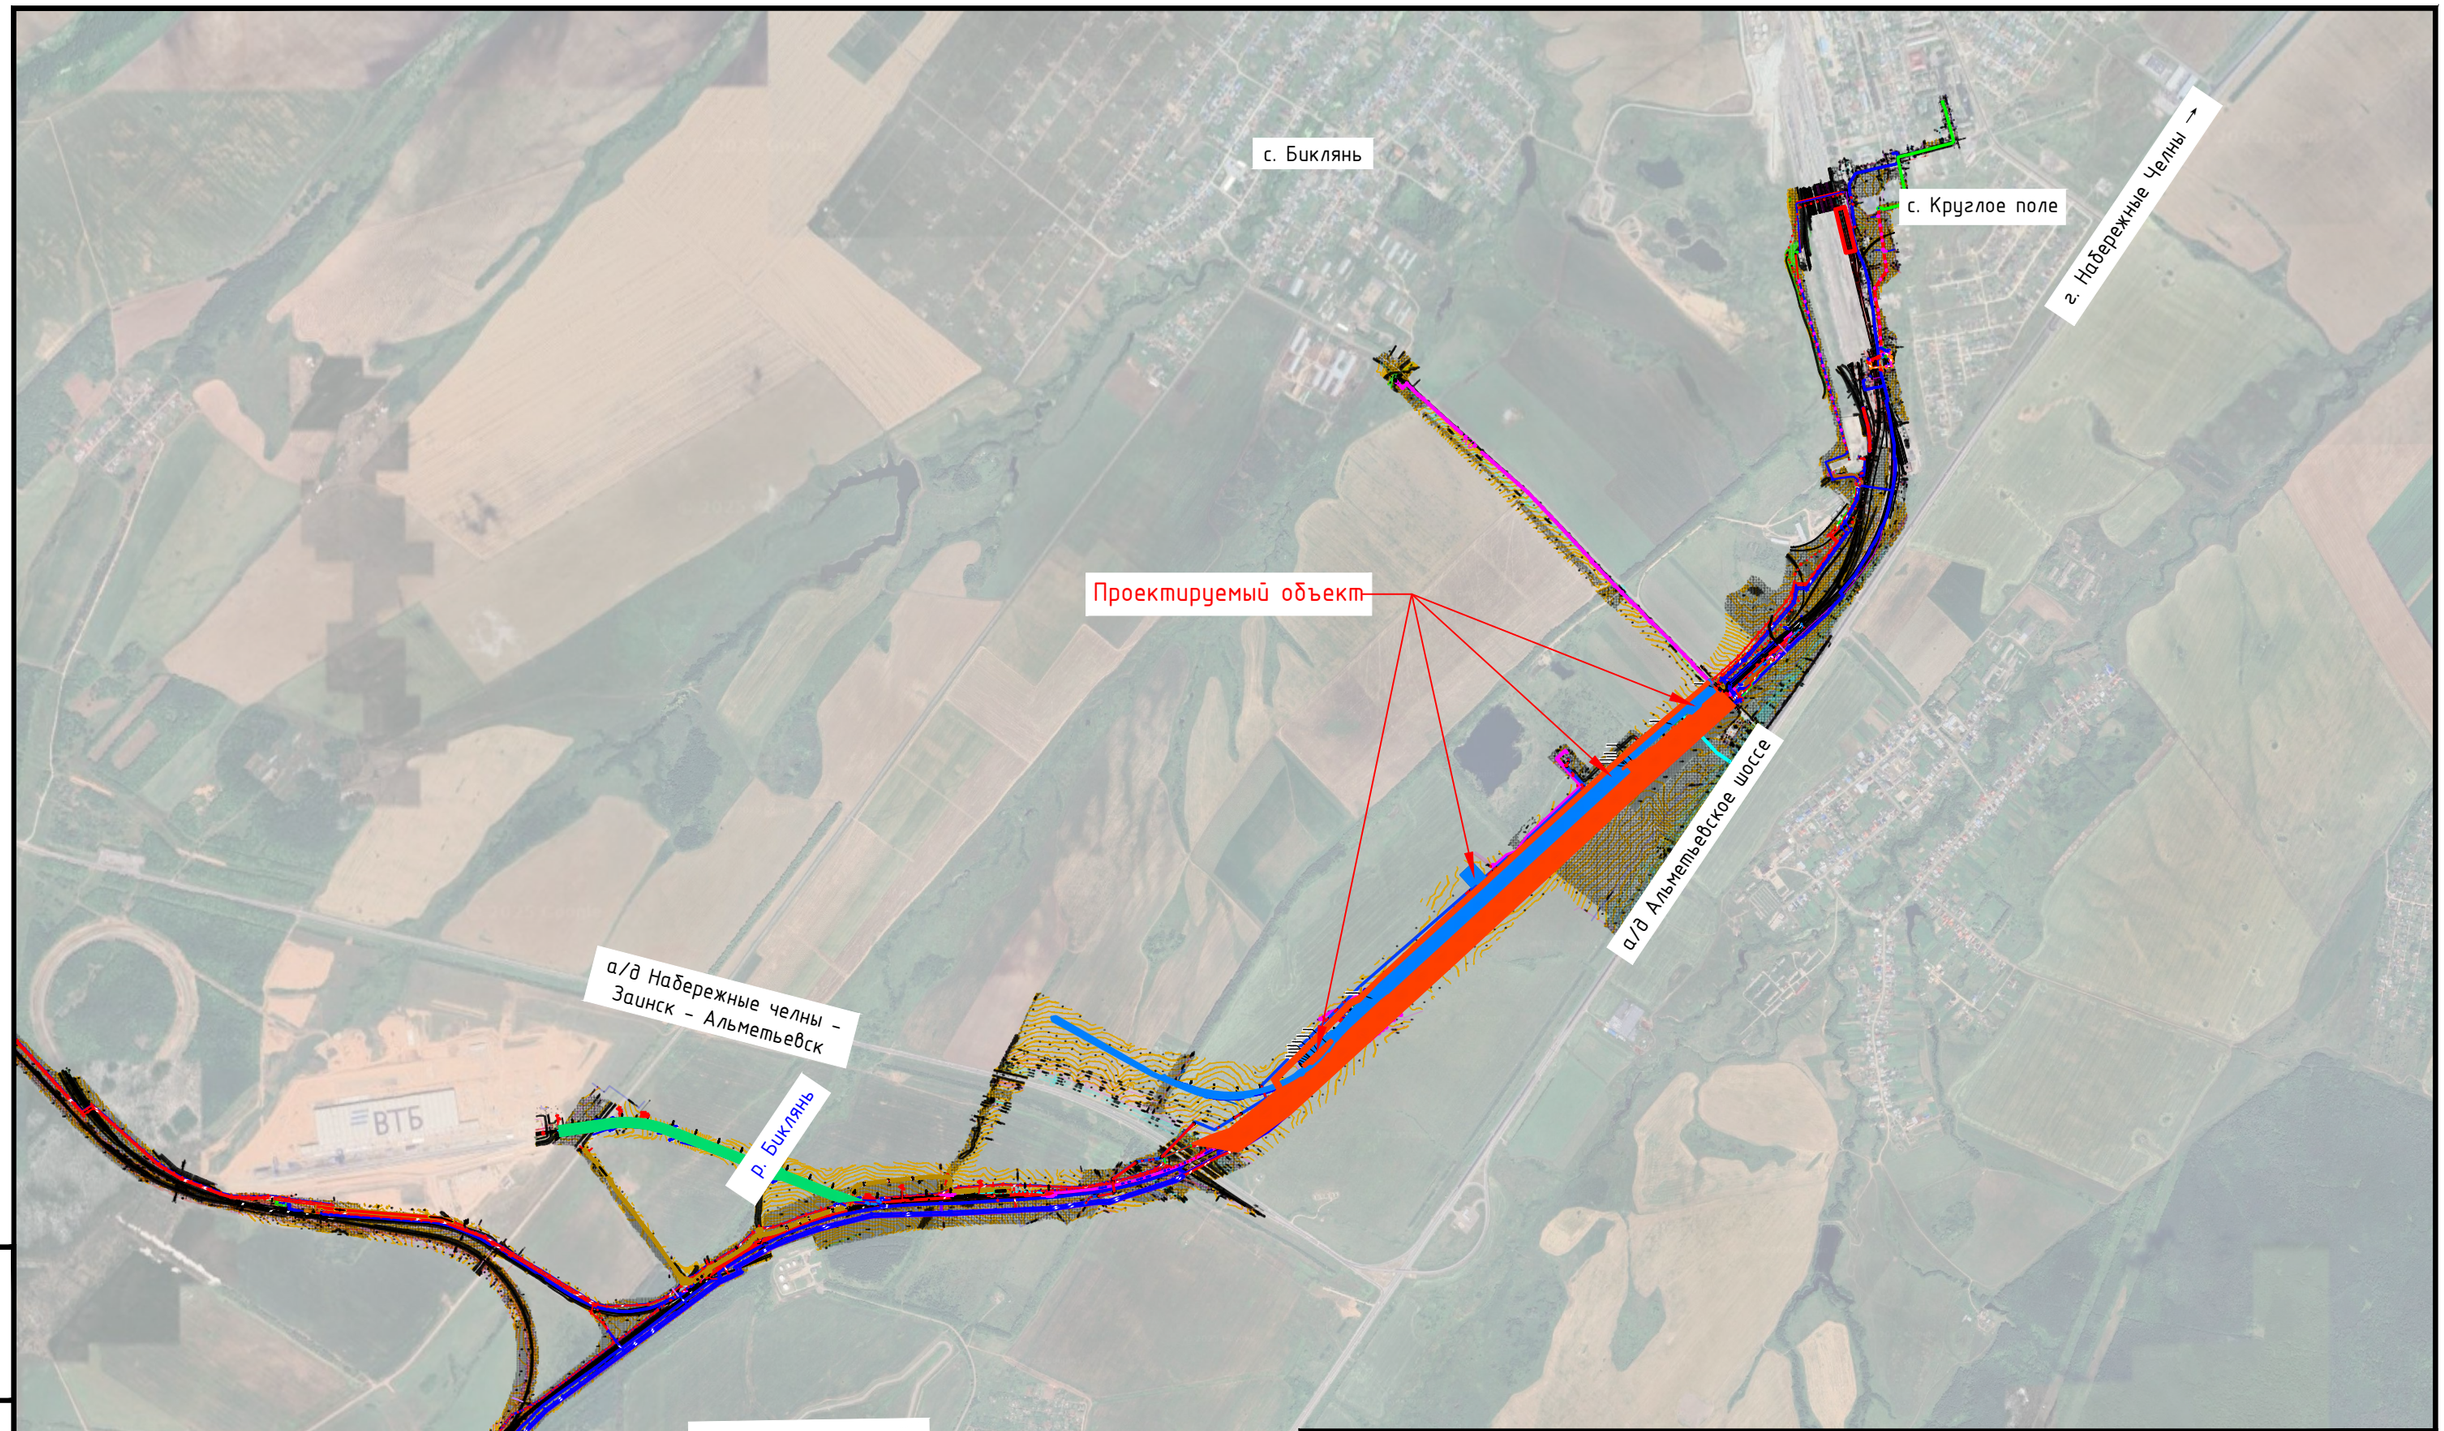

Взам. инв. №

Подп. и дата

Инв. № подл.

Изм.	Кол.уч	Лист	N°док.	Подпись	Дата
Разраб.		Бурайкин			18.05.26
Проверил		Сундеев			18.05.26
Н. контр.		Грошев			18.05.26

1439/2025/5-ИЛО1-ГЧ.02

Инфраструктура индустриального парка «Этилен-600», Железнодорожная инфраструктура. Этап №5. Строительство железнодорожных путей необщего пользования (приемоотправочный парк ст. Круглое Поле)


Этап №5	Стадия	Лист	Листов
	П		1

Ситуационный план

ГРАДО ПРОЕКТ

Формат А3

Площадка размещения зданий необщего пользования №1

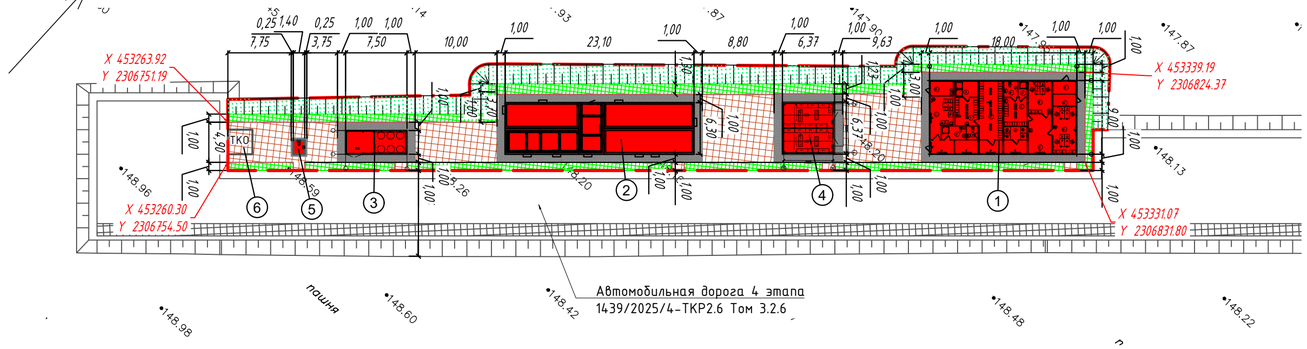

Экспликация зданий и сооружений


Номер на плане	Наименование	Примечание
1	Административно-бытовой модуль	Проектируемое
2	Мобильный комплекс железнодорожной Автоматики, телемеханики и связи (МК АТС)	Проектируемое
3	Модульная компрессорная	Проектируемое
4	Кладовая для хранения путевого инструмента и материалов ВСП	Проектируемое
5	Туалетный модуль 1.4х1.7	Проектируемое
6	ТКО	Проектируемое

Условные обозначения

	Граница проектирования благоустройства
	Проектируемое здание
	Тротуар из асфальтобетона
	Отмостка
	Газон
	Откос
	Бортовой камень БР100.20.8
	Бровка земляного полотна


Установка бортового камня БР100.20.8 в сопряжении тротуара и газона

Тротуар
Тип 1

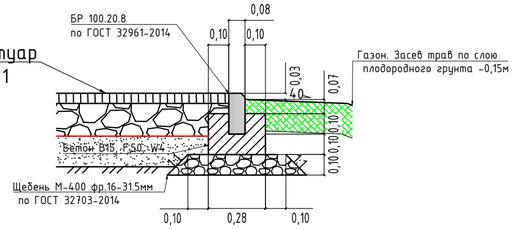


Установка бортового камня БР100.20.8 в сопряжении отмостки и газона

Отмостка зданий
Тип 2

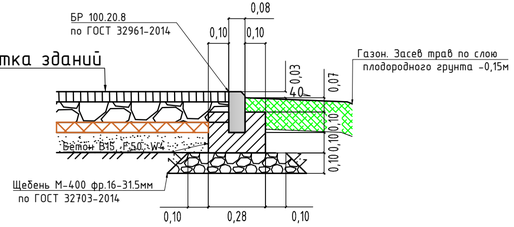


Тип 1. Тротуар

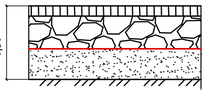


Покрытие: асфальтобетон А5Вл по ГОСТ 58406.2-2020 на битуме PG 64-22 вяжущее по ГОСТ 58400.1-2019	-0,05м
Слой основания: щебень М-600 по ГОСТ 32703-2014 фр. 16-31.5мм	-0,16м
Разделяющая прослойка: нетканый геотекстиль предельная прочность не менее 5кН/м, ГОСТ Р 56419-2015	
Дополнительный слой основания: песок очень мелкий по ГОСТ 32824-2014 Кф>1 м/сут	-0,15м

Тип 2. Отмостка зданий

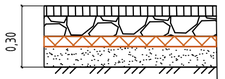

Покрытие: асфальтобетон А5Вл по ГОСТ 58406.2-2020 на битуме PG 64-22 вяжущее по ГОСТ 58400.1-2019	-0,05м
Слой основания: щебень М-600 по ГОСТ 32703-2014 фр. 16-31.5мм	-0,10м
Гидроизоляция	
Утеплитель ЭППС	-0,05м
Дополнительный слой основания: песок очень мелкий по ГОСТ 32824-2014 Кф>1 м/сут	-0,10м

Укрепление откосов

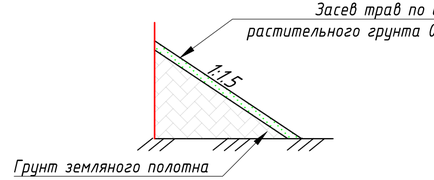


						1439/2025/5-ИЛ01-ГЧ.03	
						Инфраструктура индустриального парка «Этилен-600», Железнодорожная инфраструктура. Этап №5. Строительство железнодорожных путей необщего пользования (приемоотправочный парк ст. Круглое Поле)	
Изм.	Кол.уч	Лист	№док.	Подпись	Дата		
Разраб.		Бурайкин			18.05.26	Этап №5	Стадия: П; Лист: 1; Листов: 4
Проверил		Сундеев			18.05.26		
Н. контр.		Грошев			18.05.26	Схема планировочной организации земельного участка М 1:500	ГРАДО ПРОЕКТ

Взам. инв. №
Подп. и дата
Инв. № подл.

Формат А4х3


Площадка размещения зданий необщего пользования №2

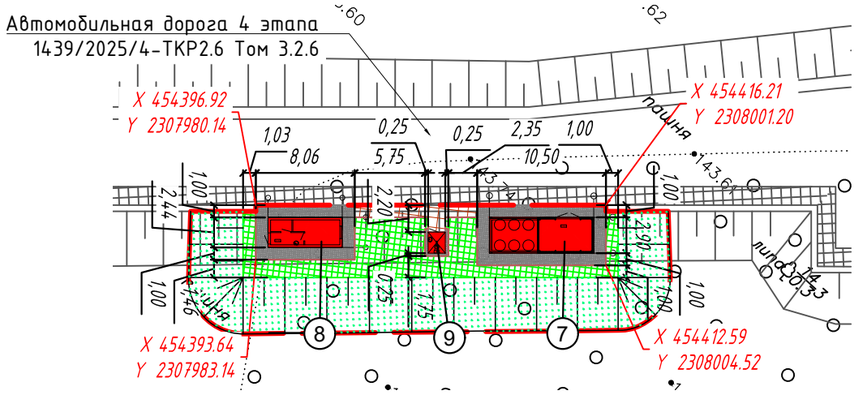


Тип 1. Тротуар

Покрытие: асфальтобетон А5Вл по ГОСТ 58406.2-2020 на битуме PG 64-22 вяжущее по ГОСТ 58400.1-2019	-0,05м
Слой основания: щебень М-600 по ГОСТ 32703-2014 фр. 16-31.5мм	-0,16м
Разделяющая прослойка: нетканый геотекстиль предельная прочность не менее 5кН/м, ГОСТ Р 56419-2015	
Дополнительный слой основания: песок очень мелкий по ГОСТ 32824-2014 Кф>1 м/сут	-0,15м

Укрепление откосов

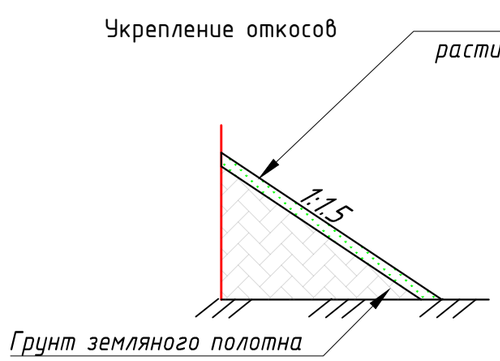

Тип 2. Отмостка зданий

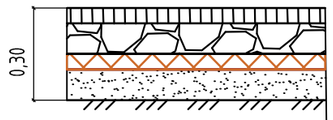

Покрытие: асфальтобетон А5Вл по ГОСТ 58406.2-2020 на битуме PG 64-22 вяжущее по ГОСТ 58400.1-2019	-0,05м
Слой основания: щебень М-600 по ГОСТ 32703-2014 фр. 16-31.5мм	-0,10м
Гидроизоляция	
Утеплитель ЭППС	-0,05м
Дополнительный слой основания: песок очень мелкий по ГОСТ 32824-2014 Кф>1 м/сут	-0,10м


Экспликация зданий и сооружений

Номер на плане	Наименование	Примечание
7	Модульная компрессорная	Проектируемое
8	Модульный пункт обогрева	Проектируемое
9	Туалетный модуль 1.4х1.7	Проектируемое


Условные обозначения

	Граница проектирования благоустройства
	Проектируемое здание
	Тротуар из асфальтобетона
	Отмостка
	Газон
	Откос
	Бортовой камень БР100.20.8
	Бровка земляного полотна

Установка бортового камня БР100.20.8
в сопряжении тротуара и газона

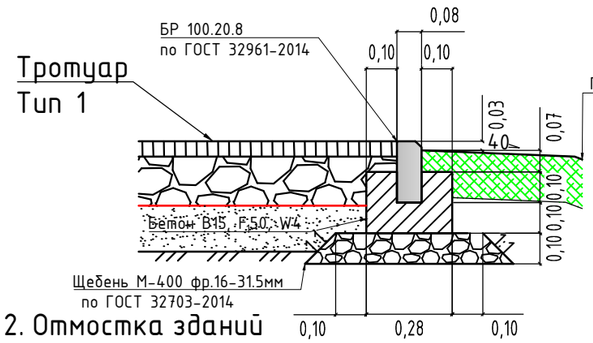

Установка бортового камня БР100.20.8
в сопряжении отмостки и газона

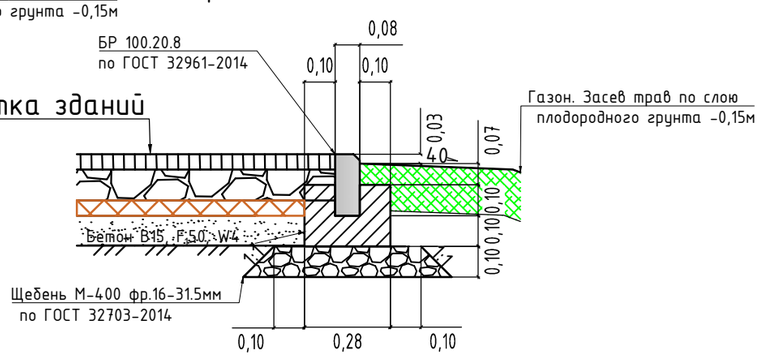

Изм.	Кол.уч	Лист	N°док.	Подпись	Дата
Разраб.		Бурайкин			18.05.26
Проверил		Сундеев			18.05.26
Н. контр.		Грошев			18.05.26

1439/2025/5-ИЛО1-ГЧ.03

Инфраструктура индустриального парка «Этилен-600», Железнодорожная инфраструктура. Этап №5. Строительство железнодорожных путей необщего пользования (приемоотправочный парк ст. Круглое Поле)

Этап №5

Стадия	Лист	Листов
П	2	4


Схема планировочной организации земельного участка
М 1:500

ГРАДО ПРОЕКТ


Взам. инв. N°
Подп. и дата
Инв. N° подл.

Формат А3

Площадка Водоподготовки

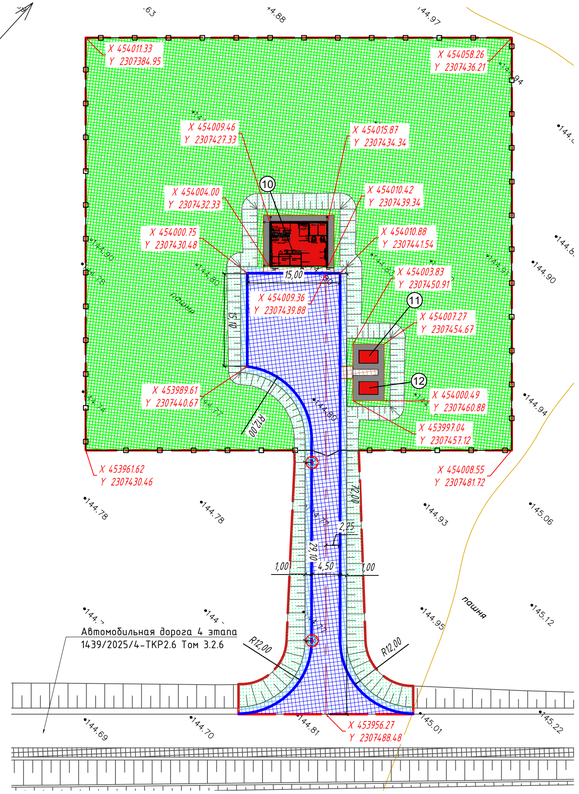


Тип 2. Отмостка зданий

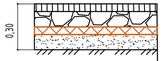


Покрытие: асфальтобетон А5Вл по ГОСТ 58406.2-2020 на битуме PG 64-22 вяжущее по ГОСТ 58400.1-2019	-0,05м
Слой основания: щебень М-600 по ГОСТ 32703-2014 фр. 16-31.5мм	-0,10м
Гидроизоляция	
Утеплитель ЭППС	-0,05м
Дополнительный слой основания: песок очень мелкий по ГОСТ 32824-2014 Кф>1 м/сут	-0,10м

Тип 1. Тротуар

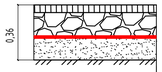


Покрытие: асфальтобетон А5Вл по ГОСТ 58406.2-2020 на битуме PG 64-22 вяжущее по ГОСТ 58400.1-2019	-0,05м
Слой основания: щебень М-600 по ГОСТ 32703-2014 фр. 16-31.5мм	-0,16м
Разделяющая прослойка: нетканый геотекстиль предельная прочность не менее 5кН/м, ГОСТ Р 56419-2015	
Дополнительный слой основания: песок очень мелкий по ГОСТ 32824-2014 Кф>1 м/сут	-0,15м


Установка бортового камня БР100.20.8 в сопряжение тротуара и газона

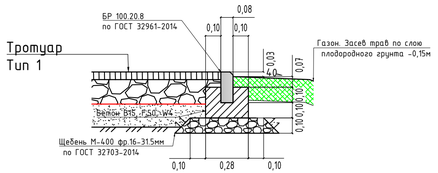


Установка бортового камня БР100.20.8 в сопряжении отмостки и газона

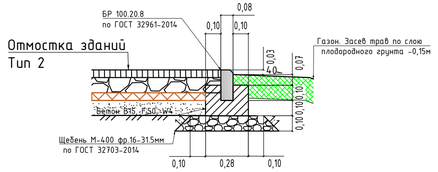

Поперечный разрез асфальтобетонного проезда

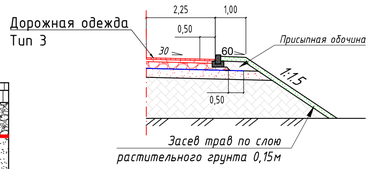

Тип 3. Асфальтобетонный проезд

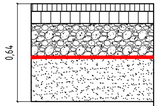

Верхний слой покрытия - Асфальтобетон $A16B_{II}$ по ГОСТ Р 58406.2-2020 на битумном вяжущем PG 64-34 по ГОСТ Р 58400.1-2019	-0,05м
Нижний слой покрытия - Асфальтобетон $A32H_{II}$ по ГОСТ Р 58406.2-2020 на битумном вяжущем PG 64-34 по ГОСТ Р 58400.1-2019	-0,08м
Слой основания - Щебень фракционированный фракции св. 31,5-63 мм М600 с расклинцовкой верхнего слоя щебнем фр. 4-8мм. и фр. 8-16мм М600 по ГОСТ 32703-2014 уложенный в один слой	-0,22м
Разделяющая прослойка - нетканый геотекстиль предельная прочность не менее 5кН/м, ГОСТ Р 56419-2015	
Дополнительный слой основания - Песок мелкий по ГОСТ 32824-2014 с коэф. фильтрации Кф>2 м/сут.	-0,29м
Грунт рабочего слоя - глина	

Примечание:

1. Все размеры даны в метрах, поперечные уклоны в промилле.
2. Дорожно-климатическая зона - II_2.
3. Тип дорожной одежды - облегченный.
4. Перед устройством асфальтобетонных покрытий (оснований) по основаниям из щебня производится розлив битумной эмульсии по ГОСТ Р 58952.1-2020 ЭБДК-Б из расчета 0,7л/м^2.
5. Перед устройством асфальтобетонных покрытий по асфальтобетонным покрытиям (основаниям) производится розлив битумной эмульсии по ГОСТ Р 58952.1-2020 ЭБДК-Б из расчета 0,3 л/м^2.
6. Расчет прочности дорожной одежды выполнен по ГОСТ Р 71404-2024.
7. Класс асфальтобетона А16Вн по истираемости не ниже 2.
8. Марка щебня по сопротивлению истираемости по показателю микро-Деваль для приготовления А16Вн - МД2 или МД1.
9. Марка щебня по дробимости, для устройства оснований, не менее М600.


Экспликация зданий и сооружений

Номер на плане	Наименование	Примечание
10	Водоподготовка	Проектируемое
11, 12	Трансформаторная подстанция	Проектируемое

Условные обозначения

	Граница проектирования благоустройства
	Проектируемое здание
	Асфальтобетонный проезд
	Тротуар из асфальтобетонна
	Отмостка из асфальтобетонна
	Обочина
	Газон
	Откос
	Бортовой камень БР100.30.15
	Бортовой камень БР100.20.8
	Бровка земляного полотна
	Ось проезда
	Дождеприемный колодец
	Ограждение l=269,30 м
	Ворота распашные 4,5 м

Укрепление откосов

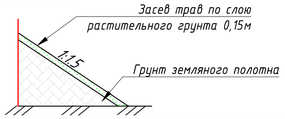

Изм.	Кол.уч.	Лист	N°док.	Подпись	Дата
Разраб.		Бурайкин			18.05.26
Проверил		Сундеев			18.05.26
Н. контр.		Грошев			18.05.26

1439/2025/5-ИЛО1-ГЧ.03

Инфраструктура индустриального парка «Этилен-600», Железнодорожная инфраструктура. Этап №5. Строительство железнодорожных путей необщего пользования (приемоотправочный парк ст. Круглое Поле)

Стадия	Лист	Листов
П	3	4

Этап №5

Схема планировочной организации земельного участка
М 1:500

ГРАДО ПРОЕКТ


Формат А4х4

Взам. инв. N°

Подп. и дата

Инв. N° подл.


Площадка локальных очистных сооружений

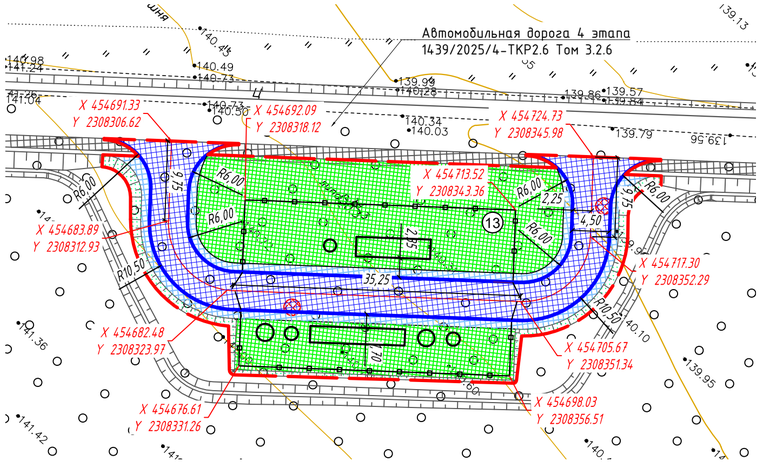

Примечание:


1. Все размеры даны в метрах, поперечные уклоны в промилле.
2. Дорожно-климатическая зона – II_2.
3. Тип дорожной одежды – облегченный.
4. Перед устройством асфальтобетонных покрытий (оснований) по основаниям из щебня производится розлив битумной эмульсии по ГОСТ Р 58952.1-2020 ЭБДК-Б из расчета 0,7л/м^2.
5. Перед устройством асфальтобетонных покрытий по асфальтобетонным покрытиям (основаниям) производится розлив битумной эмульсии по ГОСТ Р 58952.1-2020 ЭБДК-Б из расчета 0,3 л/м^2.
6. Расчет прочности дорожной одежды выполнен по ГОСТ Р 71404-2024.
7. Класс асфальтобетона А16Вн по истираемости не ниже 2.
8. Марка щебня по сопротивлению истираемости по показателю микро-Деваль для приготовления А16Вн – МД2 или МД1.
9. Марка щебня по дробимости, для устройства оснований, не менее М600.

Тип 3. Асфальтобетонный проезд

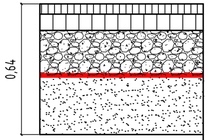

Верхний слой покрытия – Асфальтобетон А16$В_Н$ по ГОСТ Р 58406.2-2020 на битумном вяжущем PG 64-34 по ГОСТ Р 58400.1-2019	–0,05м
Нижний слой покрытия – Асфальтобетон А32$Н_Н$ по ГОСТ Р 58406.2-2020 на битумном вяжущем PG 64-34 по ГОСТ Р 58400.1-2019	–0,08м
Слой основания – Щебень фракционированный фракции св. 31,5-63 мм М600 с расклинцовкой верхнего слоя щебнем фр. 4-8мм. и фр. 8-16мм М600 по ГОСТ 32703-2014 уложенный в один слой	–0,22м
Разделяющая прослойка – нетканый геотекстиль предельная прочность не менее 5кН/м, ГОСТ Р 56419-2015	
Дополнительный слой основания – Песок мелкий по ГОСТ 32824-2014 с коэф. фильтрации Кф>2 м/сут.	–0,29м
Грунт рабочего слоя – глина	

Поперечный разрез асфальтобетонного проезда

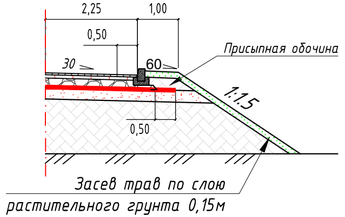


Экспликация зданий и сооружений

Номер на плане	Наименование	Примечание
13	Локальные очистные сооружения (ЛОС)	Проектируемое

Условные обозначения

	Граница проектирования благоустройства
	Проектируемые сооружения
	Асфальтобетонный проезд
	Обочина
	Газон
	Откос
	Бортовой камень БР100.30.15
	Бровка земляного полотна
	Ось проезда
	Ограждение l=97,90 м
	Ворота распашные 4,5 м

Укрепление откосов

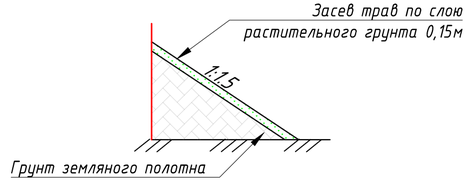

						1439/2025/5-ИЛО1-ГЧ.03	
						Инфраструктура индустриального парка «Этилен-600», Железнодорожная инфраструктура. Этап №5. Строительство железнодорожных путей необщего пользования (приемоотправочный парк ст. Круглое Поле)	
Изм.	Кол.уч	Лист	№док.	Подпись	Дата		
Разраб.		Бурайкин			18.05.26	Этап №5	Стадия: П; Лист: 4; Листов: 4
Проверил		Сундеев			18.05.26		
Н. контр.		Грошев			18.05.26	Схема планировочной организации земельного участка М 1:500	ГРАДО ПРОЕКТ


Взам. инв. №

Подп. и дата

Инв. № подл.

Формат А4х3

Площадка размещения зданий необщего пользования №1

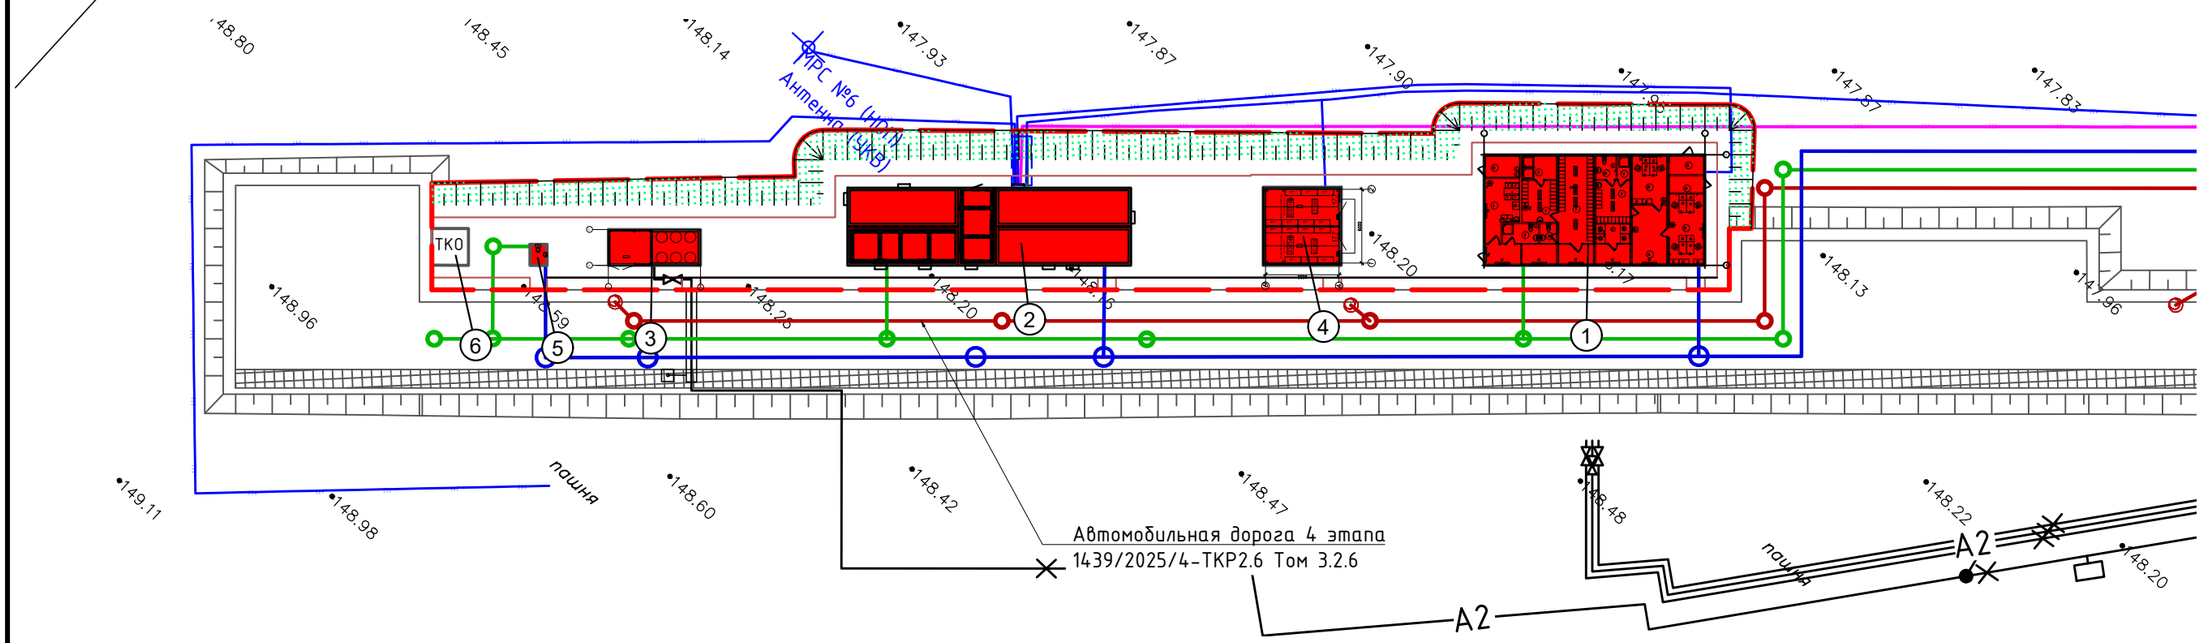

Экспликация зданий и сооружений

Номер на плане	Наименование	Примечание
1	Административно-бытовой модуль	Проектируемое
2	Мобильный комплекс железнодорожной Автоматики, телемеханики и связи (МК АТС)	Проектируемое
3	Модульная компрессорная	Проектируемое
4	Кладовая для хранения путевого инструмента и материалов ВСП	Проектируемое
5	Туалетный модуль 1.4х1.7	Проектируемое
6	ТКО	Проектируемое

Условные обозначения

	Граница проектирования благоустройства
	Проектируемое здание
	Проектируемые сети связи
	Проектируемая сеть воздуховода
WK	Проектируемая кабельная линия электропередач
	Проектируемый водопровод
	Проектируемая бытовая канализация
	Проектируемая ливневая канализация
W1	Кабельная линия 6 кВ в траншее
W2	Кабельная линия 0,4 кВ в траншее

Взам. инв. №

Подп. и дата

Инв. № подл.

Изм.	Кол.уч	Лист	№док.	Подпись	Дата
Разраб.		Бурайкин			18.05.26
Проверил		Сундеев			18.05.26
Н. контр.		Грошев			18.05.26

1439/2025/5-ИЛО1-ГЧ.04

Инфраструктура индустриального парка «Этилен-600», Железнодорожная инфраструктура. Этап №5. Строительство железнодорожных путей необщего пользования (приемоотправочный парк ст. Круглое Поле)

Этап №5	Стадия	Лист	Листов
	П	1	4


Сводный план сетей инженерно-технического обеспечения М1:500

ГРАДО ПРОЕКТ

Формат А3

Площадка размещения зданий необщего пользования №2

Автомобильная дорога 4 этапа
1439/2025/4-ТКР2.6 Том 3.2.6

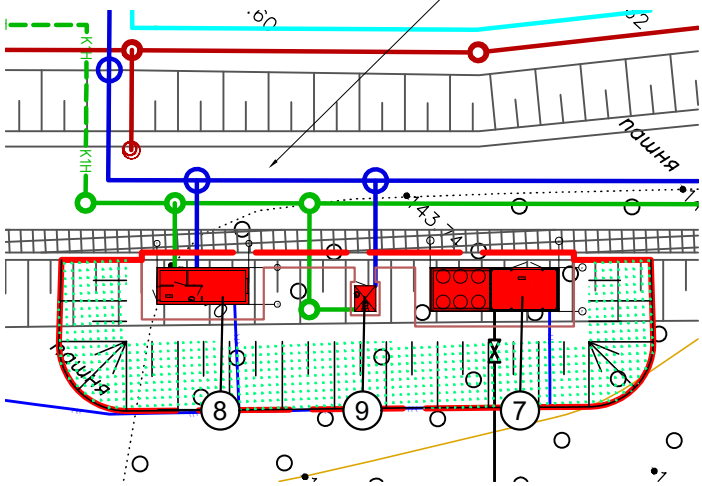

Экспликация зданий и сооружений

Номер на плане	Наименование	Примечание
7	Модульная компрессорная	Проектируемое
8	Модульный пункт обогрева	Проектируемое
9	Туалетный модуль 1.4х1.7	Проектируемое

Условные обозначения

	Граница проектирования благоустройства
	Проектируемое здание
	Проектируемый водопровод
	Проектируемая бытовая канализация
	Проектируемая ливневая канализация

Взам. инв. №

Подп. и дата

Инв. № подл.

Изм.	Кол.уч	Лист	№док.	Подпись	Дата
Разраб.		Бурайкин			18.05.26
Проверил		Сундеев			18.05.26
Н. контр.		Грошев			18.05.26

1439/2025/5-ИЛО1-ГЧ.04

Инфраструктура индустриального парка «Этилен-600», Железнодорожная инфраструктура. Этап №5. Строительство железнодорожных путей необщего пользования (приемоотправочный парк ст. Круглое Поле)

Этап №5


Стадия	Лист	Листов
П	2	4

Сводный план сетей инженерно-технического обеспечения
М1:500

ГРАДО ПРОЕКТ

Формат А4

Площадка Водоподготовки

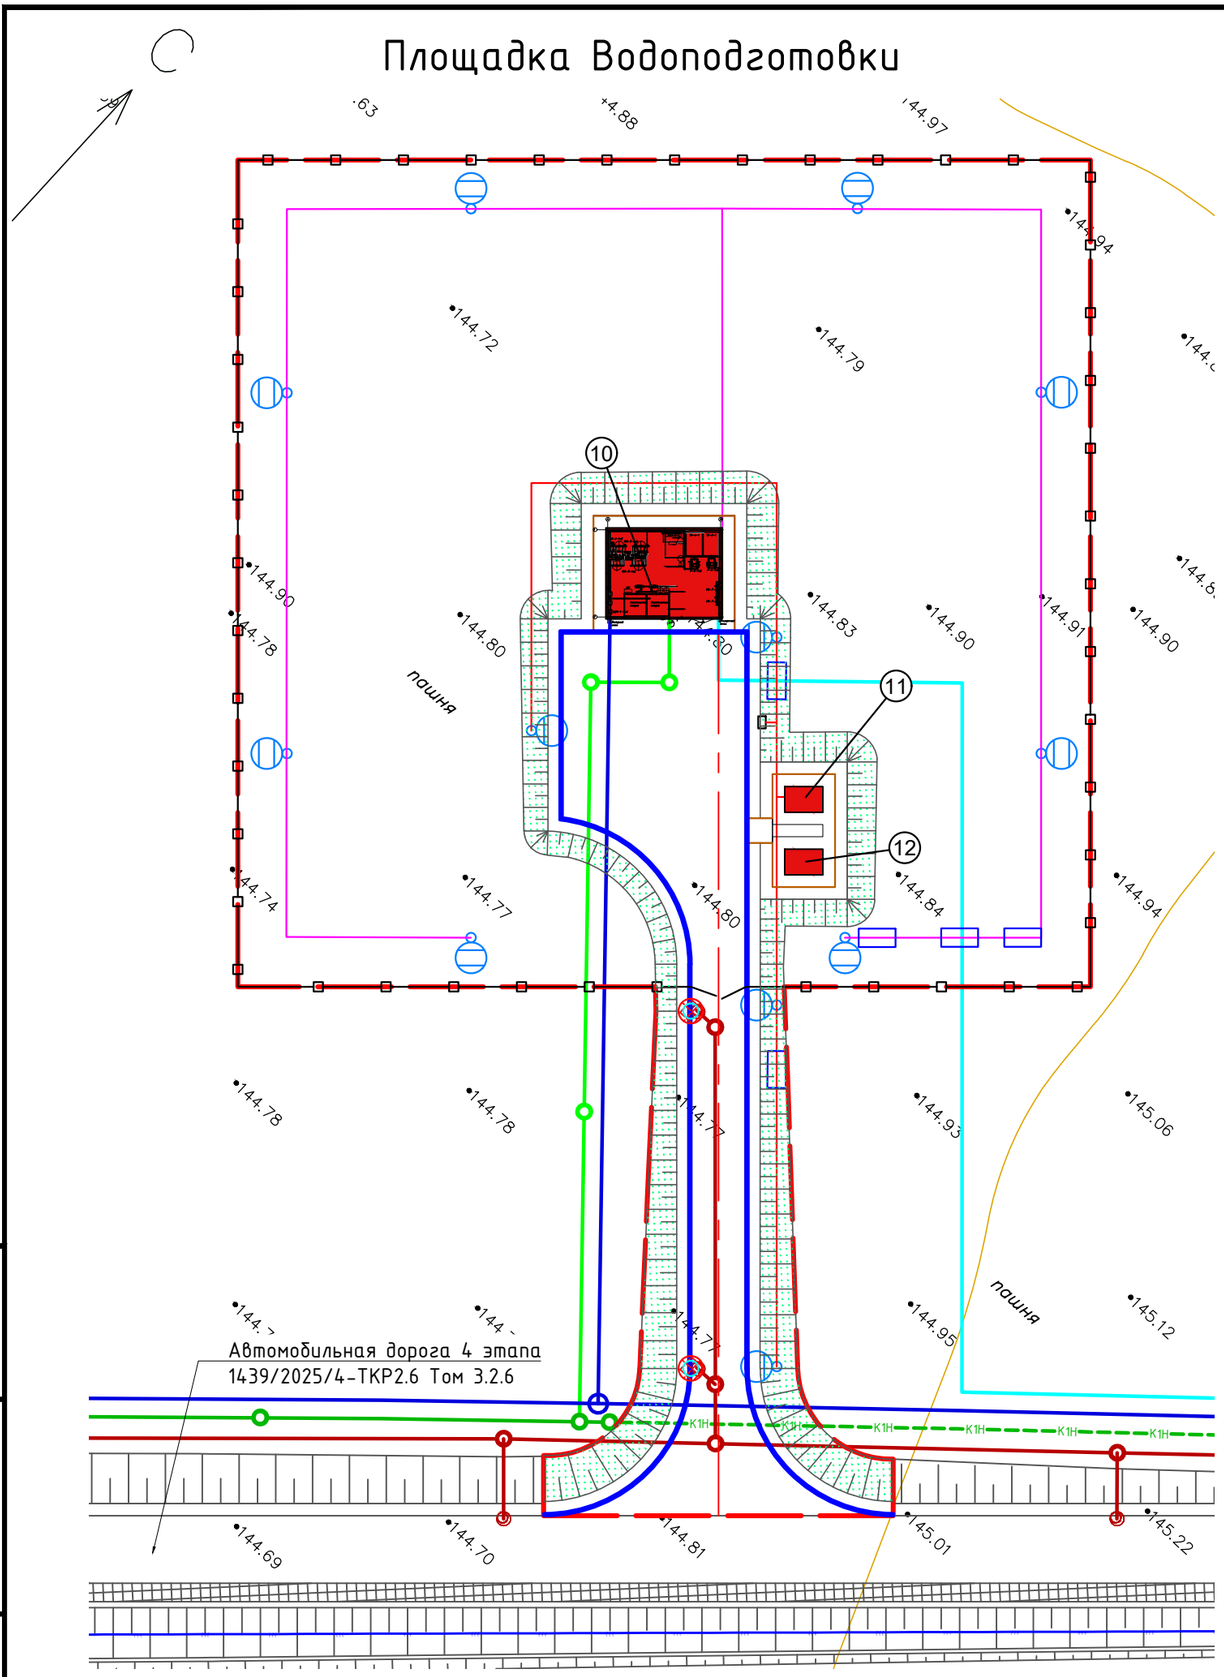

Экспликация зданий и сооружений

Номер на плане	Наименование	Примечание
10	Водоподготовка	Проектируемое
11, 12	Трансформаторная подстанция	Проектируемое

Условные обозначения

	Граница проектирования благоустройства
	Проектируемое здание
	Проектируемые сети связи
	Проектируемая сеть воздуховода
	Проектируемая кабельная линия электропередач
	Проектируемый водопровод
	Проектируемая бытовая канализация
	Проектируемая ливневая канализация
W1	Кабельная линия 6 кВ в траншее
W2	Кабельная линия 0,4 кВ в траншее
	Мачта освещения
	Дождеприемный колодец
	Ограждение l=269,30 м
	Ворота распашные 4,5 м

Изм.	Кол.уч	Лист	N°док.	Подпись	Дата
Разраб.		Бурайкин			18.05.26
Проверил		Сундеев			18.05.26
Н. контр.		Грошев			18.05.26

1439/2025/5-ИЛ01-ГЧ.04

Инфраструктура индустриального парка «Этилен-600», Железнодорожная инфраструктура. Этап №5. Строительство железнодорожных путей необщего пользования (приемоотправочный парк ст. Круглое Поле)

Стадия	Лист	Листов
П	3	4

Этап №5

Сводный план сетей инженерно-технического обеспечения М1:500

ГРАДО ПРОЕКТ


Взам. инв. N°

Подп. и дата

Инв. N° подл.

Формат А3

Площадка локальных очистных сооружений

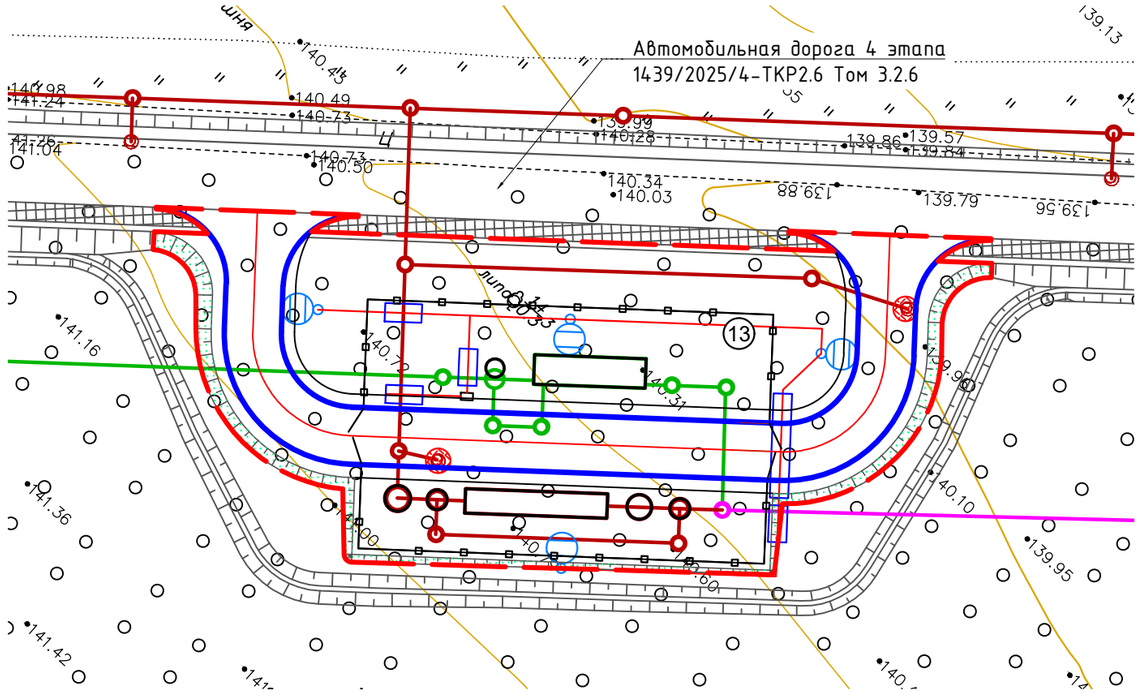

Экспликация зданий и сооружений

Номер на плане	Наименование	Примечание
13	Локальные очистные сооружения (ЛОС)	Проектируемое

Условные обозначения

	Граница проектирования благоустройства
	Проектируемое здание
	Проектируемые сети связи
	Проектируемая сеть воздуховода
	Проектируемая кабельная линия электропередач
	Проектируемый водопровод
	Проектируемая бытовая канализация
	Проектируемая ливневая канализация
W1	Кабельная линия 6 кВ в траншее
W2	Кабельная линия 0,4 кВ в траншее
	Мачта освещения
	Дождеприемный колодец
	Ограждение l=97,90 м
	Ворота распашные 4,5 м

Взам. инв. №

Подп. и дата

Инв. № подл.

Изм.	Кол.уч	Лист	№док.	Подпись	Дата
Разраб.		Бурайкин			18.05.26
Проверил		Сундеев			18.05.26
Н. контр.		Грошев			18.05.26

1439/2025/5-ИЛО1-ГЧ.04

Инфраструктура индустриального парка «Этилен-600», Железнодорожная инфраструктура. Этап №5. Строительство железнодорожных путей необщего пользования (приемоотправочный парк ст. Круглое Поле)

Этап №5


Стадия	Лист	Листов
П	4	4


Сводный план сетей инженерно-технического обеспечения
М1:500

ГРАДО ПРОЕКТ

Формат А3

Площадка размещения зданий необщего пользования №1

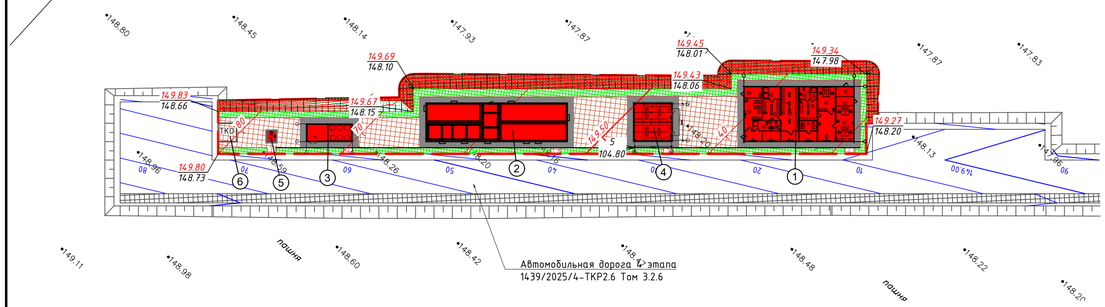

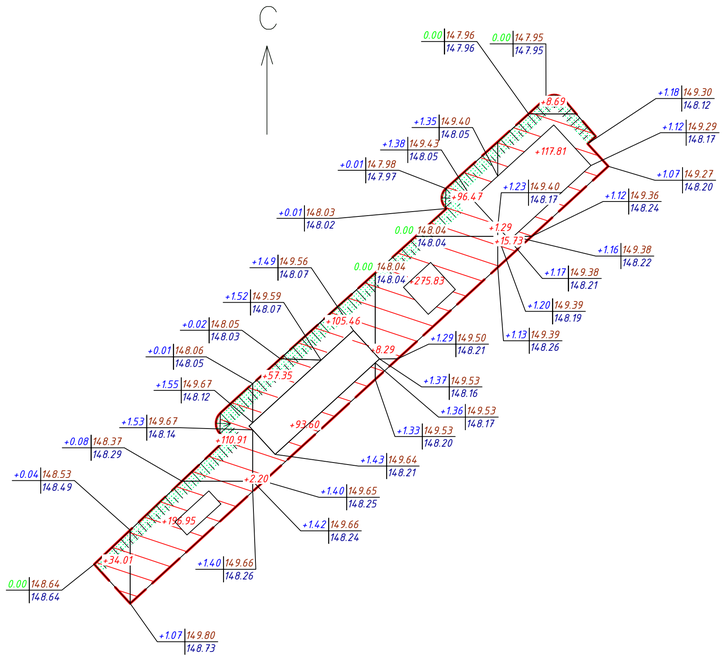

Экспликация зданий и сооружений

Номер на плане	Наименование	Примечание
1	Административно-бытовой модуль	Проектируемое
2	Мобильный комплекс железнодорожной Автоматики, телемеханики и связи (МК АТС)	Проектируемое
3	Модульная компрессорная	Проектируемое
4	Кладовая для хранения путевого инструмента и материалов ВСП	Проектируемое
5	Туалетный модуль 1.4х1.7	Проектируемое
6	ТКО	Проектируемое

Условные обозначения

	Граница проектирования благоустройства
	Проектируемое здание
	Тротуар из асфальтобетона
	Отмостка
	Газон
	Откос
	Бортовой камень БР100.20.8
	Бровка земляного полотна
	Проектная горизонталь
	Проектная горизонталь АД 4 этапа 1439/2025/4-ТКР2.6 Том 3.2.6
5 / 104.80	Направление уклона проектируемого рельефа
149.94 / 147.98	Отметка поверхности (проектная / существующая)

1. Система высот Балтийская 1977 г.
2. Система координат местная.
3. Отметки и уклоноуказатели приведены по верху покрытия.

Условные обозначения



Ведомость объемов земляных масс

Наименование грунта	Количество, м³		Приме-чание
	Насыпь (+)	Выемка (–)	
1. Грунт планировки территории	1125	–	
2. Вытесненный грунт, в т.ч. при устройстве:		225	
а) тротуара		98	
б) отмостки		53	
в) газона и откоса		74	
3. Поправка на уплотнение, k=0,1	113	–	
4. Всего пригодного грунта	1238	225	
5. Недостаток пригодного грунта		1013	
7. Плодородный грунт, всего:			
а) используемый для озеленения территории	74	–	
б) недостаток плодородного грунта		74	
8. Итого перерабатываемого грунта	1312	1312	

Итого, м³						Всего, м³	
	Насыпь	+34.01	+307.86	+258.61	+380.59	+143.52	+1125
	Выемка	–	–	–	–	–	–

Площадь картограммы – 947.21 м², в т.ч.:
насыпь – 947.21 м², выемка – 0.00 м²

1. Система высот Балтийская 1977 г.
2. Система координат местная.
3. Картограмма разработана в программном комплексе Civil3d.
4. При расчете картограммы квадраты сетки приняты стороной равной 20 м.
5. Необходимость замены грунта под зданиями и сооружениями определена в марке КР.
6. Коэффициент уплотнения – не менее 0,95. Толщина каждого слоя 0,3–0,6 м (уточняется по результатам опытного уплотнения).
7. После возведения земляного полотна откосы необходимо доуплотнять планировщиками-уплотнителями.

							1439/2025/5-ИЛО1-ГЧ.05
							Инфраструктура индустриального парка «Этилен-600», Железнодорожная инфраструктура. Этап №5. Строительство железнодорожных путей необщего пользования (приемоотправочный парк ст. Круглое Поле)
Изм.	Колич.	Лист	№док.	Подпись	Дата		
Разраб.		Бурайкин			18.05.26	Этап №5	Стадия: П; Лист: 1; Листов: 4
Проверил		Сундеев			18.05.26		
Н. контр.		Грошев			18.05.26	Схема организации рельефа и план земляных масс М 1:500	ГРАДО ПРОЕКТ


Взам. инв. №


Подп. и дата

Инв. № подл.

Формат А4х4

Площадка размещения зданий необщего пользования №2

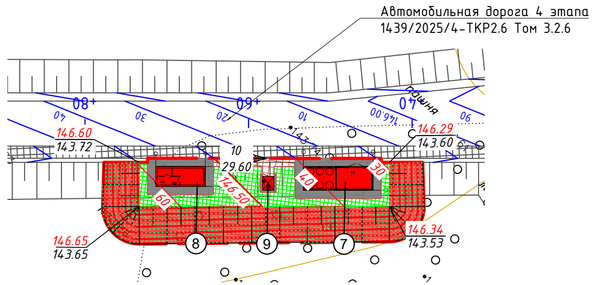

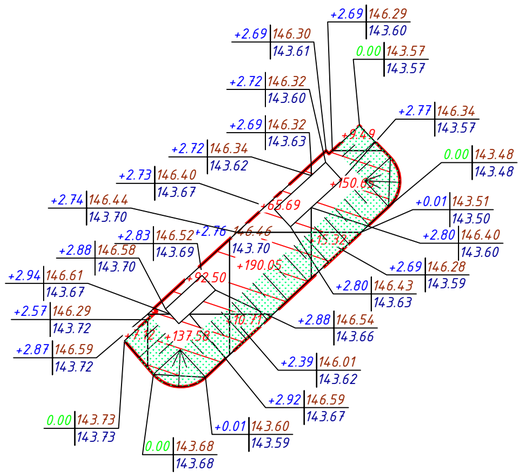

Итого, м³						Всего, м³	
	Насыпь	+7.12	+230.08	+266.45	+175.46		+679.11
	Выемка	–	–	–	–		–

Площадь картограммы – 338.89 м², в т.ч.:
насыпь – 338.89 м², выемка – 0.00 м²

1. Система высот Балтийская 1977 г.
2. Система координат местная.
3. Отметки и уклоноуказатели приведены по верху покрытия.

Экспликация зданий и сооружений

Номер на плане	Наименование	Примечание
7	Модульная компрессорная	Проектируемое
8	Модульный пункт обогрева	Проектируемое
9	Туалетный модуль 1.4x1.7	Проектируемое

Условные обозначения

	Граница проектирования благоустройства
	Проектируемое здание
	Тротуар из асфальтобетона
	Отмостка
	Газон
	Откос
	Бортовой камень БР100.20.8
	Бровка земляного полотна
	Проектная горизонталь
	Проектная горизонталь АД 4 этапа 1439/2025/4-ТКР2.6 Том 3.2.6
10 / 29.60	Направление уклона проектируемого рельефа
146.34 / 143.53	Отметка поверхности (проектная / существующая)

Ведомость объемов земляных масс

Наименование грунта	Количество, м³		Приме-чание
	Насыпь (+)	Выемка (–)	
1. Грунт планировки территории	680	–	
2. Вытесненный грунт, в т.ч. при устройстве:		234	
а) тротуара		5	
б) отмостки		15	
в) газона и откоса		214	
3. Поправка на уплотнение, k=0,1	68	–	
4. Всего пригодного грунта	748	234	
5. Недостаток пригодного грунта		514	
7. Плодородный грунт, всего:			
а) используемый для озеленения территории	214	–	
б) недостаток плодородного грунта		214	
8. Итого перерабатываемого грунта	962	962	

Условные обозначения



1. Система высот Балтийская 1977 г.
2. Система координат местная.
3. Картограмма разработана в программном комплексе Civil3d.
4. При расчете картограммы квадраты сетки приняты стороной равной 10 м.
5. Необходимость замены грунта под зданиями и сооружениями определена в марке КР.
6. Коэффициент уплотнения – не менее 0,95. Толщина каждого слоя 0,3–0,6 м (уточняется по результатам опытного уплотнения).
7. После возведения земляного полотна откосы необходимо доуплотнять планировщиками-уплотнителями.

Изм.	Кол.уч.	Лист	№док.	Подпись	Дата	1439/2025/5-ИЛО1-ГЧ.05			
						Инфраструктура индустриального парка «Этилен-600», Железнодорожная инфраструктура. Этап №5. Строительство железнодорожных путей необщего пользования (приемоотправочный парк ст. Круглое Поле)			
Разраб.		Бурайкин			18.05.26	Этап №5	Стадия	Лист	Листов
Проверил		Сундеев			18.05.26		П	2	4
Н. контр.		Грошев			18.05.26	Схема организации рельефа и план земляных масс М 1:500	ГРАДО ПРОЕКТ		


Взам. инв. №

Подп. и дата

Инв. № подл.

Формат А4х3

Площадка Водоподготовки

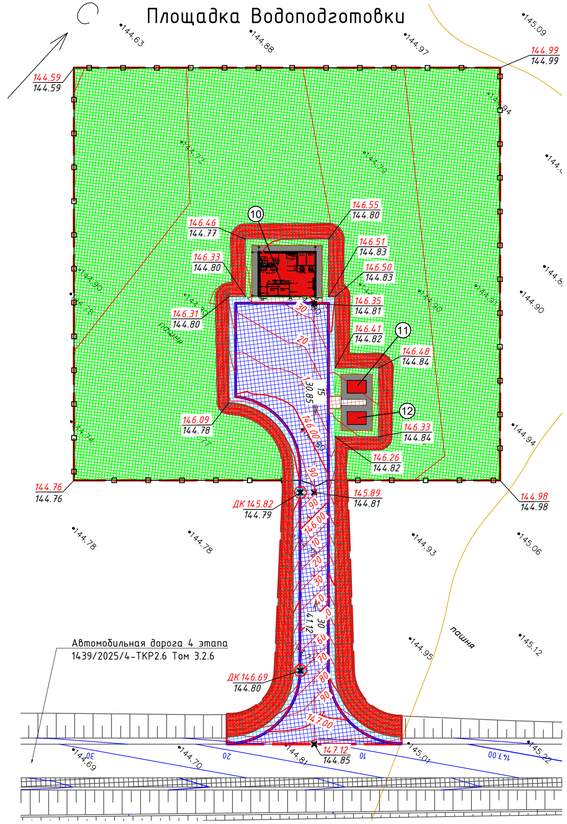

Экспликация зданий и сооружений

Номер на плане	Наименование	Примечание
10	Водоподготовка	Проектируемое
11, 12	Трансформаторная подстанция	Проектируемое


Условные обозначения

	Граница проектирования благоустройства
	Проектируемое здание
	Асфальтобетонный проезд
	Тротуар из асфальтобетонна
	Отмостка из асфальтобетонна
	Обочина
	Газон
	Откос
	Бортовой камень БР100.30.15
	Бортовой камень БР100.20.8
	Бровка земляного полотна
	Ось проезда
	Дождеприемный колодец
	Ограждение l=269,30 м
	Ворота распашные 4,5 м
	Проектная горизонталь
	Проектная горизонталь АД 4 этапа 1439/2025/4-ТКР2.6 Том 3.2.6
15 / 30.85	Направление уклона проектируемого рельефа
146.26 / 144.82	Отметка поверхности (проектная / существующая)
147.12 / 144.85	Точка перелома проектируемого рельефа (проектная / существующая)

Условные обозначения



1. Система высот Балтийская 1977 г.
2. Система координат местная.
3. Отметки и уклоноуказатели приведены по верху покрытия.

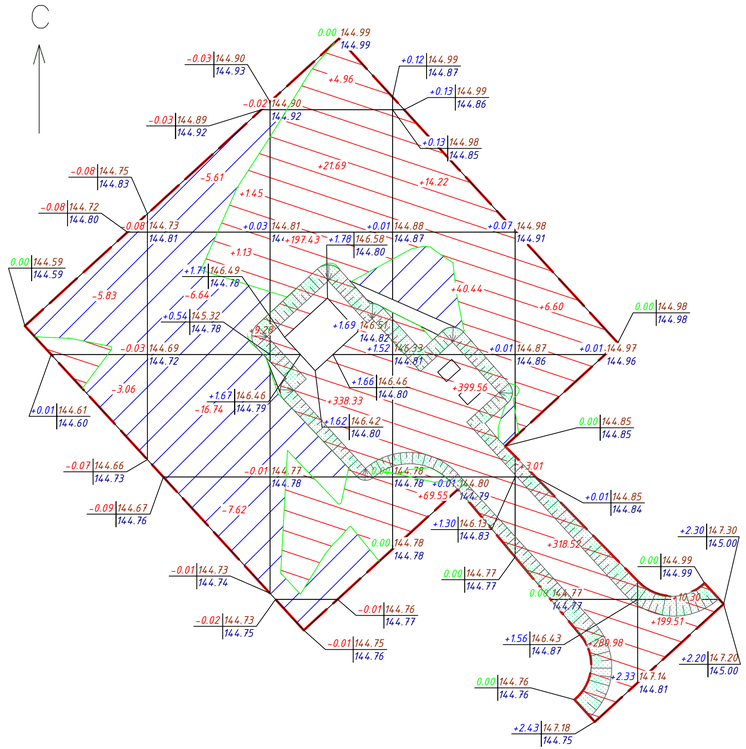

Ведомость объемов земляных масс

Наименование грунта	Количество, м³		Приме-чание
	Насыпь (+)	Выемка (–)	
1. Грунт планировки территории	1909	46	
2. Вытесненный грунт, в т.ч. при устройстве:		1332	
а) проезда		575	
б) тротуара		56	
в) отмостки		20	
г) газона и откоса		681	
3. Поправка на уплотнение, k=0,1	191	–	
4. Всего пригодного грунта	2100	1378	
5. Недостаток пригодного грунта		722	
7. Плодородный грунт, всего:			
а) используемый для озеленения территории	681	–	
б) недостаток плодородного грунта		681	
8. Итого перерабатываемого грунта	2781	2781	

Всего/Итого, м³							
	Насыпь	–	+11.86	+562.41	+523.77	+609.11	+209.81
	Выемка	-8.89	-36.61	–	–	–	–
	Насыпь	+1916.96	Площадь картограммы – 4337.80 м², в т.ч.: насыпь – 2959.10 м², выемка – 1378.70 м²				
	Выемка	-45.50					

1. Система высот Балтийская 1977 г.
2. Система координат местная.
3. Картограмма разработана в программном комплексе Civil 3d.
4. При расчете картограммы квадраты сетки приняты стороной равной 20 м.
5. Необходимость замены грунта под зданиями и сооружениями определена в марке КР.
6. Коэффициент уплотнения – не менее 0,95. Толщина каждого слоя 0,3–0,6 м (уплочняется по результатам опытного уплотнения).
7. После возведения земляного полотна откосы необходимо доуплотнять планировщиками-уплотнителями.

Изм.	Колич.	Лист	№док.	Подпись	Дата
Разраб.		Бураикин			18.05.26
Проверил		Сундеев			18.05.26
Н. контр.		Грошев			18.05.26

1439/2025/5-ИЛО1-ГЧ.05

Инфраструктура индустриального парка «Этилен-600», Железнодорожная инфраструктура. Этап №5. Строительство железнодорожных путей необщего пользования (приемоотправочный парк ст. Круглое Поле)

Этап №5

Стадия	Лист	Листов
П	3	4

Схема организации рельефа и план земляных масс
М 1:500

ГРАДО ПРОЕКТ


Взам. инв. №


Подп. и дата

Инв. № подл.

Формат А4х4

Площадка локальных очистных сооружений

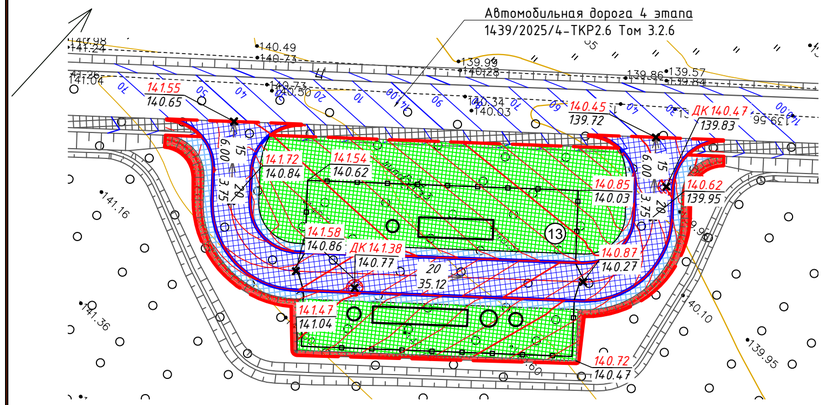

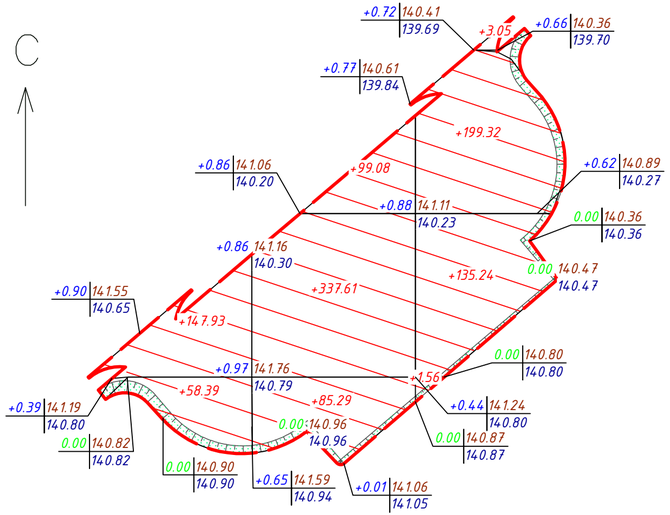

Итого, м³					Всего, м³	
	Насыпь	+206.32	+521.98	+339.17		+1067.47
	Выемка	-	-	-		-


Площадь картограммы - 1453.29 м², в т.ч.:
насыпь - 1453.29 м², выемка - 0.00 м²

Условные обозначения

	Граница проектирования благоустройства
	Проектируемые сооружения
	Асфальтобетонный проезд
	Отмостка из асфальтобетонна
	Обочина
	Газон
	Откос
	Бортовой камень БР100.30.15
	Бровка земляного полотна
	Ось проезда
	Дождеприемный колодец
	Ограждение l=97,90 м
	Ворота распашные 4,5 м
	Проектная горизонталь
	Проектная горизонталь АД 4 этапа 1439/2025/4-ТКР2.6 Том 3.2.6
20 / 35.12	Направление уклона проектируемого рельефа
140.87 / 140.27	Отметка поверхности (проектная / существующая)
140.62 / 139.95	Точка перелома проектируемого рельефа (проектная / существующая)

1. Система высот Балтийская 1977 г.
2. Система координат местная.
3. Отметки и уклоноуказатели приведены по верху покрытия.

Условные обозначения

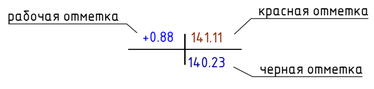

+99.08 Насыпь

Экспликация зданий и сооружений

Номер на плане	Наименование	Примечание
13	Локальные очистные сооружения (ЛОС)	Проектируемое

Ведомость объемов земляных масс

Наименование грунта	Количество, м³		Приме-чание
	Насыпь (+)	Выемка (-)	
1. Грунт планировки территории	1068	-	
2. Вытесненный грунт, в т.ч. при устройстве:		408	
а) проезда		252	
г) газона и откоса		156	
3. Поправка на уплотнение, k=0,1	107	-	
4. Всего пригодного грунта	1175	408	
5. Недостаток пригодного грунта		767	
7. Плодородный грунт, всего:			
а) используемый для озеленения территории	156	-	
б) недостаток плодородного грунта		156	
8. Итого перерабатываемого грунта	1331	1331	

1. Система высот Балтийская 1977 г.
2. Система координат местная.
3. Картограмма разработана в программном комплексе Civil3d.
4. При расчете картограммы квадраты сетки приняты стороной равной 20 м.
5. Необходимость замены грунта под зданиями и сооружениями определена в марке КР.
6. Коэффициент уплотнения - не менее 0,95. Толщина каждого слоя 0,3-0,6 м (уточняется по результатам опытного уплотнения).
7. После возведения земляного полотна откосы необходимо доуплотнять планировщиками-уплотнителями.

Изм.	Кол.уч	Лист	№док.	Подпись	Дата	1439/2025/5-ИЛО1-ГЧ.05			
						Инфраструктура индустриального парка «Этилен-600», Железнодорожная инфраструктура. Этап №5. Строительство железнодорожных путей необщего пользования (приемоотправочный парк ст. Круглое Поле)			
Разраб.		Бурайкин			18.05.26	Этап №5	Стадия	Лист	Листов
Проверил		Сундеев			18.05.26		П	4	4
Н. контр.		Грошев			18.05.26	Схема организации рельефа и план земляных масс М 1:500	ГРАДО ПРОЕКТ		

Взам. инв. №

Подп. и дата

Инв. № подл.

Формат А4х3