ОБЩЕСТВО С ОГРАНИЧЕННОЙ ОТВЕТСТВЕННОСТЬЮ

alabuga DEVELOPMENT

№ СРО-П-114-14012010

Заказчик – АО «ОЭЗ ППТ «Алабуга»

Инфраструктура индустриального парка «Этилен-600», Железнодорожная инфраструктура.

Этап №4. Строительство железнодорожных путей общего пользования (приемоотправочный парк ст. Круглое Поле)

РАБОЧАЯ ДОКУМЕНТАЦИЯ

Генеральный план. Здания обслуживания железнодорожной инфраструктуры общего пользования Дополнительного Парка

1439/2025/4-ГП.ДП

2026 г.

ОБЩЕСТВО С ОГРАНИЧЕННОЙ ОТВЕТСТВЕННОСТЬЮ

№ СРО-П-114-14012010

Заказчик – АО «ОЭЗ ППТ «Алабуга»

Инфраструктура индустриального парка «Этилен-600», Железнодорожная инфраструктура.

Этап №4. Строительство железнодорожных путей общего пользования (приемоотправочный парк ст. Круглое Поле)

РАБОЧАЯ ДОКУМЕНТАЦИЯ

Генеральный план. Здания обслуживания железнодорожной инфраструктуры общего пользования Дополнительного Парка

1439/2025/4-ГП.ДП

Главный инженер Мезенцев Д.В.

2026 г.



Общество с ограниченной ответственностью
«ГрадоПроект»

Инфраструктура индустриального парка «Этилен-600», Железнодорожная инфраструктура.

Этап №4. Строительство железнодорожных путей общего пользования (приемоотправочный парк ст. Круглое Поле)

РАБОЧАЯ ДОКУМЕНТАЦИЯ

Генеральный план.
Здания обслуживания железнодорожной инфраструктуры общего пользования Дополнительного Парка

1439/2025/4-ГП.ДП

Директор **И. А. Трубицин**

Главный инженер проекта **В. В. Сундеев**

2026 г.

Ведомость ссылочных и прилагаемых документов

Обозначение	Наименование	Примечание
	Ссылочные документы	
ГОСТ 32824-2014	Дороги автомобильные общего пользования. Песок природный	
ГОСТ 58406.2-2020	Дороги автомобильные общего пользования. Смеси горячие асфальтобетонные и асфальтобетон	
ГОСТ 32703-2014	Дороги автомобильные общего пользования. Щебень и гравий из плотных горных пород для строительных работ	
ГОСТ 32961-2014	Дороги автомобильные общего пользования. Камни бортовые	
ГОСТ 6665-91	Камни бетонные и железобетонные бортовые	
ГОСТ 32945-2014	Дороги автомобильные общего пользования. Знаки дорожные	

Ведомость рабочих чертежей основного комплекта

Лист	Наименование	Примечание
1	Общие данные	
2.1	Разбивочный план (1:500). Площадка в районе четной горловины проектируемого Парка	
2.2	Разбивочный план (1:500). Площадка в районе нечетной горловины проектируемого Парка	
3.1	План организации рельефа (1:500). Площадка в районе четной горловины проектируемого Парка	
3.2	План организации рельефа (1:500). Площадка в районе нечетной горловины проектируемого Парка	
4.1	План земляных масс (1:500). Площадка в районе четной горловины проектируемого Парка	
4.2	План земляных масс (1:500). Площадка в районе нечетной горловины проектируемого Парка	
5.1	Сводный план сетей инженерно-технического обеспечения (1:500). Площадка в районе четной горловины проектируемого Парка	
5.2	Сводный план сетей инженерно-технического обеспечения (1:500). Площадка в районе нечетной горловины проектируемого Парка	
6.1	План благоустройства (1:500). Площадка в районе четной горловины проектируемого Парка	
6.2	План благоустройства (1:500). Площадка в районе нечетной горловины проектируемого Парка	

Взам. инв. N°

Подп. и дата

Инв. N° подл.

Общие указания

1 Рабочая документация разработана на основании задания на разработку проектно-сметной документации «Инфраструктура индустриального парка «Этилен-600», Железнодорожная инфраструктура. Этап №4. Строительство железнодорожных путей общего пользования (приемоотправочный парк ст. Круглое Поле)

2 Рабочие чертежи разработаны в соответствии действующими нормами, правилами и стандартами, действующими на территории Российской Федерации:

- СП 18.13330.2019 "Генеральные планы промышленных предприятий. Актуализированная редакция СНиП II-89-80*";
- СП 4.131.30.2013 «Системы противопожарной защиты. Ограничение распространения пожара на объектах защиты. Требования к объемно-планировочным и конструктивным решениям»;
- СП 34.13330.2021 «Автомобильные дороги»;
- СП 34.13330.2012 «Промышленный транспорт»;
- ГОСТ 21.508-2020 «СПДС. Правила выполнения рабочей документации генеральных планов предприятий, сооружений и жилищно-гражданских объектов»;
- ГОСТ Р 21.101-2020 «Основные требования к проектной и рабочей документации»;
- СанПин 2.2.1/2.1.1.1200-03 «Санитарно-защитные зоны и санитарная классификация предприятий, сооружений и иных объектов»;
- ПУЭ «Правила устройства электроустановок. Издание 7».

3 В качестве подосновы для выполнения чертежей использована топографическая съемка участка, выполненная ООО "Геодезия Кадастр Изыскания" в 2026 г.

4 Система высот Балтийская 1977 г.

5 Система координат МСК-16.


6 Основные виды работ, для которых необходимо составлять акты на скрытые работы:

- снятие растительного слоя;
- укладка геотекстиля и геосетки;
- послойная отсыпка, послойное уплотнение, планировка земляного полотна и корыта;
- уплотнение и планировка обочин и откосов, засев трав при укреплении;
- засыпка коммуникаций и сооружений;
- сооружение каждого конструктивного слоя основания;
- сооружение каждого конструктивного слоя покрытия.

Изм.	Кол.уч	Лист	N°док.	Подпись	Дата	1439/2025/4-ГП.ДП-1			
						Инфраструктура индустриального парка «Этилен-600», Железнодорожная инфраструктура. Этап №4. Строительство железнодорожных путей общего пользования (приемоотправочный парк ст. Круглое Поле)			
Разраб.		Бурайкин			09.26	Этап №4	Стадия	Лист	Листов
Проверил		Сундеев			09.26		Р	1	11
Н. контр.		Грошев			09.26	Общие данные	ГРАДО ПРОЕКТ		

Формат А3

Площадка в районе четной горловины проектируемого Парка

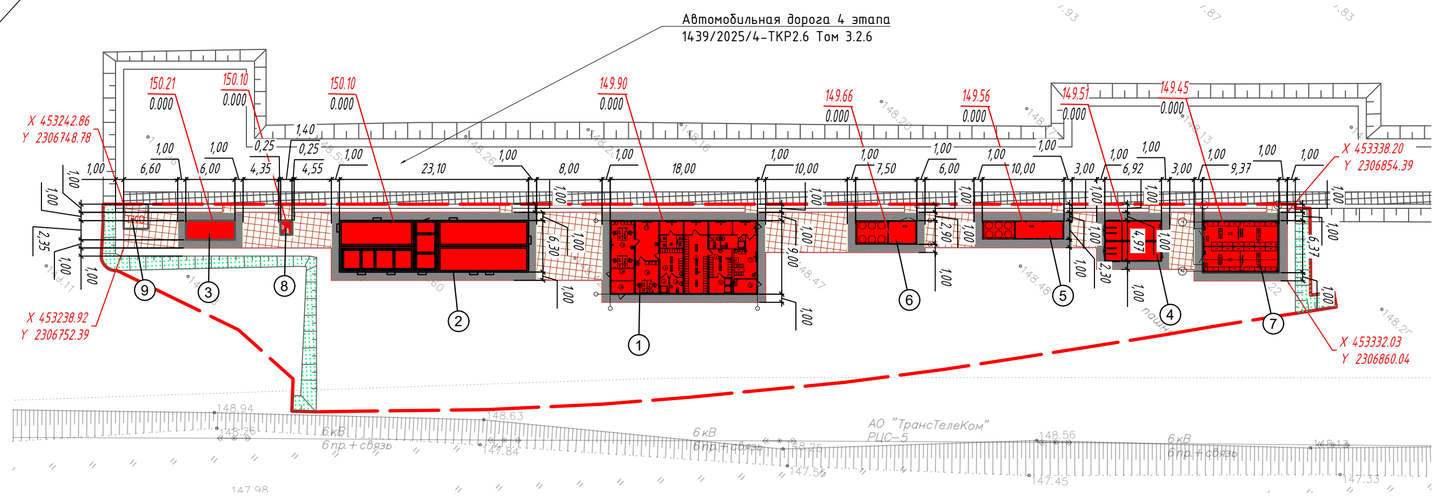


Экспликация зданий и сооружений

Номер на плане	Наименование	Примечание
1	Административно-бытовой модуль	Проектируемое
2	Мобильный комплекс железнодорожной Автоматики, телемеханики и связи (МК АТС)	Проектируемое
3	Модульный дизель-генераторный агрегат (ДГА)	Проектируемое
4	КТП	Проектируемое
5	Модуль автоматизированной системы диагностики тормозов (АСДТ)	Проектируемое
6	Модульная компрессорная	Проектируемое
7	Кладовая для хранения путевого инструмента и материалов ВСП	Проектируемое
8	Туалетный модуль 1.4х1.7	Проектируемое
9	ТКО	Проектируемое

Условные обозначения


	Граница проектирования благоустройства
	Проектируемое здание
	Откос
	Бортовой камень БР100.20.8
	Бровка земляного полотна

Тип 1. Тротуар

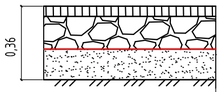


Покрытие: асфальтобетон А5Вл по ГОСТ 58406.2-2020 на битуме PG 64-22 вяжущее по ГОСТ 58400.1-2019	-0,05м
Слой основания: щебень М-600 по ГОСТ 32703-2014 фр. 16-31.5мм	-0,16м
Разделяющая прослойка: нетканый геотекстиль предельная прочность не менее 5кН/м, ГОСТ Р 56419-2015	
Дополнительный слой основания: песок очень мелкий по ГОСТ 32824-2014 Кф>1 м/сут	-0,15м

Тип 2. Отмостка зданий

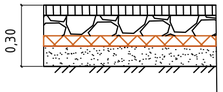


Покрытие: асфальтобетон А5Вл по ГОСТ 58406.2-2020 на битуме PG 64-22 вяжущее по ГОСТ 58400.1-2019	-0,05м
Слой основания: щебень М-600 по ГОСТ 32703-2014 фр. 16-31.5мм	-0,10м
Гидроизоляция	
Утеплитель ЭППС	-0,05м
Дополнительный слой основания: песок очень мелкий по ГОСТ 32824-2014 Кф>1 м/сут	-0,10м


Установка бортового камня БР100.20.8 в сопряжении отмостки и газона

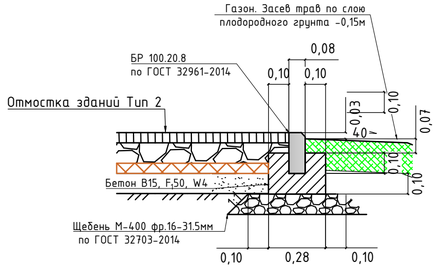

Установка бортового камня БР100.20.8 в сопряжении тротуара и газона

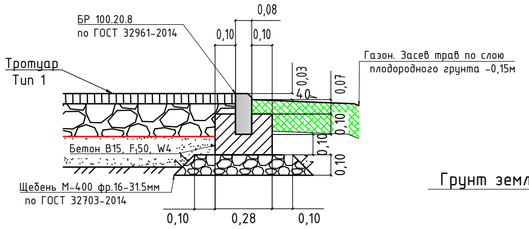

Укрепление откосов

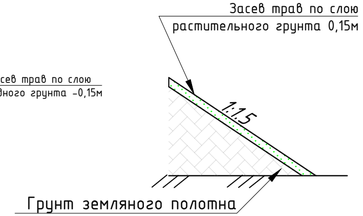

1. Система высот Балтийская 1977 г.
2. Система координат местная.
3. Размеры даны в метрах

Изм.	Кол.уч.	Лист	№док.	Подпись	Дата
Разраб.		Бурайкин			09.26
Проверил		Сундеев			09.26
Н. контр.		Грошев			09.26

1439/2025/4-ГП.ДП-2.1

Инфраструктура индустриального парка «Этилен-600», Железнодорожная инфраструктура. Этап №4. Строительство железнодорожных путей общего пользования (приемоотправочный парк ст. Круглое Поле)

Этап №4

Стадия	Лист	Листов
Р	2.1	

Разбивочный план М 1:500
Площадка в районе четной горловины проектируемого Парка

ГРАДО ПРОЕКТ


Взам. инв. №

Подп. и дата

Инв. № подл.

Формат А4х3

Площадка в районе нечетной горловины проектируемого Парка

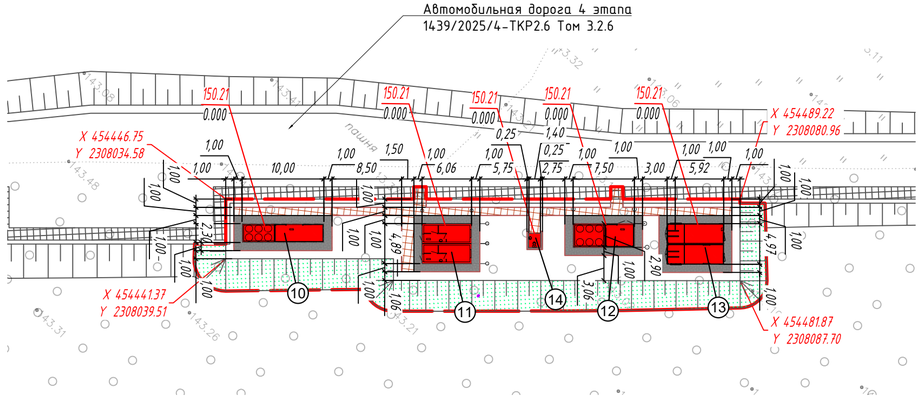


Экспликация зданий и сооружений

Номер на плане	Наименование	Примечание
10	Модуль автоматизированной системы диагностики тормозов (АСДТ)	Проектируемое
11	Модульный пункт обогрева	Проектируемое
12	Модульная компрессорная	Проектируемое
13	КТП	Проектируемое
14	Туалетный модуль 1,4х1,7	Проектируемое

Условные обозначения


	Граница проектирования благоустройства
	Проектируемое здание
	Откос
	Бортовой камень БР100.20.8
	Бровка земляного полотна

Тип 1. Тротуар

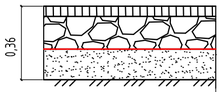


Покрытие: асфальтобетон А5Вл по ГОСТ 58406.2-2020 на битуме PG 64-22 вяжущее по ГОСТ 58400.1-2019	-0,05м
Слой основания: щебень М-600 по ГОСТ 32703-2014 фр. 16-31.5мм	-0,16м
Разделяющая прослойка: нетканый геотекстиль предельная прочность не менее 5кН/м, ГОСТ Р 56419-2015	
Дополнительный слой основания: песок очень мелкий по ГОСТ 32824-2014 Кф>1 м/сут	-0,15м

Тип 2. Отмостка зданий

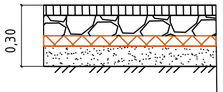


Покрытие: асфальтобетон А5Вл по ГОСТ 58406.2-2020 на битуме PG 64-22 вяжущее по ГОСТ 58400.1-2019	-0,05м
Слой основания: щебень М-600 по ГОСТ 32703-2014 фр. 16-31.5мм	-0,10м
Гидроизоляция	
Утеплитель ЭППС	-0,05м
Дополнительный слой основания: песок очень мелкий по ГОСТ 32824-2014 Кф>1 м/сут	-0,10м


Установка бортового камня БР100.20.8 в сопряжении отмостки и газона

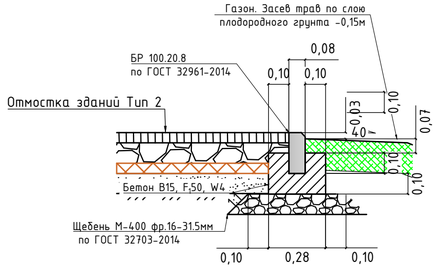

Установка бортового камня БР100.20.8 в сопряжении тротуара и газона

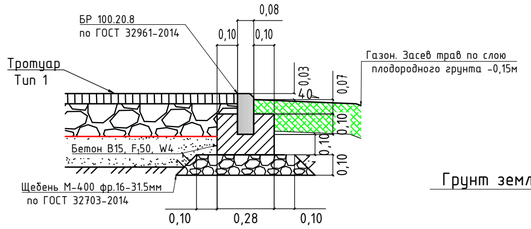

Укрепление откосов

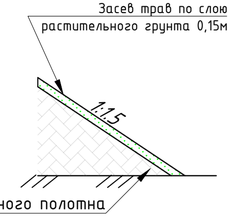

1. Система высот Балтийская 1977 г.
2. Система координат местная.
3. Размеры даны в метрах

Изм.	Кол.уч.	Лист	№док.	Подпись	Дата	1439/2025/4-ГП.ДП-2.2			
						Инфраструктура индустриального парка «Этилен-600», Железнодорожная инфраструктура. Этап №4. Строительство железнодорожных путей общего пользования (приемоотправочный парк ст. Круглое Поле)			
Разраб.		Бурайкин			09.26	Этап №4	Стадия	Лист	Листов
Проверил		Сундеев			09.26		Р	2.2	
Н. контр.		Грошев			09.26	Разбивочный план М 1:500 Площадка в районе нечетной горловины проектируемого Парка	ГРАДО ПРОЕКТ		


Взам. инв. №

Подп. и дата

Инв. № подл.

Формат А4х3

Площадка в районе четной горловины проектируемого Парка

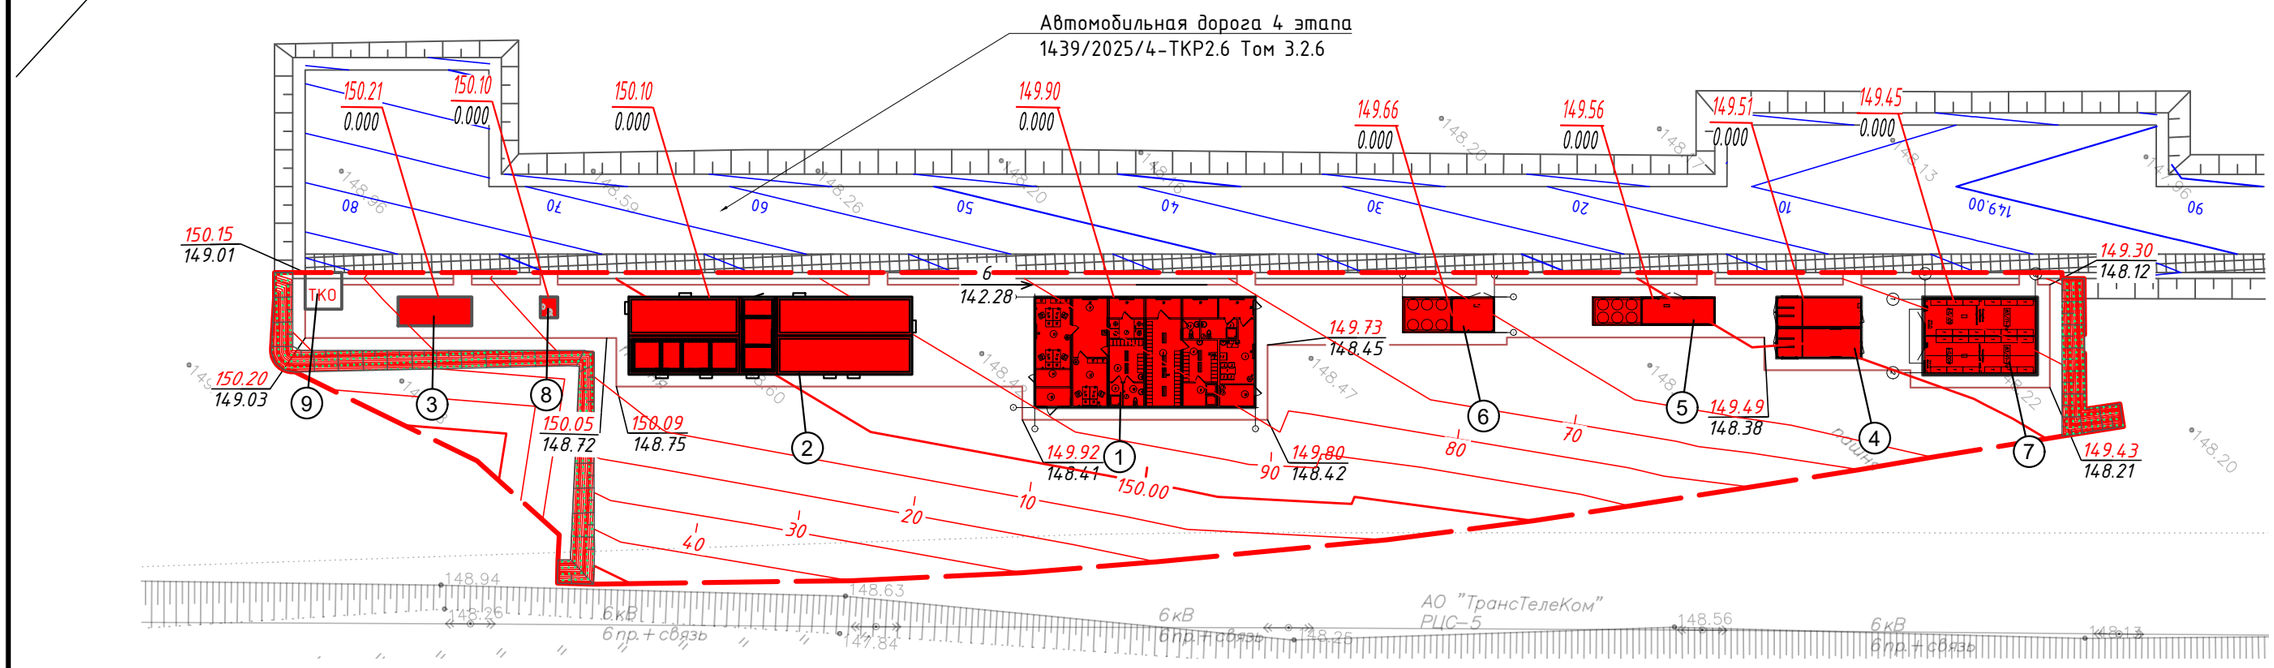

Экспликация зданий и сооружений

Номер на плане	Наименование	Примечание
1	Административно-бытовой модуль	Проектируемое
2	Мобильный комплекс железнодорожной Автоматики, телемеханики и связи (МК АТС)	Проектируемое
3	Модульный дизель-генераторный агрегат (ДГА)	Проектируемое
4	КТП	Проектируемое
5	Модуль автоматизированной системы диагностики тормозов (АСДТ)	Проектируемое
6	Модульная компрессорная	Проектируемое
7	Кладовая для хранения путевого инструмента и материалов ВСП	Проектируемое
8	Туалетный модуль 1.4х1.7	Проектируемое
9	ТКО	Проектируемое

1. Система высот Балтийская 1977 г.
2. Система координат местная.
3. Отметки и уклоноуказатели приведены по верху покрытия.

Условные обозначения


	Граница проектирования благоустройства
	Проектируемое здание
	Откос
	Бортовой камень БР100.20.8
	Бровка земляного полотна
	Проектная горизонталь
	Проектная горизонталь АД 4 этапа 1439/2025/4-ТКР2.6 Том 3.2.6
6 / 142.78	Направление уклона проектируемого рельефа
149.43 / 148.21	Отметка поверхности (проектная / существующая)

Изм.	Кол.уч	Лист	N°док.	Подпись	Дата	1439/2025/4-ГП.ДП-3.1			
						Инфраструктура индустриального парка «Этилен-600», Железнодорожная инфраструктура. Этап №4. Строительство железнодорожных путей общего пользования (приемоотправочный парк ст. Круглое Поле)			
Разраб.		Бурайкин			09.26	Этап №4	Стадия	Лист	Листов
Проверил		Сундеев			09.26		Р	3.1	
Н. контр.		Грошев			09.26	План организации рельефа М 1:500 Площадка в районе четной горловины проектируемого Парка	ГРАДО ПРОЕКТ		

Взам. инв. N° | Подп. и дата | Инв. N° подл.

Формат А3

Площадка в районе нечетной горловины проектируемого Парка

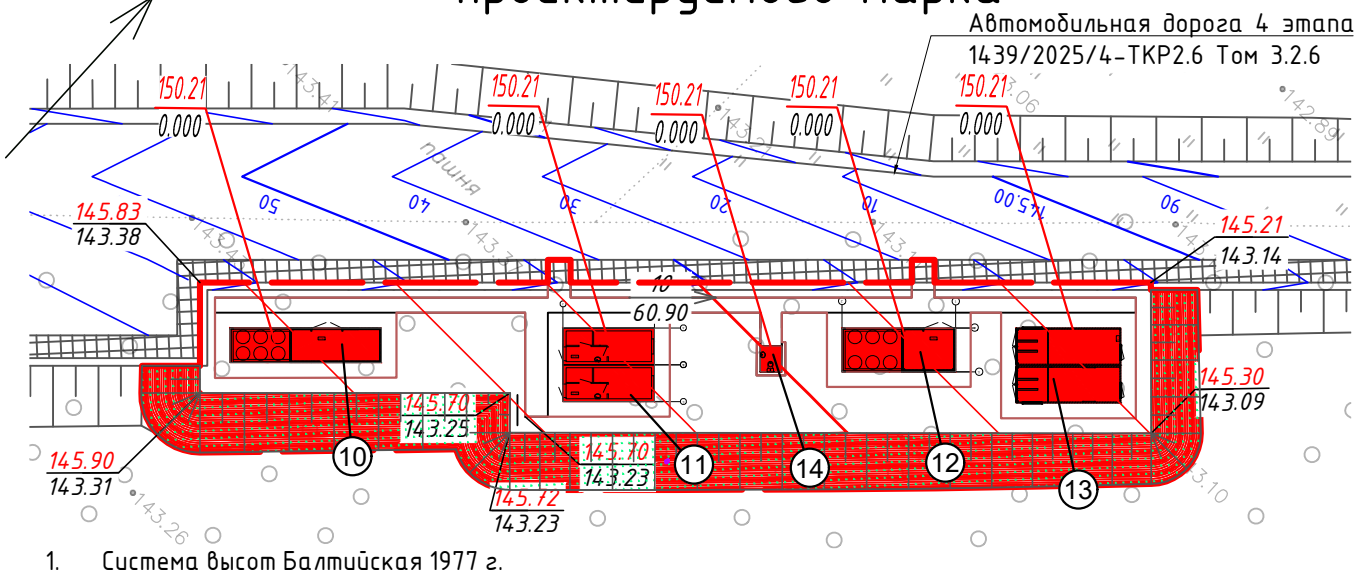

1. Система высот Балтийская 1977 г.
2. Система координат местная.
3. Отметки и уклоноуказатели приведены по верху покрытия.

Экспликация зданий и сооружений

Номер на плане	Наименование	Примечание
10	Модуль автоматизированной системы диагностики тормозов (АСДТ)	Проектируемое
11	Модульный пункт обогрева	Проектируемое
12	Модульная компрессорная	Проектируемое
13	КТП	Проектируемое
14	Туалетный модуль 1,4х1,7	Проектируемое

Условные обозначения

	Граница проектирования благоустройства
	Проектируемое здание
	Откос
	Бортовой камень БР100.20.8
	Бровка земляного полотна
	Проектная горизонталь
	Проектная горизонталь АД 4 этапа 1439/2025/4-ТКР2.6 Том 3.2.6
10 / 60.90	Направление уклона проектируемого рельефа
145.30 / 143.09	Отметка поверхности (проектная / существующая)

Взам. инв. N°

Подп. и дата

Инв. N° подл.

Изм.	Кол.уч	Лист	N°док.	Подпись	Дата
Разраб.		Бурайкин			09.26
Проверил		Сундеев			09.26
Н. контр.		Грошев			09.26

1439/2025/4-ГП.ДП-3.2

Инфраструктура индустриального парка «Этилен-600», Железнодорожная инфраструктура. Этап №4. Строительство железнодорожных путей общего пользования (приемоотправочный парк ст. Круглое Поле)

Этап №4

Стадия	Лист	Листов
Р	3.2	


План организации рельефа М 1:500
Площадка в районе нечетной горловины проектируемого Парка

ГРАДО ПРОЕКТ

Формат А4

С

Площадка в районе четной горловины проектируемого Парка

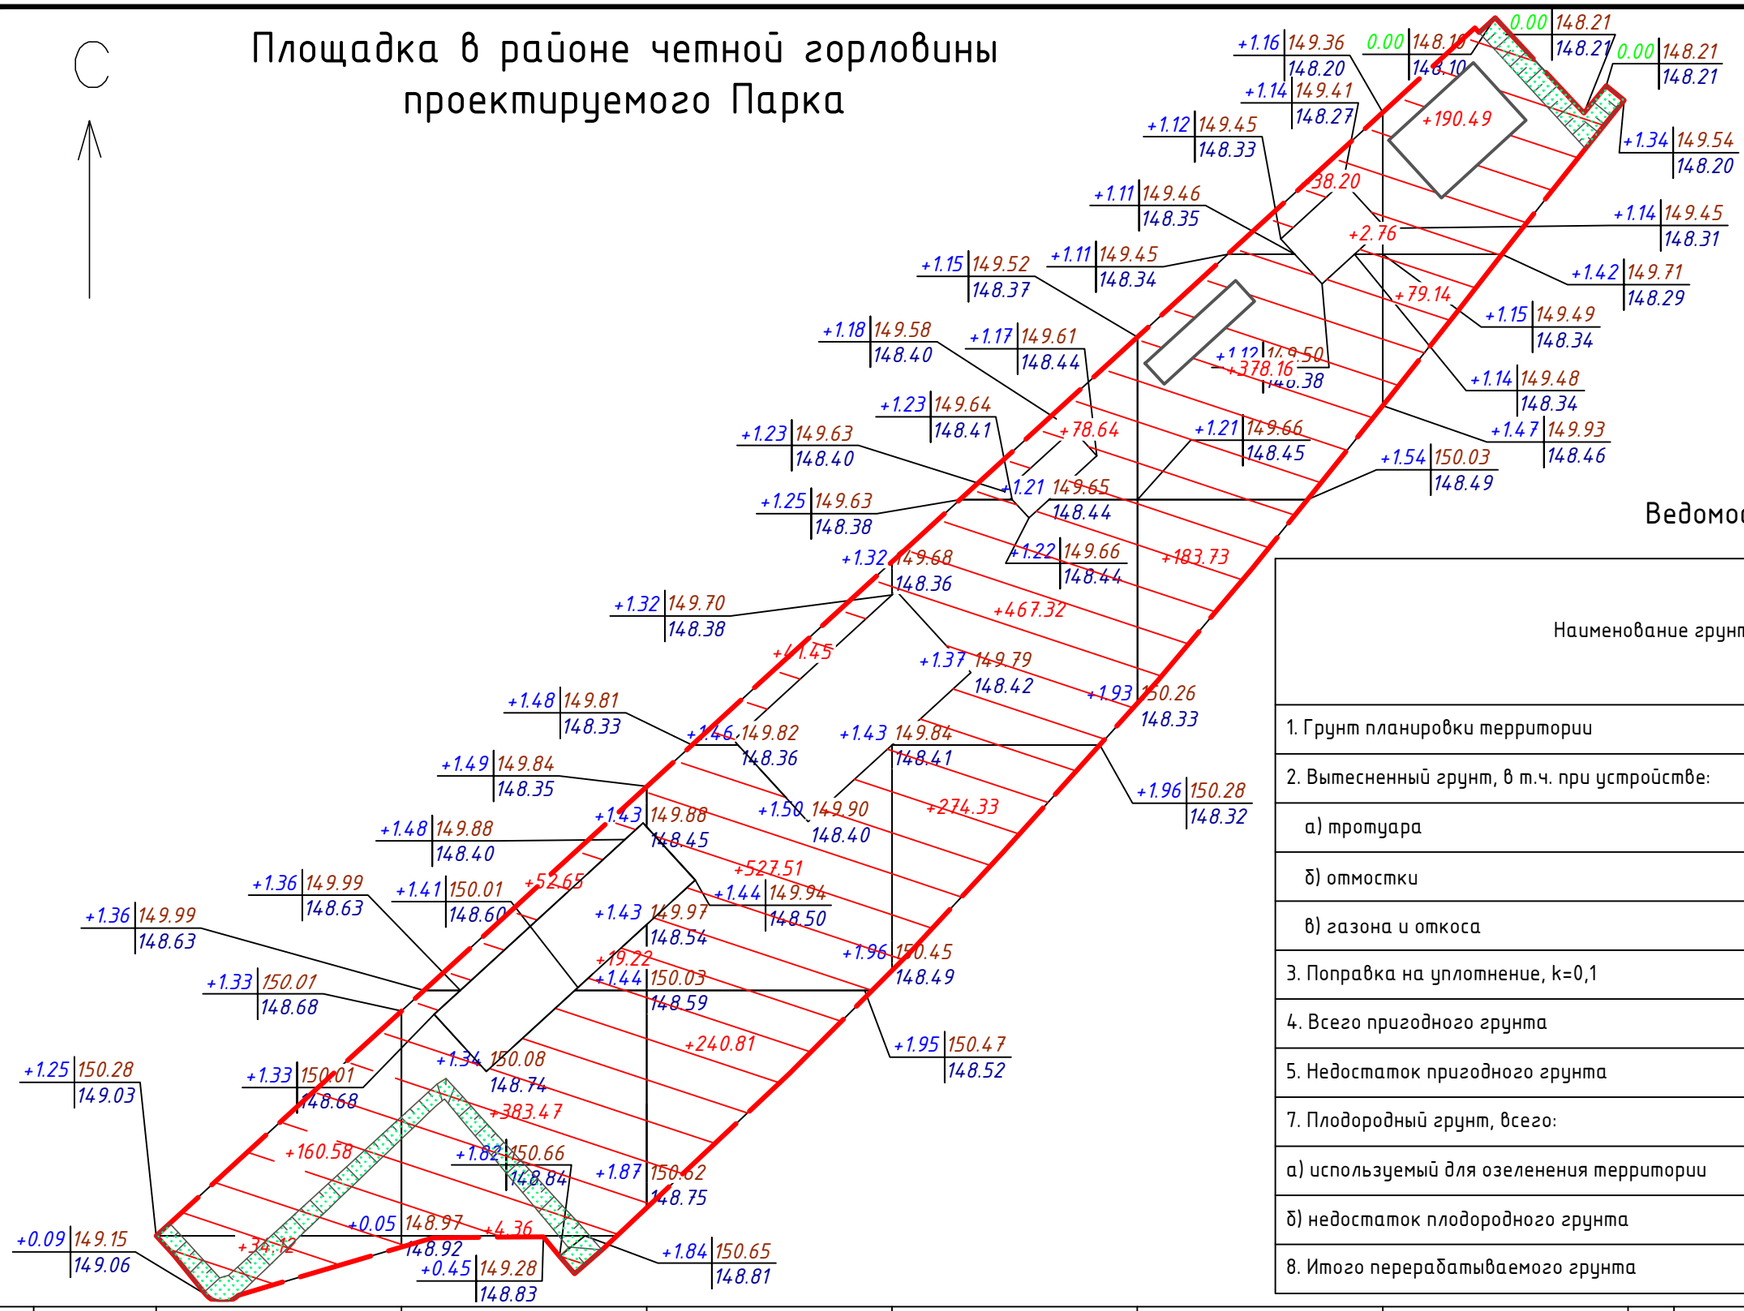

Условные обозначения

рабочая отметка — +1.33 | 150.01 — красная отметка

148.68 — черная отметка

+160.58 — Насыпь

Ведомость объемов земляных масс

Наименование грунта	Количество, м³		Приме-чание
	Насыпь (+)	Выемка (–)	
1. Грунт планировки территории	3157	–	
2. Вытесненный грунт, в т.ч. при устройстве:		468	
а) тротуара		94	
б) отмостки		78	
в) газона и откоса		296	
3. Поправка на уплотнение, k=0,1	316	–	
4. Всего пригодного грунта	3473	468	
5. Недостаток пригодного грунта		3005	
7. Плодородный грунт, всего:			
а) используемый для озеленения территории	296	–	
б) недостаток плодородного грунта		296	
8. Итого перерабатываемого грунта	3769	3769	

Итого, м³							Всего, м³	
	Насыпь	+194.70	+459.70	+809.77	+820.29	+602.85	+269.63	+3157
	Выемка	–	–	–	–	–	–	–

Площадь картограммы – 2491.44 м², в т.ч.:
насыпь – 2491.44 м², выемка – 0.00 м²

1. Система высот Балтийская 1977 г.
2. Система координат местная.
3. Картограмма разработана в программном комплексе Civil3d.
4. При расчете картограммы квадраты сетки приняты стороной равной 20 м.
5. Необходимость замены грунта под зданиями и сооружениями определена в марке КР.
6. Коэффициент уплотнения – не менее 0,95. Толщина каждого слоя 0,3–0,6 м (уточняется по результатам опытного уплотнения).
7. После возведения земляного полотна откосы необходимо доуплотнять планировщиками-уплотнителями.

Изм.	Кол.уч	Лист	N°док.	Подпись	Дата
Разраб.		Бурайкин			09.26
Проверил		Сундеев			09.26
Н. контр.		Грошев			09.26

1439/2025/4-ГП.ДП-4.1

Инфраструктура индустриального парка «Этилен-600», Железнодорожная инфраструктура. Этап №4. Строительство железнодорожных путей общего пользования (приемоотправочный парк ст. Круглое Поле)

Стадия	Лист	Листов
Р	4.1	

Этап №4


План земляных масс М 1:500
Площадка в районе четной горловины проектируемого Парка

ГРАДО ПРОЕКТ

Взам. инв. N° | Подп. и дата | Инв. N° подл.

Формат А3

Площадка в районе нечетной горловины проектируемого Парка

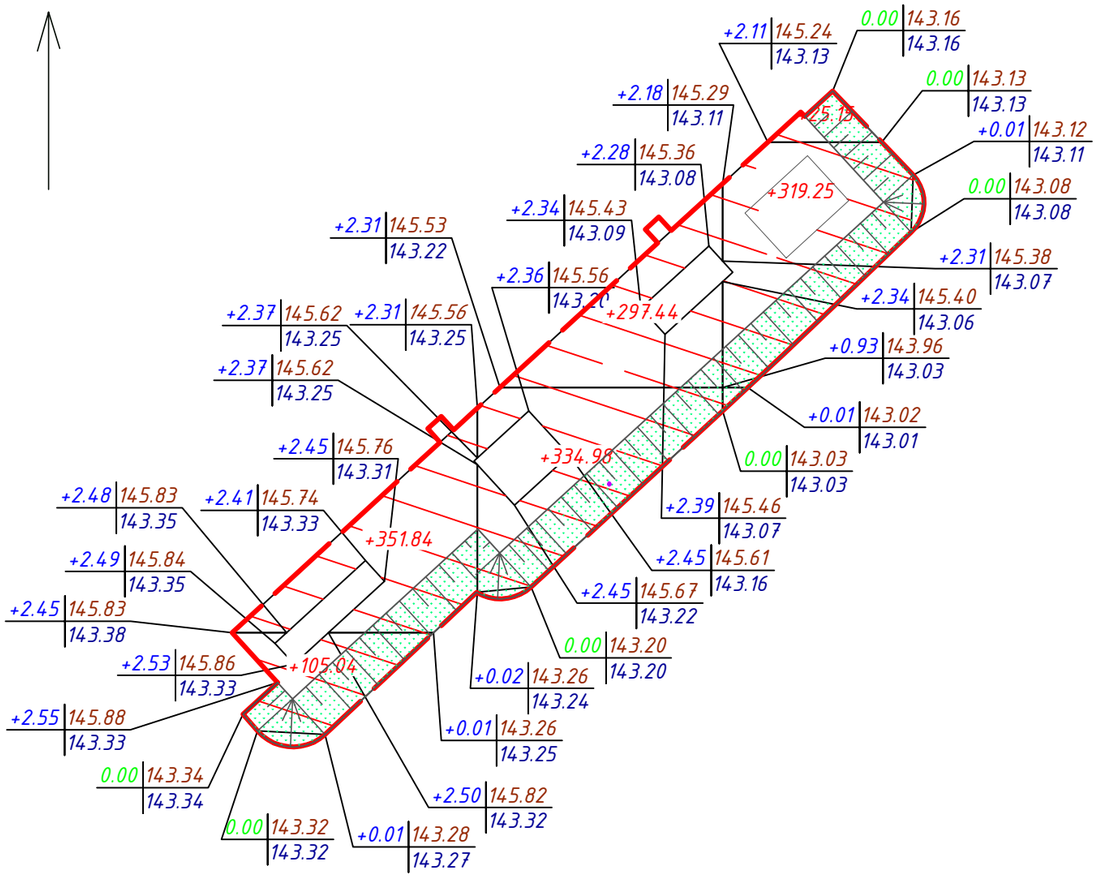

Итого, м³	*Насыпь*	*+456.88*	*+632.42*	*+344.40*	*Всего, м³*	*+1433.70*
	Выемка	-	-	-		-

Площадь картограммы – 751.53 м², в т.ч.:
насыпь – 751.53 м², выемка – 0.00 м²

Ведомость объемов земляных масс

Наименование грунта	Количество, м³		Примечание
	Насыпь (+)	Выемка (–)	
1. Грунт планировки территории	1434	–	
2. Вытесненный грунт, в т.ч. при устройстве:		149	
а) тротуара		30	
б) отмостки		32	
в) газона и откоса		87	
3. Поправка на уплотнение, k=0,1	144	–	
4. Всего пригодного грунта	1578	149	
5. Недостаток пригодного грунта		1429	
7. Плодородный грунт, всего:			
а) используемый для озеленения территории	87	–	
б) недостаток плодородного грунта		87	
8. Итого перерабатываемого грунта	1665	1665	

1. Система высот Балтийская 1977 г.
2. Система координат местная.
3. Картограмма разработана в программном комплексе Civil3d.
4. При расчете картограммы квадраты сетки приняты стороной равной 20 м.
5. Необходимость замены грунта под зданиями и сооружениями определена в марке КР.
6. Коэффициент уплотнения – не менее 0,95. Толщина каждого слоя 0,3–0,6 м (уточняется по результатам опытного уплотнения).
7. После возведения земляного полотна откосы необходимо доуплотнять планировщиками-уплотнителями.

Условные обозначения



Взам. инв. №
Подп. и дата
Инв. № подл.

Изм.	Кол.уч	Лист	N°док.	Подпись	Дата
Разраб.		Бурайкин			09.26
Проверил		Сундеев			09.26
Н. контр.		Грошев			09.26

1439/2025/4-ГП.ДП-4.2

Инфраструктура индустриального парка «Этилен-600», Железнодорожная инфраструктура. Этап №4. Строительство железнодорожных путей общего пользования (приемоотправочный парк ст. Круглое Поле)

Этап №4


Стадия	Лист	Листов
Р	4.2	

План земляных масс М 1:500
Площадка в районе нечетной горловины проектируемого Парка

ГРАДО ПРОЕКТ

Формат А3

Площадка в районе четной горловины проектируемого Парка

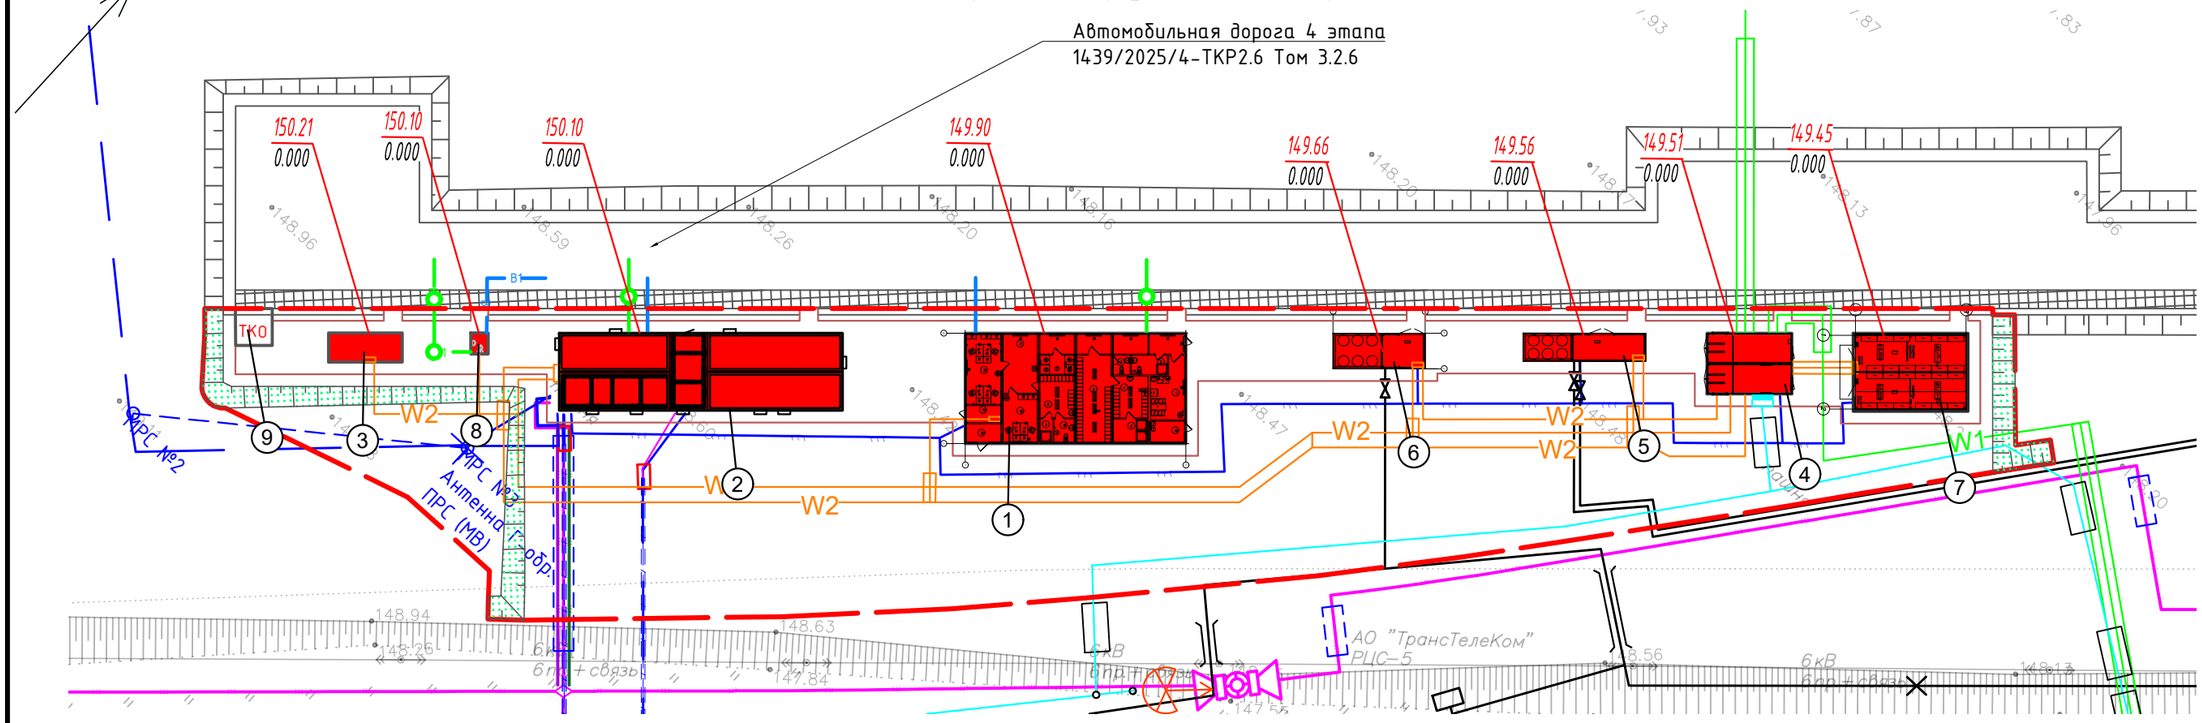

Экспликация зданий и сооружений

Номер на плане	Наименование	Примечание
1	Административно-бытовой модуль	Проектируемое
2	Мобильный комплекс железнодорожной Автоматики, телемеханики и связи (МК АТС)	Проектируемое
3	Модульный дизель-генераторный агрегат (ДГА)	Проектируемое
4	КТП	Проектируемое
5	Модуль автоматизированной системы диагностики тормозов (АСДТ)	Проектируемое
6	Модульная Компрессорная	Проектируемое
7	Кладовая для хранения путевого инструмента и материалов ВСП	Проектируемое
8	Туалетный модуль 1.4х1.7	Проектируемое
9	ТКО	Проектируемое

1. Система высот Балтийская 1977 г.
2. Система координат местная.

Условные обозначения


	Граница проектирования благоустройства
	Проектируемое здание
	Проектируемые сети связи
	Проектируемая сеть воздуховода
W1	Проектируемая кабельная линия электропередач
	Проектируемый водопровод
	Проектируемая бытовая канализация
	Проектируемая ливневая канализация
W1	Кабельная линия 6 кВ в траншее
W2	Кабельная линия 0,4 кВ в траншее

Изм.	Кол.уч	Лист	N°док.	Подпись	Дата	1439/2025/4-ГП.ДП-5.1			
						Инфраструктура индустриального парка «Этилен-600», Железнодорожная инфраструктура. Этап №4. Строительство железнодорожных путей общего пользования (приемоотправочный парк ст. Круглое Поле)			
Разраб.		Бурайкин			09.26	Этап №4	Стадия	Лист	Листов
Проверил		Сундеев			09.26		Р	5.1	
Н. контр.		Грошев			09.26	Сводный план сетей инженерно-технического обеспечения М 1:500. Площадка в районе четной горловины проектируемого Парка	ГРАДО ПРОЕКТ		

Взам. инв. N° | Подп. и дата | Инв. N° подл.

Формат А3

Площадка в районе нечетной горловины проектируемого Парка

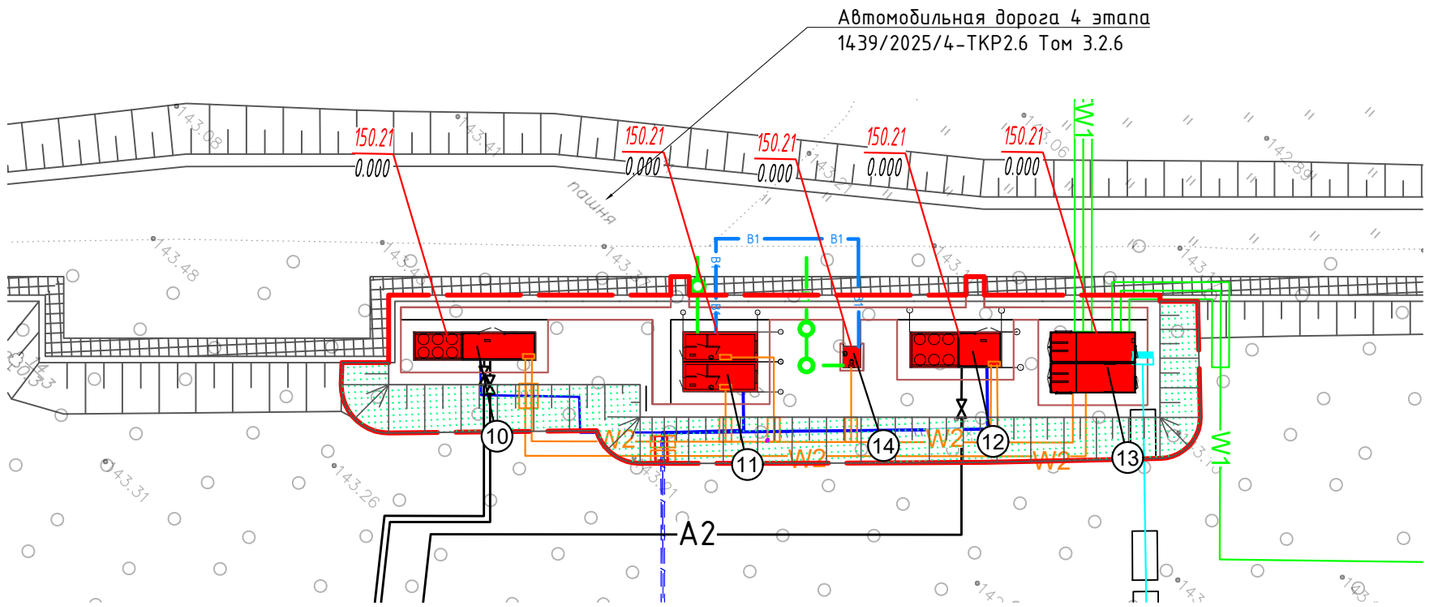

Экспликация зданий и сооружений

Номер на плане	Наименование	Примечание
10	Модуль автоматизированной системы диагностики тормозов (АСДТ)	Проектируемое
11	Модульный пункт обогрева	Проектируемое
12	Модульная компрессорная	Проектируемое
13	КТП	Проектируемое
14	Туалетный модуль 1,4х1,7	Проектируемое

Условные обозначения

	Граница проектирования благоустройства
	Проектируемое здание
	Проектируемые сети связи
	Проектируемая сеть воздуховода
W1	Проектируемая кабельная линия электропередач
	Проектируемый водопровод
	Проектируемая бытовая канализация
	Проектируемая ливневая канализация
W1	Кабельная линия 6 кВ в траншее
W2	Кабельная линия 0,4 кВ в траншее

1. Система высот Балтийская 1977 г.
2. Система координат местная.

Изм.	Кол.уч	Лист	N°док.	Подпись	Дата
Разраб.		Бурайкин			09.26
Проверил		Сундеев			09.26
Н. контр.		Грошев			09.26

1439/2025/4-ГП.ДП-5.2

Инфраструктура индустриального парка «Этилен-600», Железнодорожная инфраструктура. Этап №4. Строительство железнодорожных путей общего пользования (приемоотправочный парк ст. Круглое Поле)

Этап №4

Стадия	Лист	Листов
Р	5.2	

Сводный план сетей инженерно-технического обеспечения М 1:500. Площадка в районе нечетной горловины проектируемого Парка

ГРАДО ПРОЕКТ


Формат А3

Взам. инв. N°


Подп. и дата

Инв. N° подл.


Площадка в районе четной горловины проектируемого Парка

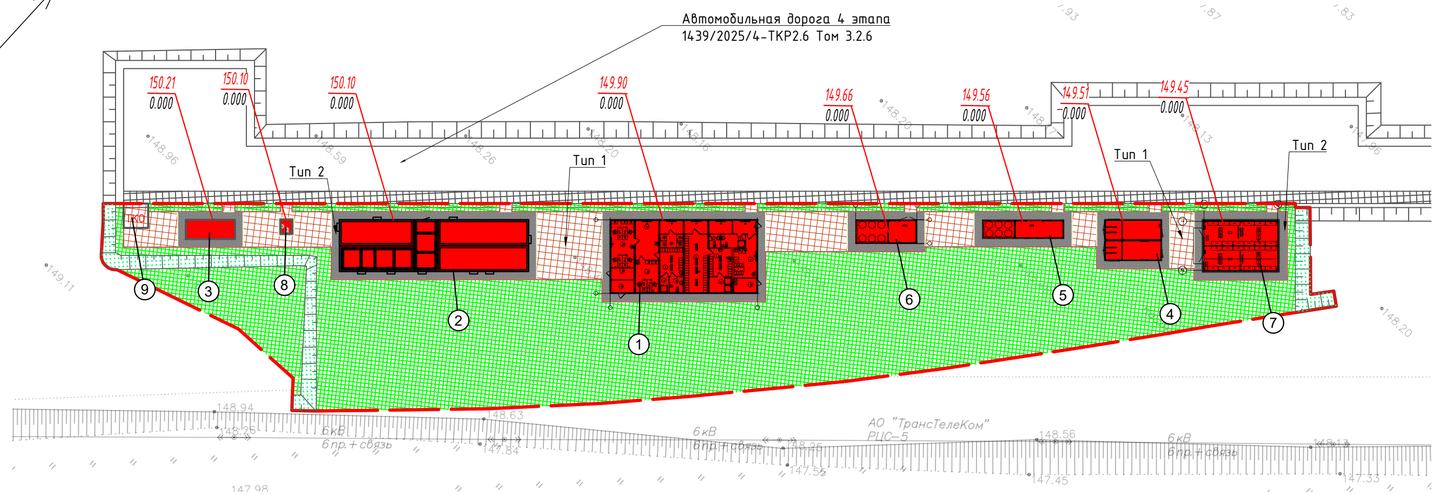

Установка бортового камня БР100.20.8 в сопряжении тротуара и газона

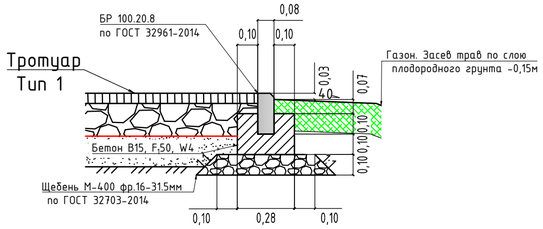

Установка бортового камня БР100.20.8 в сопряжении отмостки и газона

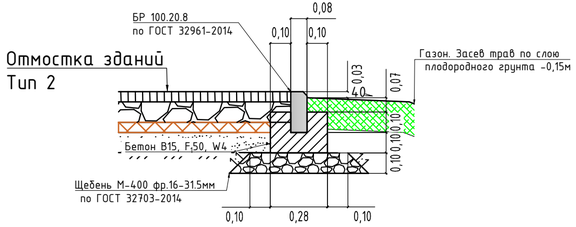

Ведомость тротуаров, дорожек и площадок

Поз.	Наименование	Тип	Площадь покрытия, м²	Примечание
1	Тротуар (асфальтобетон)	1	259,85	
2	Отмостка (асфальтобетон)	2	258,15	

Ведомость элементов озеленения

Поз.	Наименование породы или вида насаждения	Воз-раст, лет	Площадь покрытия, м²	Примечание
1	Газон посевной		1860,60	м²
2	Укрепление откосов посевом трав		108,50	м²

Ведомость бортовых камней

Поз.	Наименование	Тип	пог.м	Примечание
1	БР 100.20.18 ГОСТ 32961-2014	1	317,70	


Экспликация зданий и сооружений

Номер на плане	Наименование	Примечание
1	Административно-бытовой модуль	Проектируемое
2	Мобильный комплекс железнодорожной Автоматики, телемеханики и связи (МК АТС)	Проектируемое
3	Модульный дизель-генераторный агрегат (ДГА)	Проектируемое
4	КТП	Проектируемое
5	Модуль автоматизированной системы диагностики тормозов (АСДТ)	Проектируемое
6	Модульная компрессорная	Проектируемое
7	Кладовая для хранения путевого инструмента и материалов ВСП	Проектируемое
8	Туалетный модуль 1.4х1.7	Проектируемое
9	ТКО	Проектируемое

Условные обозначения

	Граница проектирования благоустройства
	Проектируемое здание
	Тротуар из асфальтобетона
	Отмостка
	Газон
	Откос
	Бортовой камень БР100.20.8
	Бровка земляного полотна

Укрепление откосов

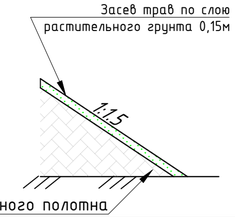

1. Система высот Балтийская 1977 г.
2. Система координат местная.
3. Размеры даны в метрах

Изм.	Кол.уч.	Лист	№док.	Подпись	Дата	1439/2025/4-ГП.ДП-6.1			
						Инфраструктура индустриального парка «Этилен-600», Железнодорожная инфраструктура. Этап №4. Строительство железнодорожных путей общего пользования (приемоотправочный парк ст. Круглое Поле)			
Разраб.		Бурайкин			09.26	Этап №4	Стадия	Лист	Листов
Проверил		Сундеев			09.26		Р	6.1	
Н. контр.		Грошев			09.26	План благоустройствам 1:500. Площадка в районе четной горловины проектируемого Парка	ГРАДО ПРОЕКТ		


Взам. инв. №

Подп. и дата

Инв. № подл.

Формат А4х3

Площадка в районе нечетной горловины проектируемого Парка

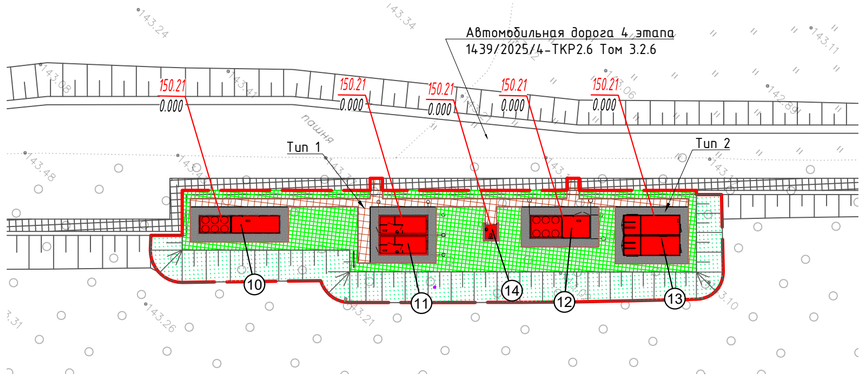


Экспликация зданий и сооружений

Номер на плане	Наименование	Примечание
10	Модуль автоматизированной системы диагностики тормозов (АСДТ)	Проектируемое
11	Модульный пункт обогрева	Проектируемое
12	Модульная компрессорная	Проектируемое
13	КТП	Проектируемое
14	Туалетный модуль 1,4х1,7	Проектируемое


Условные обозначения

	Граница проектирования благоустройства
	Проектируемое здание
	Тротуар из асфальтобетона
	Отмостка
	Газон
	Откос
	Бортовой камень БР100.20.8
	Бровка земляного полотна

Установка бортового камня БР100.20.8
в сопряжении тротуара и газона

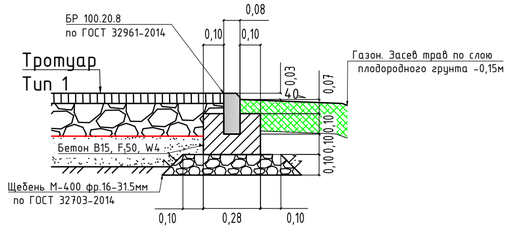

Установка бортового камня БР100.20.8
в сопряжении отмостки и газона

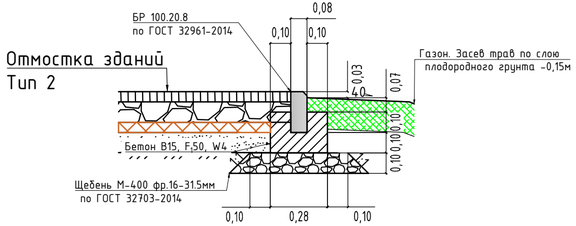

Ведомость тротуаров, дорожек и площадок

Поз.	Наименование	Тип	Площадь покрытия, м²	Примечание
1	Тротуар (асфальтобетон)	1	81,80	
2	Отмостка (асфальтобетон)	2	106,50	


Ведомость элементов озеленения

Поз.	Наименование породы или вида насаждения	Воз-раст, лет	Площадь покрытия, м²	Примечание
1	Газон посевной		274,60	м²
2	Укрепление откосов посевом трав		298,30	м²

Ведомость бортовых камней

Поз.	Наименование	Тип	пог.м	Примечание
1	БР 100.20.18 ГОСТ 32961-2014	1	186,20	

Укрепление откосов

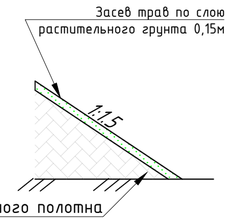

1. Система высот Балтийская 1977 г.
2. Система координат местная.
3. Размеры даны в метрах

Изм.	Кол.уч.	Лист	№док.	Подпись	Дата	1439/2025/4-ГП.ДП-6.2			
						Инфраструктура индустриального парка «Этилен-600», Железнодорожная инфраструктура. Этап №4. Строительство железнодорожных путей общего пользования (приемоотправочный парк ст. Круглое Поле)			
Разраб.		Бурайкин			09.26	Этап №4	Стадия	Лист	Листов
Проверил		Сундеев			09.26		Р	6.2	
Н. контр.		Грошев			09.26	План благоустройства М 1:500 Площадка в районе четной горловины проектируемого Парка	ГРАДО ПРОЕКТ		

Взам. инв. №

Подп. и дата

Инв. № подл.

Формат А4х3