ОБЩЕСТВО С ОГРАНИЧЕННОЙ ОТВЕТСТВЕННОСТЬЮ

alabuga DEVELOPMENT

№ СРО-П-114-14012010

Заказчик – АО «ОЭЗ ППТ «Алабуга»

Инфраструктура индустриального парка «Этилен-600», Железнодорожная инфраструктура.

Этап №4. Строительство железнодорожных путей общего пользования (приемоотправочный парк ст. Круглое Поле)

РАБОЧАЯ ДОКУМЕНТАЦИЯ

Генеральный план.
Здания для обслуживания стрелочных переводов

1439/2025/4-ГП.СП

2026 г.

ОБЩЕСТВО С ОГРАНИЧЕННОЙ ОТВЕТСТВЕННОСТЬЮ

№ СРО-П-114-14012010

Заказчик – АО «ОЭЗ ППТ «Алабуга»

Инфраструктура индустриального парка «Этилен-600», Железнодорожная инфраструктура.

Этап №4. Строительство железнодорожных путей общего пользования (приемоотправочный парк ст. Круглое Поле)

РАБОЧАЯ ДОКУМЕНТАЦИЯ

Генеральный план.
Здания для обслуживания стрелочных переводов

1439/2025/4-ГП.СП

Главный инженер Мезенцев Д.В.

2026 г.

Общество с ограниченной ответственностью
«ГрадоПроект»

Инфраструктура индустриального парка «Этилен-600», Железнодорожная инфраструктура.

Этап №4. Строительство железнодорожных путей общего пользования (приемоотправочный парк ст. Круглое Поле)

РАБОЧАЯ ДОКУМЕНТАЦИЯ

Генеральный план.
Здания для обслуживания стрелочных переводов

1439/2025/4-ГП.СП

Директор **И. А. Трубицин**

Главный инженер проекта **В. В. Сундеев**

2026 г.

Ведомость ссылочных и прилагаемых документов

Обозначение	Наименование	Примечание
	Ссылочные документы	
ГОСТ 32824-2014	Дороги автомобильные общего пользования. Песок природный	
ГОСТ 58406.2-2020	Дороги автомобильные общего пользования. Смеси горячие асфальтобетонные и асфальтобетон	
ГОСТ 32703-2014	Дороги автомобильные общего пользования. Щебень и гравий из плотных горных пород для строительных работ	
ГОСТ 32961-2014	Дороги автомобильные общего пользования. Камни бортовые	
ГОСТ 6665-91	Камни бетонные и железобетонные бортовые	
ГОСТ 32945-2014	Дороги автомобильные общего пользования. Знаки дорожные	

Ведомость рабочих чертежей основного комплекта

Лист	Наименование	Примечание
1	Общие данные	
2.1	Разбивочный план (1:500). Площадка размещения зданий в районе стрелочных переводов: №5, 7, 35, 37, 39, 41	
2.2	Разбивочный план (1:500). Площадка размещения зданий в районе стрелочных переводов: №1, 3	
2.3	Разбивочный план (1:500). Площадка размещения зданий в районе стрелочных переводов: №302, 304, 306, 308	
3.1	План организации рельефа (1:500). Площадка размещения зданий в районе стрелочных переводов: №5, 7, 35, 37, 39, 41	
3.2	План организации рельефа (1:500). Площадка размещения зданий в районе стрелочных переводов: №1, 3	
3.3	План организации рельефа (1:500). Площадка размещения зданий в районе стрелочных переводов: №302, 304, 306, 308	
4.1	План земляных масс (1:500). Площадка размещения зданий в районе стрелочных переводов: №5, 7, 35, 37, 39, 41	
4.2	План земляных масс (1:500). Площадка размещения зданий в районе стрелочных переводов: №1, 3	
4.3	План земляных масс (1:500). Площадка размещения зданий в районе стрелочных переводов: №302, 304, 306, 308	
5.1	Сводный план сетей инженерно-технического обеспечения (1:500). Площадка размещения зданий в районе стрелочных переводов: №5, 7, 35, 37, 39, 41	
5.2	Сводный план сетей инженерно-технического обеспечения (1:500). Площадка размещения зданий в районе стрелочных переводов: №1, 3	
5.3	Сводный план сетей инженерно-технического обеспечения (1:500). Площадка размещения зданий в районе стрелочных переводов: №302, 304, 306, 308	
6.1	План благоустройства (1:500). Площадка размещения зданий в районе стрелочных переводов: №5, 7, 35, 37, 39, 41	
6.2	План благоустройства (1:500). Площадка размещения зданий в районе стрелочных переводов: №1, 3	
6.3	План благоустройства (1:500). Площадка размещения зданий в районе стрелочных переводов: №302, 304, 306, 308	

Общие указания

1 Рабочая документация разработана на основании задания на разработку проектно-сметной документации «Инфраструктура индустриального парка «Этилен-600», Железнодорожная инфраструктура. Этап №4. Строительство железнодорожных путей общего пользования (приемоотправочный парк ст. Круглое Поле)

2 Рабочие чертежи разработаны в соответствии действующими нормами, правилами и стандартами, действующими на территории Российской Федерации:

- СП 18.13330.2019 "Генеральные планы промышленных предприятий. Актуализированная редакция СНиП II-89-80*";
- СП 4.131.30.2013 «Системы противопожарной защиты. Ограничение распространения пожара на объектах защиты. Требования к объемно-планировочным и конструктивным решениям»;
- СП 34.13330.2021 «Автомобильные дороги»;
- СП 34.13330.2012 «Промышленный транспорт»;
- ГОСТ 21.508-2020 «СПДС. Правила выполнения рабочей документации генеральных планов предприятий, сооружений и жилищно-гражданских объектов»;
- ГОСТ Р 21.101-2020 «Основные требования к проектной и рабочей документации»;
- СанПин 2.2.1/2.1.1.1200-03 «Санитарно-защитные зоны и санитарная классификация предприятий, сооружений и иных объектов»;
- ПУЭ «Правила устройства электроустановок. Издание 7».

3 В качестве подосновы для выполнения чертежей использована топографическая съемка участка, выполненная ООО "Геодезия Кадастр Изыскания" в 2026 г.

4 Система высот Балтийская 1977 г.

5 Система координат МСК-16.

6 Основные виды работ, для которых необходимо составлять акты на скрытые работы:

- снятие растительного слоя;
- укладка геотекстиля и геосетки;
- послойная отсыпка, послойное уплотнение, планировка земляного полотна и корыта;
- уплотнение и планировка обочин и откосов, засев трав при укреплении;
- засыпка коммуникаций и сооружений;
- сооружение каждого конструктивного слоя основания;
- сооружение каждого конструктивного слоя покрытия.

Взам. инв. №


Подп. и дата

Инв. № подл.


Изм.	Кол.уч.	Лист	№док.	Подпись	Дата	1439/2025/4-ГП.СП-1			
						Инфраструктура индустриального парка «Этилен-600», Железнодорожная инфраструктура. Этап №4. Строительство железнодорожных путей общего пользования (приемоотправочный парк ст. Круглое Поле)			
Разраб.		Бурайкин			09.26	Этап №4	Стадия	Лист	Листов
Проверил		Сундеев			09.26		Р	1	16
Н. контр.		Грошев			09.26	Общие данные	ГРАДО ПРОЕКТ		

Формат А4х3


Площадка размещения зданий в районе стрелочных переводов: №5, 7, 35, 37, 39, 41

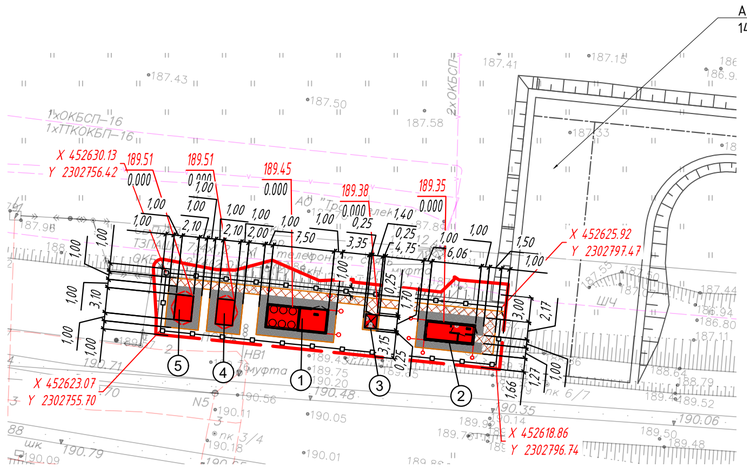


Установка бортового камня БР100.20.8 в сопряжении отмостки и газона

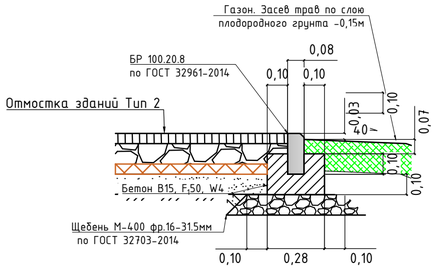

Установка бортового камня БР100.20.8 в сопряжении тротуара и газона

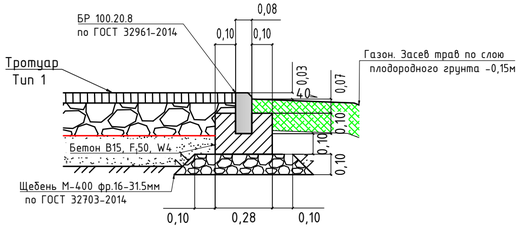


Тип 1. Тротуар

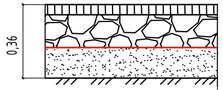

Покрытие: асфальтобетон А5Вл по ГОСТ 58406.2-2020 на битуме PG 64-22 вяжущее по ГОСТ 58400.1-2019	-0,05м
Слой основания: щебень М-600 по ГОСТ 32703-2014 фр. 16-31.5мм	-0,16м
Разделяющая прослойка: нетканый геотекстиль предельная прочность не менее 5кН/м, ГОСТ Р 56419-2015	
Дополнительный слой основания: песок очень мелкий по ГОСТ 32824-2014 Кф>1 м/сут	-0,15м

Тип 2. Отмостка зданий

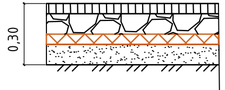

Покрытие: асфальтобетон А5Вл по ГОСТ 58406.2-2020 на битуме PG 64-22 вяжущее по ГОСТ 58400.1-2019	-0,05м
Слой основания: щебень М-600 по ГОСТ 32703-2014 фр. 16-31.5мм	-0,10м
Гидроизоляция	
Утеплитель ЭППС	-0,05м
Дополнительный слой основания: песок очень мелкий по ГОСТ 32824-2014 Кф>1 м/сут	-0,10м


Экспликация зданий и сооружений

Номер на плане	Наименование	Примечание
1	Модульная компрессорная	Проектируемое
2	Модульный пункт обогрева	Проектируемое
3	Туалетный модуль	Проектируемое
4,5	Трансформаторная подстанция	Проектируемое

Условные обозначения

	Граница проектирования благоустройства
	Проектируемое здание
	Откос
	Бортовой камень БР100.20.8
	Бровка земляного полотна
	Ограждение l=93,70 м
	Калитка 1,50 м

Укрепление откосов

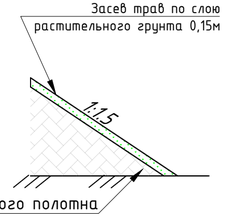

1. Система высот Балтийская 1977 г.
2. Система координат местная.
3. Размеры даны в метрах

Изм.	Кол.уч.	Лист	№док.	Подпись	Дата
Разраб.		Бурайкин			09.26
Проверил		Сундеев			09.26
Н. контр.		Грошев			09.26

1439/2025/4-ГП.СП-2.1

Инфраструктура индустриального парка «Этилен-600», Железнодорожная инфраструктура. Этап №4. Строительство железнодорожных путей общего пользования (приемоотправочный парк ст. Круглое Поле)

Этап №4

Стадия	Лист	Листов
Р	2.1	

Разбивочный план М 1:500. Площадка размещения зданий в районе стрелочных переводов: №5, 7, 35, 37, 39, 41

ГРАДО ПРОЕКТ

Взам. инв. №

Подп. и дата


Инв. № подл.

Формат А4х3


Площадка размещения зданий в районе стрелочных переводов: №1, 3




Установка бортового камня БР100.20.8 в сопряжении отмостки и газона

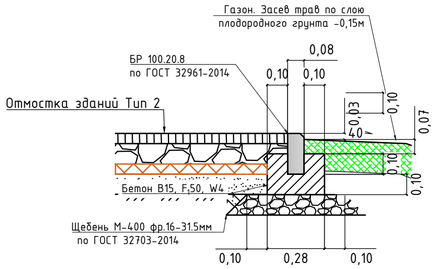

Установка бортового камня БР100.20.8 в сопряжении тротуара и газона

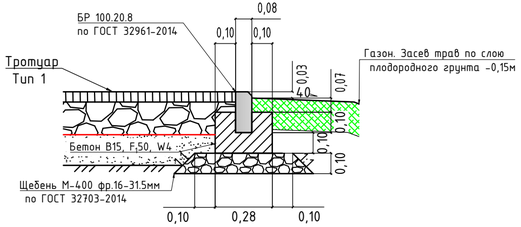


Тип 1. Тротуар

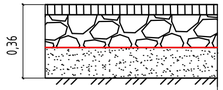

Покрытие: асфальтобетон А5Вл по ГОСТ 58406.2-2020 на битуме PG 64-22 вяжущее по ГОСТ 58400.1-2019	-0,05м
Слой основания: щебень М-600 по ГОСТ 32703-2014 фр. 16-31.5мм	-0,16м
Разделяющая прослойка: нетканый геотекстиль предельная прочность не менее 5кН/м, ГОСТ Р 56419-2015	
Дополнительный слой основания: песок очень мелкий по ГОСТ 32824-2014 Кф>1 м/сут	-0,15м

Тип 2. Отмостка зданий

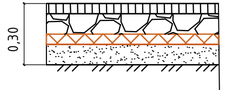

Покрытие: асфальтобетон А5Вл по ГОСТ 58406.2-2020 на битуме PG 64-22 вяжущее по ГОСТ 58400.1-2019	-0,05м
Слой основания: щебень М-600 по ГОСТ 32703-2014 фр. 16-31.5мм	-0,10м
Гидроизоляция	
Утеплитель ЭППС	-0,05м
Дополнительный слой основания: песок очень мелкий по ГОСТ 32824-2014 Кф>1 м/сут	-0,10м


Экспликация зданий и сооружений

Номер на плане	Наименование	Примечание
6	Модульная компрессорная	Проектируемое
7	Модульный пункт обогрева	Проектируемое
8	Туалетный модуль	Проектируемое
9,10	Трансформаторная подстанция	Проектируемое

Условные обозначения

	Граница проектирования благоустройства
	Проектируемое здание
	Откос
	Бортовой камень БР100.20.8
	Бровка земляного полотна
	Ограждение l=90,70 м
	Калитка 1,50 м

Укрепление откосов

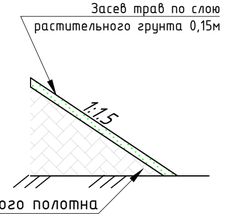

1. Система высот Балтийская 1977 г.
2. Система координат местная.
3. Размеры даны в метрах

Изм.	Кол.уч.	Лист	№док.	Подпись	Дата	1439/2025/4-ГП.СП-2.2			
						Инфраструктура индустриального парка «Этилен-600», Железнодорожная инфраструктура. Этап №4. Строительство железнодорожных путей общего пользования (приемоотправочный парк ст. Круглое Поле)			
Разраб.		Бурайкин			09.26	Этап №4	Стадия	Лист	Листов
Проверил		Сундеев			09.26		Р	2.2	
Н. контр.		Грошев			09.26	Разбивочный план М 1:500. Площадка размещения зданий в районе стрелочных переводов: №1, 3	ГРАДО ПРОЕКТ		


Взам. инв. №

Подп. и дата

Инв. № подл.


Формат А4х3

Площадка размещения зданий в районе стрелочных переводов: №302, 304, 306, 308

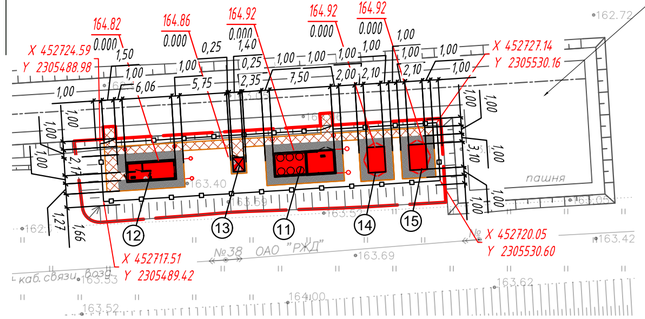


Автомобильная дорога 4 этапа 1439/2025/4-ТКР2.6 Том 3.2.6


Установка бортового камня БР100.20.8 в сопряжении отмостки и газона

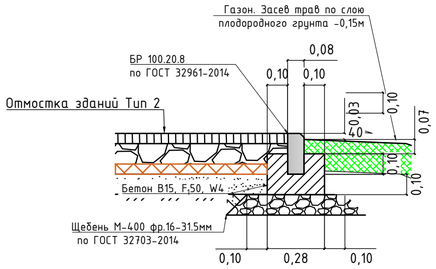

Установка бортового камня БР100.20.8 в сопряжении тротуара и газона

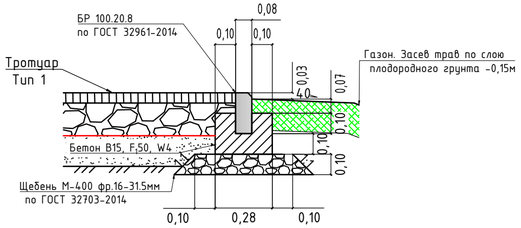


Тип 1. Тротуар

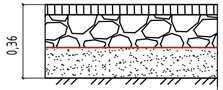

Покрытие: асфальтобетон А5Вл по ГОСТ 58406.2-2020 на битуме PG 64-22 вяжущее по ГОСТ 58400.1-2019	-0,05м
Слой основания: щебень М-600 по ГОСТ 32703-2014 фр. 16-31.5мм	-0,16м
Разделяющая прослойка: нетканый геотекстиль предельная прочность не менее 5кН/м, ГОСТ Р 56419-2015	
Дополнительный слой основания: песок очень мелкий по ГОСТ 32824-2014 Кф>1 м/сут	-0,15м

Тип 2. Отмостка зданий

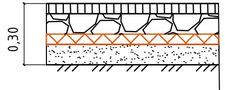

Покрытие: асфальтобетон А5Вл по ГОСТ 58406.2-2020 на битуме PG 64-22 вяжущее по ГОСТ 58400.1-2019	-0,05м
Слой основания: щебень М-600 по ГОСТ 32703-2014 фр. 16-31.5мм	-0,10м
Гидроизоляция	
Утеплитель ЭППС	-0,05м
Дополнительный слой основания: песок очень мелкий по ГОСТ 32824-2014 Кф>1 м/сут	-0,10м


Экспликация зданий и сооружений

Номер на плане	Наименование	Примечание
11	Модульная компрессорная	Проектируемое
12	Модульный пункт обогрева	Проектируемое
13	Туалетный модуль	Проектируемое
14,15	Трансформаторная подстанция	Проектируемое

Условные обозначения

	Граница проектирования благоустройства
	Проектируемое здание
	Откос
	Бортовой камень БР100.20.8
	Бровка земляного полотна
	Ограждение l=93,70 м
	Калитка 1,50 м

Укрепление откосов

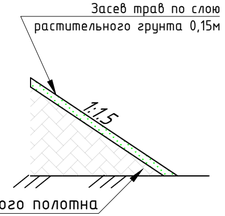

1. Система высот Балтийская 1977 г.
2. Система координат местная.
3. Размеры даны в метрах

Изм.	Кол.уч.	Лист	№док.	Подпись	Дата	1439/2025/4-ГП.СП-2.3			
						Инфраструктура индустриального парка «Этилен-600», Железнодорожная инфраструктура. Этап №4. Строительство железнодорожных путей общего пользования (приемоотправочный парк ст. Круглое Поле)			
Разраб.		Бурайкин			09.26	Этап №4	Стадия	Лист	Листов
Проверил		Сундеев			09.26		Р	2.3	
Н. контр.		Грошев			09.26	Разбивочный план М 1:500. Площадка размещения зданий в районе стрелочных переводов: №302, 304, 306, 308	ГРАДО ПРОЕКТ		

Взам. инв. №


Подп. и дата

Инв. № подл.

Формат А4х3

С

Площадка размещения зданий в районе стрелочных переводов: №5, 7, 35, 37, 39, 41

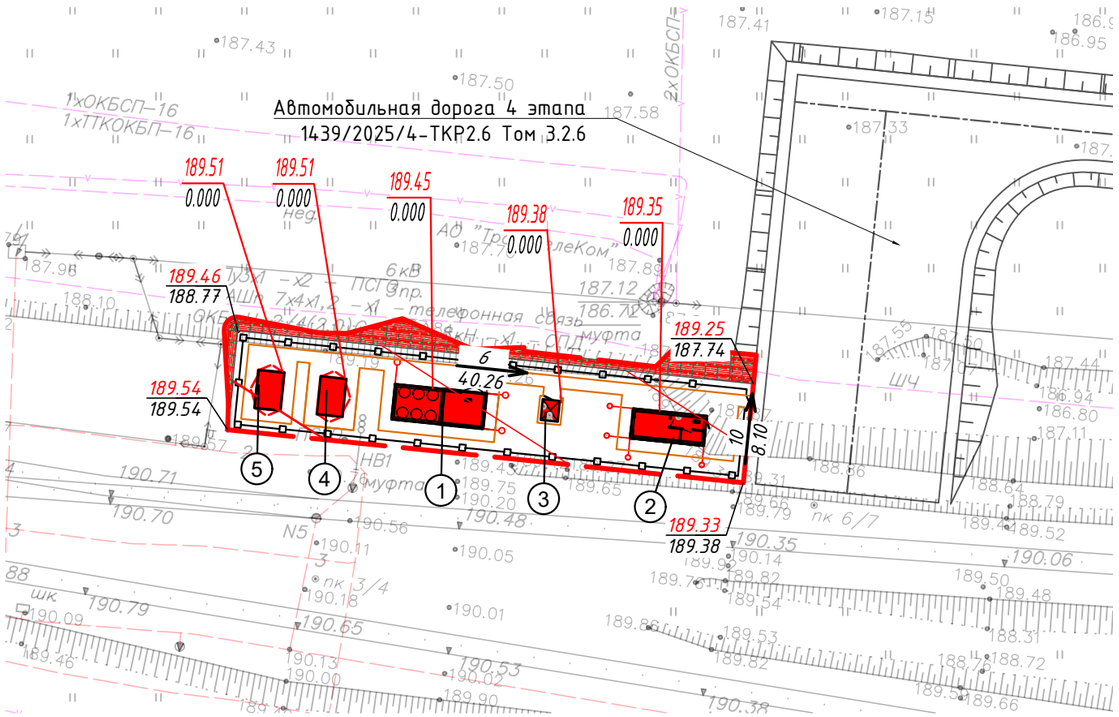

Экспликация зданий и сооружений

Номер на плане	Наименование	Примечание
1	Модульная компрессорная	Проектируемое
2	Модульный пункт обогрева	Проектируемое
3	Туалетный модуль	Проектируемое
4,5	Трансформаторная подстанция	Проектируемое

Условные обозначения

	Граница проектирования благоустройства
	Проектируемое здание
	Откос
	Бортовой камень БР100.20.8
	Бровка земляного полотна
	Ограждение l=93,70 м
	Калитка 1,50 м
	Проектная горизонталь
5 / 42.26	Направление уклона проектируемого рельефа
189.54 / 189.54	Отметка поверхности (проектная / существующая)

1. Система высот Балтийская 1977 г.
2. Система координат местная.
3. Отметки и уклоноуказатели приведены по верху покрытия.

Изм.	Кол.уч	Лист	N°док.	Подпись	Дата
Разраб.		Бурайкин			09.26
Проверил		Сундеев			09.26
Н. контр.		Грошев			09.26

1439/2025/4-ГП.СП-3.1

Инфраструктура индустриального парка «Этилен-600», Железнодорожная инфраструктура. Этап №4. Строительство железнодорожных путей общего пользования (приемоотправочный парк ст. Круглое Поле)

Этап №4	Стадия	Лист	Листов
	Р	3.1	

План организации рельефа М 1:500. Площадка размещения зданий в районе стрелочных переводов: №5, 7, 35, 37, 39, 41

ГРАДО ПРОЕКТ

Взам. инв. N°


Подп. и дата

Инв. N° подл.

Формат А3

С

Площадка размещения зданий в районе стрелочных переводов: №1, 3

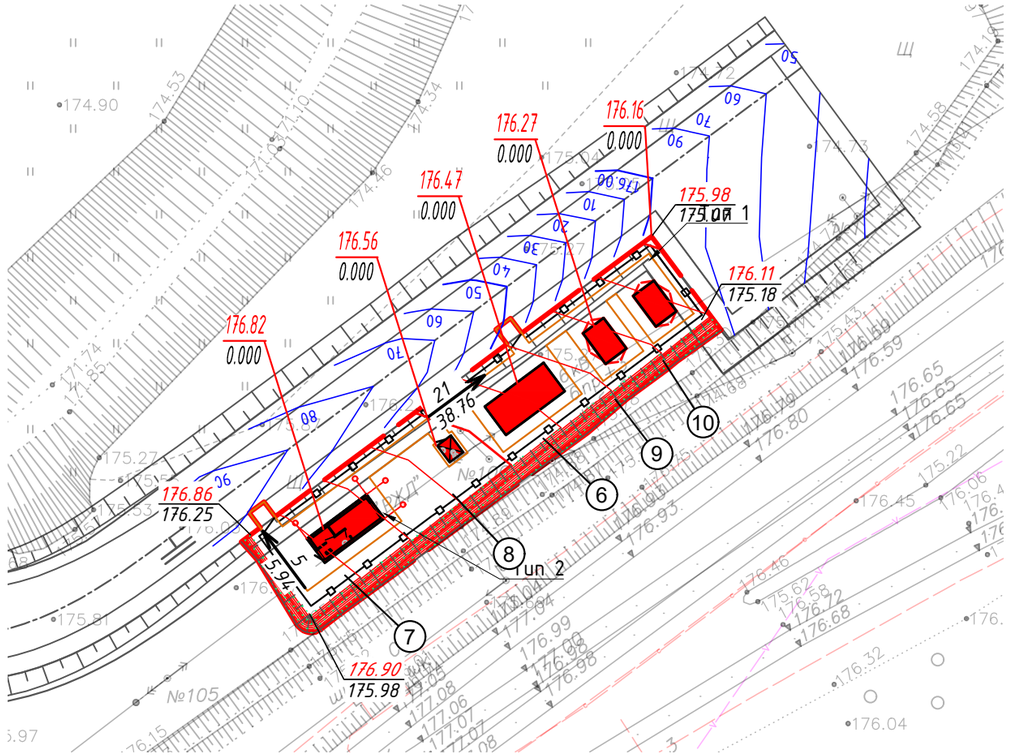

Экспликация зданий и сооружений

Номер на плане	Наименование	Примечание
6	Модульная компрессорная	Проектируемое
7	Модульный пункт обогрева	Проектируемое
8	Туалетный модуль	Проектируемое
9,10	Трансформаторная подстанция	Проектируемое

Условные обозначения

	Граница проектирования благоустройства
	Проектируемое здание
	Откос
	Бортовой камень БР100.20.8
	Бровка земляного полотна
	Ограждение l=90,70 м
	Калитка 1,50 м
	Проектная горизонталь
	Проектная горизонталь АД 4 этапа 1439/2025/4-ТКР2.6 Том 3.2.6
27 / 5.00	Направление уклона проектируемого рельефа
153.40 / 152.47	Отметка поверхности (проектная / существующая)
153.06 / 152.06	Точка перелома проектируемого рельефа (проектная / существующая)

1. Система высот Балтийская 1977 г.
2. Система координат местная.
3. Отметки и уклоноуказатели приведены по верху покрытия.

Изм.	Кол.уч	Лист	N°док.	Подпись	Дата
Разраб.		Бурайкин			09.26
Проверил		Сундеев			09.26
Н. контр.		Грошев			09.26

1439/2025/4-ГП.СП-3.2

Инфраструктура индустриального парка «Этилен-600», Железнодорожная инфраструктура. Этап №4. Строительство железнодорожных путей общего пользования (приемоотправочный парк ст. Круглое Поле)

Этап №4	Стадия	Лист	Листов
	Р	3.2	

План организации рельефа М 1:500. Площадка размещения зданий в районе стрелочных переводов: №1, 3

ГРАДО ПРОЕКТ

Взам. инв. N°


Подп. и дата

Инв. N° подл.

Формат А3

С

Площадка размещения зданий в районе стрелочных переводов: №302, 304, 306, 308

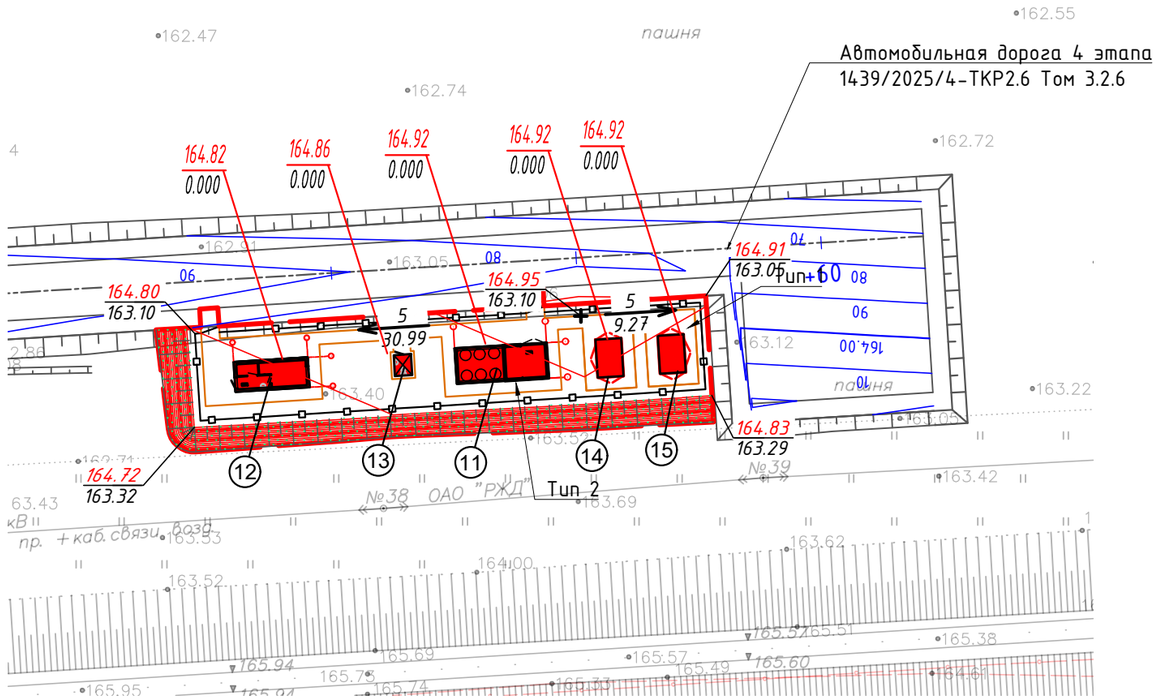

Экспликация зданий и сооружений

Номер на плане	Наименование	Примечание
11	Модульная компрессорная	Проектируемое
12	Модульный пункт обогрева	Проектируемое
13	Туалетный модуль	Проектируемое
14,15	Трансформаторная подстанция	Проектируемое

Условные обозначения

	Граница проектирования благоустройства
	Проектируемое здание
	Откос
	Бортовой камень БР100.20.8
	Бровка земляного полотна
	Ограждение l=93,70 м
	Калитка 1,50 м
	Проектная горизонталь
	Проектная горизонталь АД 4 этапа 1439/2025/4-ТКР2.6 Том 3.2.6
27 / 5.00	Направление уклона проектируемого рельефа
153.40 / 152.47	Отметка поверхности (проектная / существующая)
153.06 / 152.06	Точка перелома проектируемого рельефа (проектная / существующая)

1. Система высот Балтийская 1977 г.
2. Система координат местная.
3. Отметки и уклоноуказатели приведены по верху покрытия.

Изм.	Кол.уч	Лист	№док.	Подпись	Дата
Разраб.		Бурайкин			09.26
Проверил		Сундеев			09.26
Н. контр.		Грошев			09.26

1439/2025/4-ГП.СП-3.3

Инфраструктура индустриального парка «Этилен-600», Железнодорожная инфраструктура. Этап №4. Строительство железнодорожных путей общего пользования (приемоотправочный парк ст. Круглое Поле)

Этап №4

Стадия	Лист	Листов
Р	3.3	

План организации рельефа М 1:500. Площадка размещения зданий в районе стрелочных переводов: №302, 304, 306, 308

ГРАДО ПРОЕКТ

Взам. инв. №


Подп. и дата

Инв. № подл.

Формат А3

С

Площадка размещения зданий в районе стрелочных переводов: №5, 7, 35, 37, 39, 41

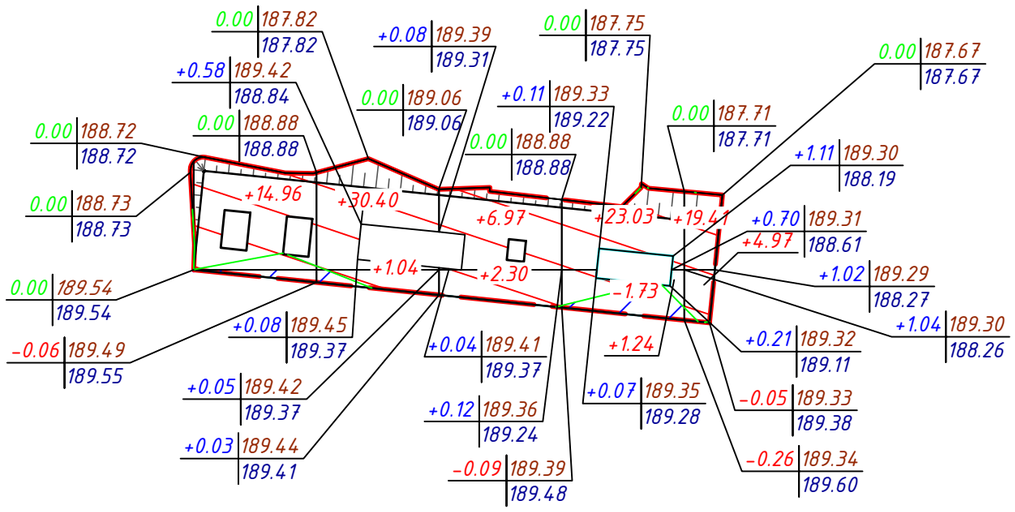

Итого, м³	Насыпь	–	+14.96	+31.44	+9.27	+24.27	+24.38	Всего, м³ +104.32
	Выемка	–	–	–	–	-1.73	–	-1.73

Площадь картограммы – 324.60 м², в т.ч.:
насыпь – 308.25 м², выемка – 16.35 м²

Условные обозначения

рабочая отметка
-0.26
красная отметка
189.34
189.60
черная отметка

Выемка

+2.30
Насыпь

Ведомость объемов земляных масс

Наименование грунта	Количество, м³		Примечание
	Насыпь (+)	Выемка (–)	
1. Грунт планировки территории	105	2	
2. Вытесненный грунт, в т.ч. при устройстве:		75	
а) тротуара		19	
б) отмостки		23	
в) газона и откоса		33	
3. Поправка на уплотнение, k=0,1	11	–	
4. Всего пригодного грунта	116	77	
5. Недостаток пригодного грунта		39	
7. Плодородный грунт, всего:			
а) используемый для озеленения территории	33	–	
б) недостаток плодородного грунта		33	
8. Итого перерабатываемого грунта	149	149	

1. Система высот Балтийская 1977 г.
2. Система координат местная.
3. Картограмма разработана в программном комплексе Civil3d.
4. При расчете картограммы квадраты сетки приняты стороной равной 10 м.
5. Необходимость замены грунта под зданиями и сооружениями определена в марке КР.
6. Коэффициент уплотнения – не менее 0,95. Толщина каждого слоя 0,3-0,6 м (уточняется по результатам опытного уплотнения).
7. После возведения земляного полотна откосы необходимо доуплотнять планировщиками-уплотнителями.

Изм.	Кол.уч	Лист	N°док.	Подпись	Дата
Разраб.		Бурайкин			09.26
Проверил		Сундеев			09.26
Н. контр.		Грошев			09.26

1439/2025/4-ГП.СП-4.1

Инфраструктура индустриального парка «Этилен-600», Железнодорожная инфраструктура. Этап №4. Строительство железнодорожных путей общего пользования (приемоотправочный парк ст. Круглое Поле)

Этап №4

Стадия	Лист	Листов
Р	4.1	

План земляных масс М 1:500. Площадка размещения зданий в районе стрелочных переводов: №5, 7, 35, 37, 39, 41


ГРАДО ПРОЕКТ

Взам. инв. N° | Подп. и дата | Инв. N° подл.

Формат А3

С


Площадка размещения зданий в районе стрелочных переводов: №1, 3

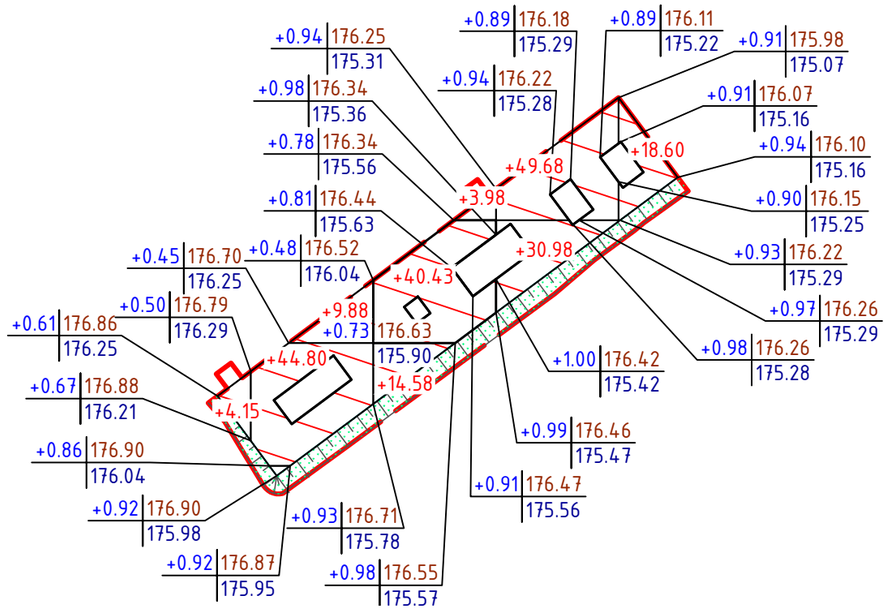

Итого, м³							Всего, м³	
	Насыпь	+4.15	+54.68	+58.99	+80.66	+18.60		+217.08
	Выемка	-	-	-	-	-		-

Площадь картограммы - 281.86 м², в т.ч.:
насыпь - 281.86 м², выемка - 0.00 м²

Условные обозначения

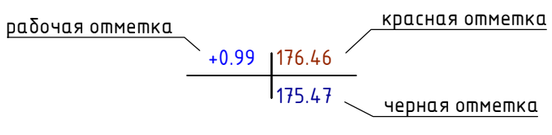

Ведомость объемов земляных масс

Наименование грунта	Количество, м³		Примечание
	Насыпь (+)	Выемка (-)	
1. Грунт планировки территории	217	-	
2. Вытесненный грунт, в т.ч. при устройстве:		77	
а) тротуара		20	
б) отмостки		22	
в) газона и откоса		35	
3. Поправка на уплотнение, k=0,1	22	-	
4. Всего пригодного грунта	239	77	
5. Недостаток пригодного грунта		162	
7. Плодородный грунт, всего:			
а) используемый для озеленения территории	35	-	
б) недостаток плодородного грунта		35	
8. Итого перерабатываемого грунта	274	274	

1. Система высот Балтийская 1977 г.
2. Система координат местная.
3. Картограмма разработана в программном комплексе Civil3d.
4. При расчете картограммы квадраты сетки приняты стороной равной 10 м.
5. Необходимость замены грунта под зданиями и сооружениями определена в марке КР.
6. Коэффициент уплотнения - не менее 0,95. Толщина каждого слоя 0,3-0,6 м (уточняется по результатам опытного уплотнения).
7. После возведения земляного полотна откосы необходимо доуплотнять планировщиками-уплотнителями.

Взам. инв. №

Подп. и дата

Инв. № подл.

Изм.	Кол.уч	Лист	№док.	Подпись	Дата
Разраб.		Бурайкин			09.26
Проверил		Сундеев			09.26
Н. контр.		Грошев			09.26

1439/2025/4-ГП.СП-4.2

Инфраструктура индустриального парка «Этилен-600», Железнодорожная инфраструктура. Этап №4. Строительство железнодорожных путей общего пользования (приемоотправочный парк ст. Круглое Поле)

Этап №4

Стадия	Лист	Листов
Р	4.2	


План земляных масс М 1:500. Площадка размещения зданий в районе стрелочных переводов: №1, 3

ГРАДО ПРОЕКТ

Формат А3

С

Площадка размещения зданий в районе стрелочных переводов: №302, 304, 306, 308

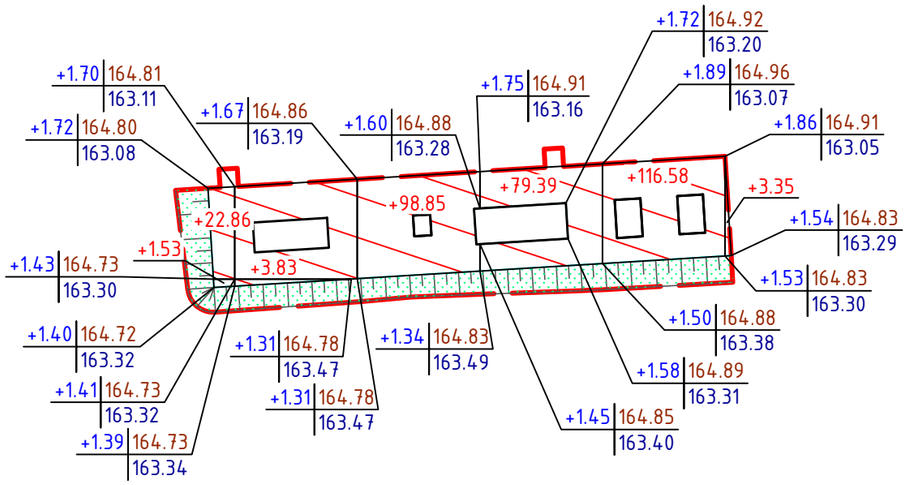

Итого, м³								Всего, м³	
	Насыпь	+24.39	+99.97	+98.85	+79.39	+116.58	+3.35		+422.53
	Выемка	-	-	-	-	-	-		-

Площадь картограммы - 290.29 м², в т.ч.:
насыпь - 290.29 м², выемка - 0.00 м²

Условные обозначения

рабочая отметка +1.60 | красная отметка 164.88 | черная отметка 163.28

+79.39 — Насыпь

Ведомость объемов земляных масс

Наименование грунта	Количество, м³		Примечание
	Насыпь (+)	Выемка (-)	
1. Грунт планировки территории	423	-	
2. Вытесненный грунт, в т.ч. при устройстве:		85	
а) тротуара		21	
б) отмостки		23	
в) газона и откоса		41	
3. Поправка на уплотнение, k=0,1	43	-	
4. Всего пригодного грунта	466	85	
5. Недостаток пригодного грунта		381	
7. Плодородный грунт, всего:			
а) используемый для озеленения территории	41		
б) недостаток плодородного грунта		41	
8. Итого перерабатываемого грунта	507	507	

1. Система высот Балтийская 1977 г.
2. Система координат местная.
3. Картограмма разработана в программном комплексе Civil3d.
4. При расчете картограммы квадраты сетки приняты стороной равной 10 м.
5. Необходимость замены грунта под зданиями и сооружениями определена в марке КР.
6. Коэффициент уплотнения - не менее 0,95. Толщина каждого слоя 0,3-0,6 м (уточняется по результатам опытного уплотнения).
7. После возведения земляного полотна откосы необходимо доуплотнять планировщиками-уплотнителями.

Изм.	Кол.уч	Лист	N°док.	Подпись	Дата
Разраб.		Бурайкин			09.26
Проверил		Сундеев			09.26
Н. контр.		Грошев			09.26

1439/2025/4-ГП.СП-4.3

Инфраструктура индустриального парка «Этилен-600», Железнодорожная инфраструктура. Этап №4. Строительство железнодорожных путей общего пользования (приемоотправочный парк ст. Круглое Поле)

Этап №4

Стадия	Лист	Листов
Р	4.3	


План земляных масс М 1:500. Площадка размещения зданий в районе стрелочных переводов: №302, 304, 306, 308

ГРАДО ПРОЕКТ

Взам. инв. N° | Подп. и дата | Инв. N° подл.

Формат А3

Площадка размещения зданий в районе стрелочных переводов: №5, 7, 35, 37, 39, 41

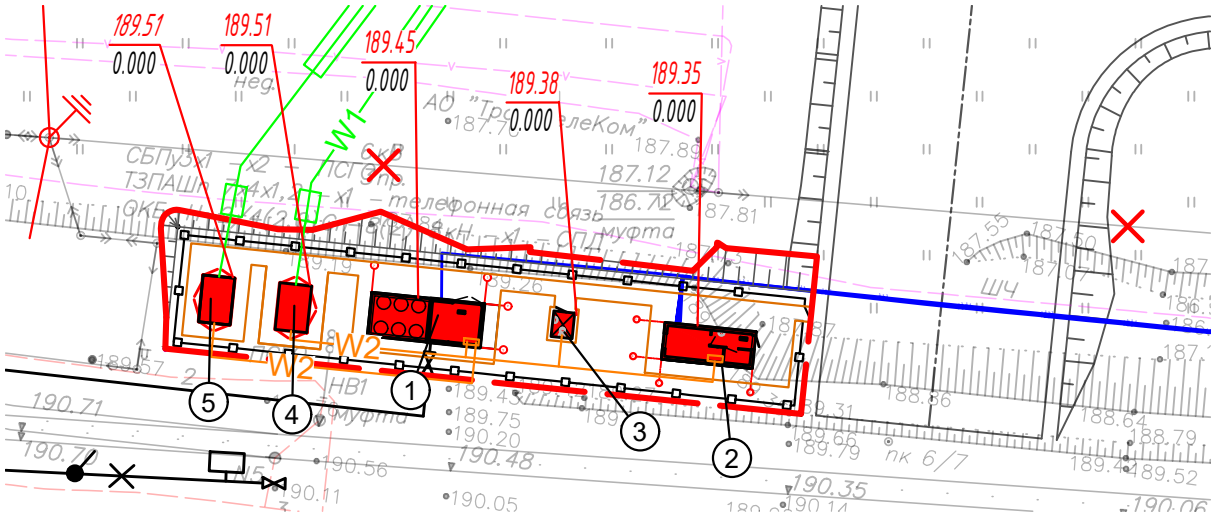

1. Система высот Балтийская 1977 г.
2. Система координат местная.

Экспликация зданий и сооружений

Номер на плане	Наименование	Примечание
1	Модульная компрессорная	Проектируемое
2	Модульный пункт обогрева	Проектируемое
3	Туалетный модуль	Проектируемое
4,5	Трансформаторная подстанция	Проектируемое

Условные обозначения

	Граница проектирования благоустройства
	Проектируемое здание
	Проектируемые сети связи
	Проектируемая сеть воздуховода
WK	Проектируемая кабельная линия электропередач
W1 / W2	Проектируемые электрические сети

Изм.	Кол.уч	Лист	N°док.	Подпись	Дата
Разраб.		Бурайкин			09.26
Проверил		Сундеев			09.26
Н. контр.		Грошев			09.26

1439/2025/4-ГП.СП-5.1

Инфраструктура индустриального парка «Этилен-600», Железнодорожная инфраструктура. Этап №4. Строительство железнодорожных путей общего пользования (приемоотправочный парк ст. Круглое Поле)

Этап №4

Стадия	Лист	Листов
Р	5.1	

Сводный план сетей инженерно-технического обеспечения М 1:500. Площадка размещения зданий в районе стрелочных переводов: №5, 7, 35, 37, 39, 41

ГРАДО ПРОЕКТ


Взам. инв. N°

Подп. и дата

Инв. N° подл.

Формат А4

Площадка размещения зданий в районе стрелочных переводов: №1, 3

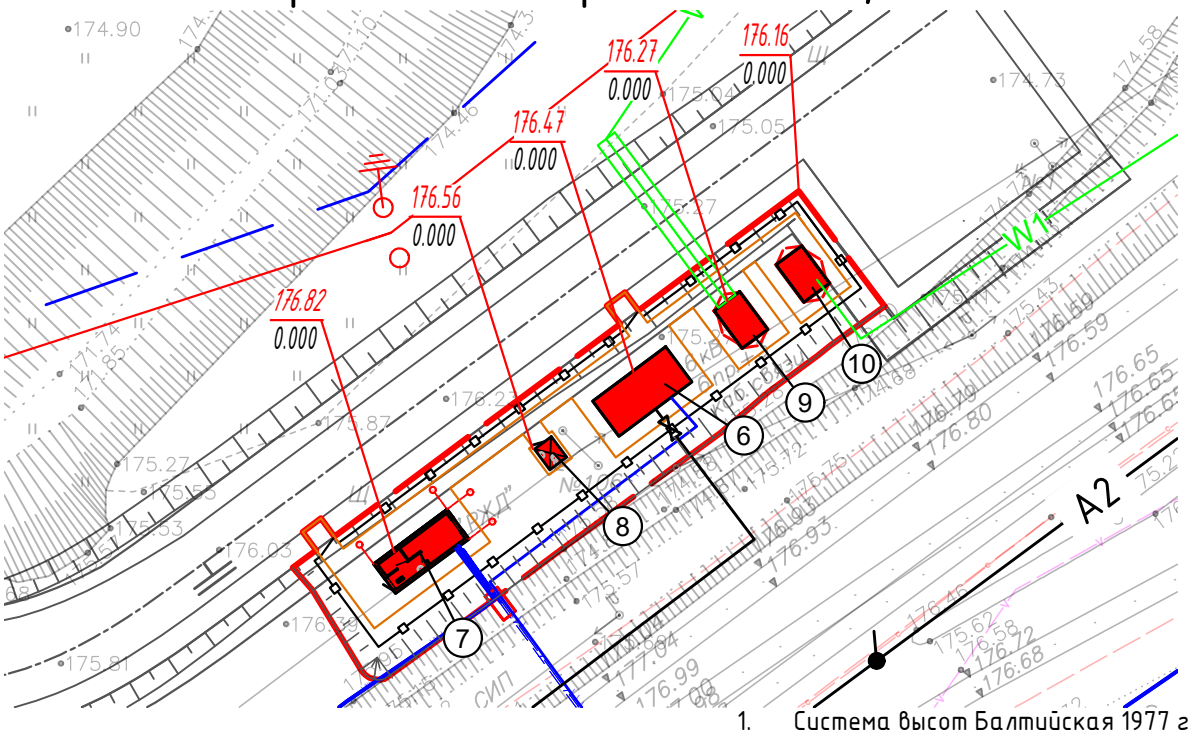

1. Система высот Балтийская 1977 г.
2. Система координат местная.

Экспликация зданий и сооружений

Номер на плане	Наименование	Примечание
6	Модульная компрессорная	Проектируемое
7	Модульный пункт обогрева	Проектируемое
8	Туалетный модуль	Проектируемое
9,10	Трансформаторная подстанция	Проектируемое

Условные обозначения

	Граница проектирования благоустройства
	Проектируемое здание
	Проектируемые сети связи
	Проектируемая сеть воздуховода
WK	Проектируемая кабельная линия электропередач
W1 / W2	Проектируемые электрические сети

Взам. инв. №

Подп. и дата

Инв. № подл.

Изм.	Кол.уч	Лист	№док.	Подпись	Дата
Разраб.		Бурайкин			09.26
Проверил		Сундеев			09.26
Н. контр.		Грошев			09.26

1439/2025/4-ГП.СП-5.2

Инфраструктура индустриального парка «Этилен-600», Железнодорожная инфраструктура. Этап №4. Строительство железнодорожных путей общего пользования (приемоотправочный парк ст. Круглое Поле)

Этап №4


Стадия	Лист	Листов
Р	5.2	

Сводный план сетей инженерно-технического обеспечения М 1:500 Площадка размещения зданий в районе стрелочных переводов: №1, 3

ГРАДО ПРОЕКТ

Формат А4

Площадка размещения зданий в районе стрелочных переводов: №302, 304, 306, 308

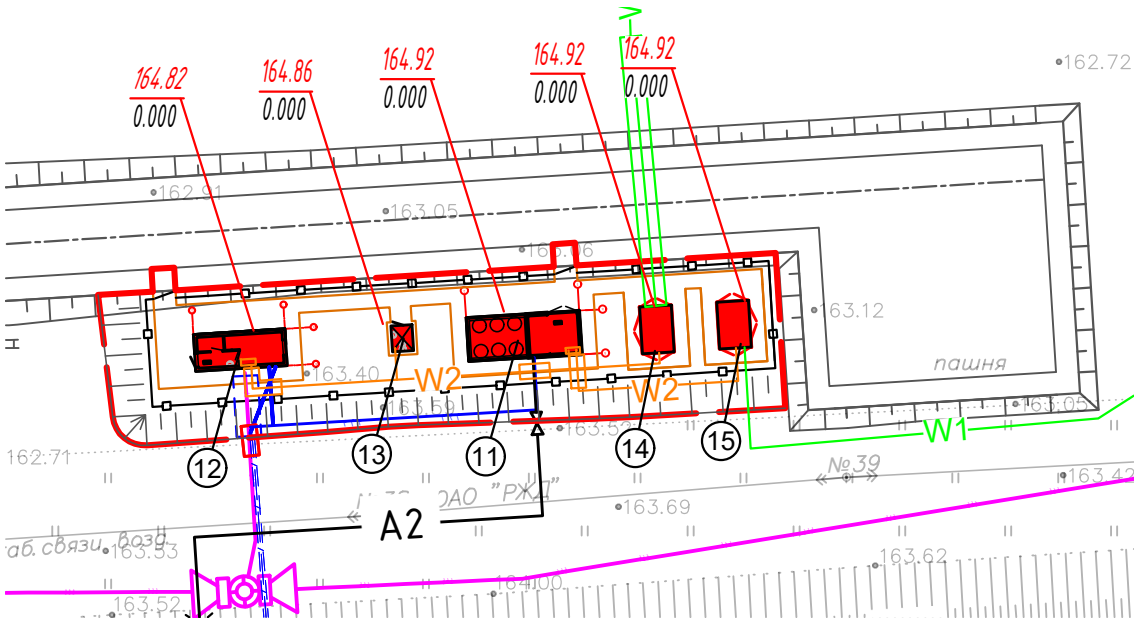

1. Система высот Балтийская 1977 г.
2. Система координат местная.

Экспликация зданий и сооружений

Номер на плане	Наименование	Примечание
11	Модульная компрессорная	Проектируемое
12	Модульный пункт обогрева	Проектируемое
13	Туалетный модуль	Проектируемое
14,15	Трансформаторная подстанция	Проектируемое

Условные обозначения

	Граница проектирования благоустройства
	Проектируемое здание
	Проектируемые сети связи
	Проектируемая сеть воздуховода
WK	Проектируемая кабельная линия электропередач
W1 / W2	Проектируемые электрические сети

Взам. инв. №

Подп. и дата

Инв. № подл.

Изм.	Кол.уч	Лист	№док.	Подпись	Дата
Разраб.		Бурайкин			09.26
Проверил		Сундеев			09.26
Н. контр.		Грошев			09.26

1439/2025/4-ГП.СП-5.3

Инфраструктура индустриального парка «Этилен-600», Железнодорожная инфраструктура. Этап №4. Строительство железнодорожных путей общего пользования (приемоотправочный парк ст. Круглое Поле)

Этап №4


Стадия	Лист	Листов
Р	5.3	

Сводный план сетей инженерно-технического обеспечения М 1:500 Площадка размещения зданий в районе стрелочных переводов: №302, 304, 306, 308

ГРАДО ПРОЕКТ

Формат А4

Площадка размещения зданий в районе стрелочных переводов: №5, 7, 35, 37, 39, 41

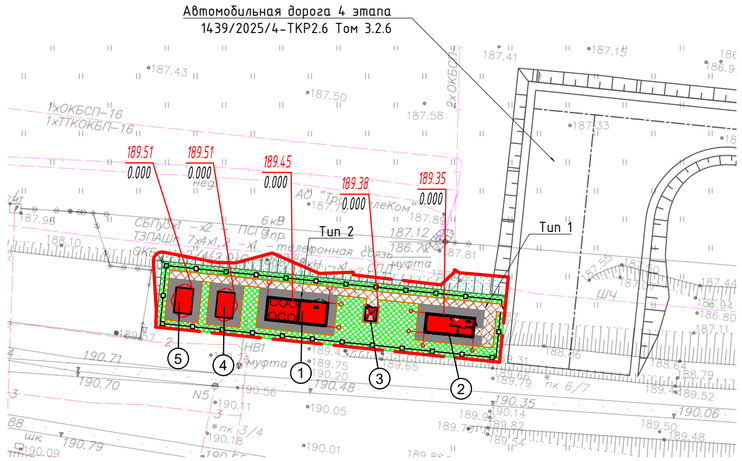

Ведомость тротуаров, дорожек и площадок

Поз.	Наименование	Тип	Площадь покрытия, м²	Примечание
1	Тротуар (асфальтобетон)	1	50,34	
2	Отмостка (асфальтобетон)	2	75,04	

Ведомость элементов озеленения

Поз.	Наименование породы или вида насаждения	Возраст, лет	Площадь покрытия, м²	Примечание
1	Газон посевной		165,00	м²
2	Укрепление откосов посевом трав		54,55	м²

Ведомость бортовых камней

Поз.	Наименование	Тип	пог.м	Примечание
1	БР 100.20.18 ГОСТ 32961-2014	1	129,50	


Экспликация зданий и сооружений

Номер на плане	Наименование	Примечание
1	Модульная компрессорная	Проектируемое
2	Модульный пункт обогрева	Проектируемое
3	Туалетный модуль	Проектируемое
4,5	Трансформаторная подстанция	Проектируемое


Условные обозначения

	Граница проектирования благоустройства
	Проектируемое здание
	Тротуар из асфальтобетона
	Отмостка
	Газон
	Откос
	Бортовой камень БР100.20.8
	Бровка земляного полотна
	Ограждение l=93,70 м
	Калитка 1,50 м


Установка бортового камня БР100.20.8 в сопряжении отмостки и газона

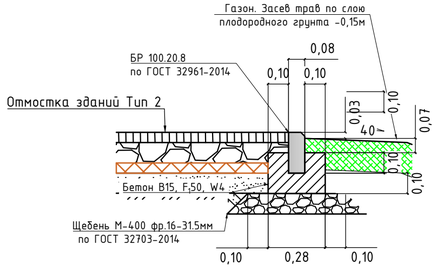

Установка бортового камня БР100.20.8 в сопряжении тротуара и газона

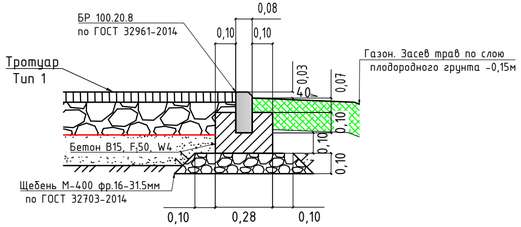

Укрепление откосов

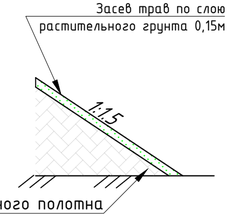

1. Система высот Балтийская 1977 г.
2. Система координат местная.
3. Размеры даны в метрах

Изм.	Кол.уч.	Лист	№док.	Подпись	Дата
Разраб.		Бурайкин			09.26
Проверил		Сундеев			09.26
Н. контр.		Грошев			09.26

1439/2025/4-ГП.СП-6.1

Инфраструктура индустриального парка «Этилен-600», Железнодорожная инфраструктура. Этап №4. Строительство железнодорожных путей общего пользования (приемоотправочный парк ст. Круглое Поле)

Этап №4

Стадия	Лист	Листов
Р	6.1	

План благоустройства М 1:500. Площадка размещения зданий в районе стрелочных переводов: №5, 7, 35, 37, 39, 41

ГРАДО ПРОЕКТ


Взам. инв. №

Подп. и дата

Инв. № подл.

Формат А4х3

Площадка размещения зданий в районе стрелочных переводов: №1, 3

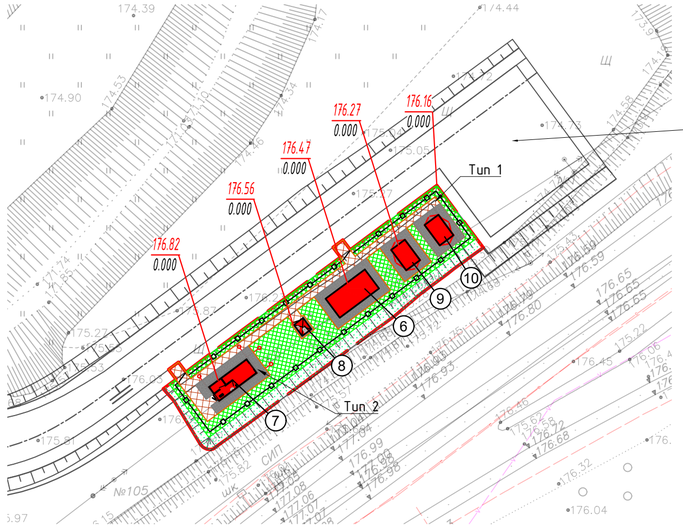

Автомобильная дорога 4 этапа
1439/2025/4-ТКР2.6 Том 3.2.6

Ведомость тротуаров, дорожек и площадок

Поз.	Наименование	Тип	Площадь покрытия, м²	Примечание
1	Тротуар (асфальтобетон)	1	55,66	
2	Отмостка (асфальтобетон)	2	72,04	

Ведомость элементов озеленения

Поз.	Наименование породы или вида насаждения	Возраст, лет	Площадь покрытия, м²	Примечание
1	Газон посевной		159.22	м²
2	Укрепление откосов посевом трав		70.91	м²

Ведомость бортовых камней

Поз.	Наименование	Тип	пог.м	Примечание
1	БР 100.20.18 ГОСТ 32961-2014	1	133	


Экспликация зданий и сооружений

Номер на плане	Наименование	Примечание
6	Модульная компрессорная	Проектируемое
7	Модульный пункт обогрева	Проектируемое
8	Туалетный модуль	Проектируемое
9,10	Трансформаторная подстанция	Проектируемое


Условные обозначения

	Граница проектирования благоустройства
	Проектируемое здание
	Тротуар из асфальтобетона
	Отмостка
	Газон
	Откос
	Бортовой камень БР100.20.8
	Бровка земляного полотна
	Ограждение l=90,70 м
	Калитка 1,50 м


Установка бортового камня БР100.20.8
в сопряжении отмостки и газона

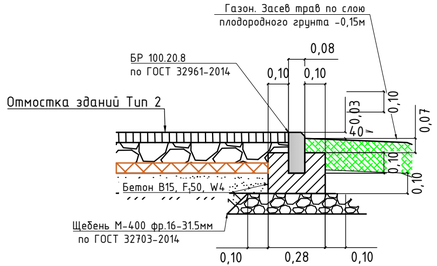

Установка бортового камня БР100.20.8
в сопряжении тротуара и газона

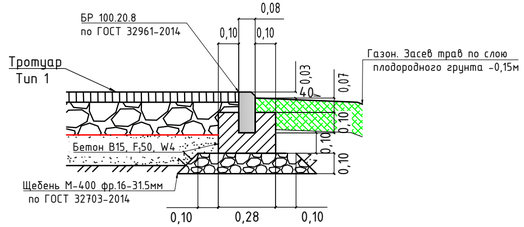

Укрепление откосов

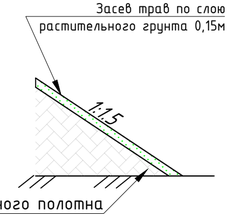

1. Система высот Балтийская 1977 г.
2. Система координат местная.
3. Размеры даны в метрах

Изм.	Кол.уч.	Лист	№док.	Подпись	Дата
Разраб.		Бурайкин			09.26
Проверил		Сундеев			09.26
Н. контр.		Грошев			09.26

1439/2025/4-ГП.СП-6.2

Инфраструктура индустриального парка «Этилен-600», Железнодорожная инфраструктура. Этап №4. Строительство железнодорожных путей общего пользования (приемоотправочный парк ст. Круглое Поле)

Этап №4

Стадия	Лист	Листов
Р	6.2	

План благоустройства М 1:500. Площадка размещения зданий в районе стрелочных переводов: №1, 3

ГРАДО ПРОЕКТ


Взам. инв. №

Подп. и дата

Инв. № подл.

Формат А4х3

Площадка размещения зданий в районе стрелочных переводов: №302, 304, 306, 308

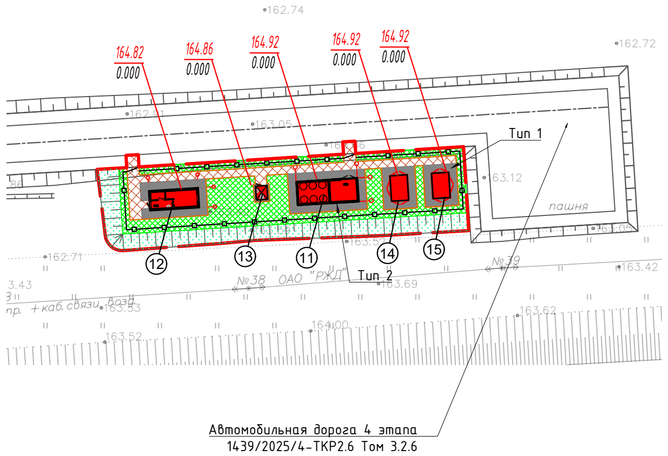

Автомобильная дорога 4 этапа
1439/2025/4-ТКР2.6 Том 3.2.6

Ведомость тротуаров, дорожек и площадок

Поз.	Наименование	Тип	Площадь покрытия, м²	Примечание
1	Тротуар (асфальтобетон)	1	57,14	
2	Отмостка (асфальтобетон)	2	75,04	

Ведомость элементов озеленения

Поз.	Наименование породы или вида насаждения	Возраст, лет	Площадь покрытия, м²	Примечание
1	Газон посевной		162.51	м²
2	Укрепление откосов посевом трав		106.61	м²

Ведомость бортовых камней

Поз.	Наименование	Тип	пог.м	Примечание
1	БР 100.20.18 ГОСТ 32961-2014	1	136	


Экспликация зданий и сооружений

Номер на плане	Наименование	Примечание
11	Модульная компрессорная	Проектируемое
12	Модульный пункт обогрева	Проектируемое
13	Туалетный модуль	Проектируемое
14,15	Трансформаторная подстанция	Проектируемое


Условные обозначения

	Граница проектирования благоустройства
	Проектируемое здание
	Тротуар из асфальтобетона
	Отмостка
	Газон
	Откос
	Бортовой камень БР100.20.8
	Бровка земляного полотна
	Ограждение l=90,70 м
	Калитка 1,50 м


Установка бортового камня БР100.20.8
в сопряжении отмостки и газона

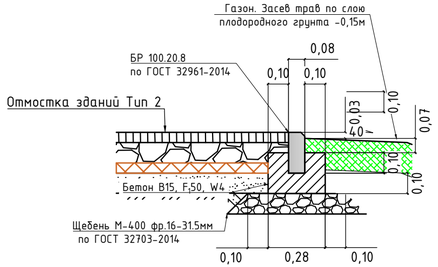

Установка бортового камня БР100.20.8
в сопряжении тротуара и газона

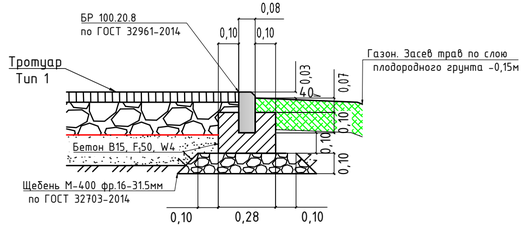

Укрепление откосов

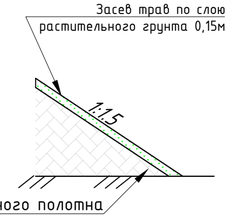

1. Система высот Балтийская 1977 г.
2. Система координат местная.
3. Размеры даны в метрах

						1439/2025/4-ГП.СП-6.3	
						Инфраструктура индустриального парка «Этилен-600», Железнодорожная инфраструктура. Этап №4. Строительство железнодорожных путей общего пользования (приемоотправочный парк ст. Круглое Поле)	
Изм.	Кол.уч.	Лист	№док.	Подпись	Дата		
Разраб.		Бурайкин			09.26	Этап №4	Стадия: Р; Лист: 6.3; Листов:
Проверил		Сундеев			09.26		
Н. контр.		Грошев			09.26	План благоустройства М 1:500. Площадка размещения зданий в районе стрелочных переводов: №302, 304, 306, 308	ГРАДО ПРОЕКТ

Взам. инв. №
Подп. и дата
Инв. № подл.

Формат А4х3